
512 D1 30MVA SIEMENS	C01R
MEDIDA B1.1	C02R
MEDIDA CALIDAD B1.1	C03R
542 AP12R LIBR_AP12R	C04R
552 FR12R2 AEROPURT2	C05R
562 FR12R1 AEROPURT1	C06R
572 U.B. B1.1–B1.2	C07R
TRANSICIÓN B1.2	C08R
592 FO21R2 PRINTER2	C09R
602 FO21R1 PRINTER1	C10R
MEDIDA CALIDAD B1.2	C11R
MEDIDA B1.2	C12R
642 D2 30MVA SIEMENS	C14R

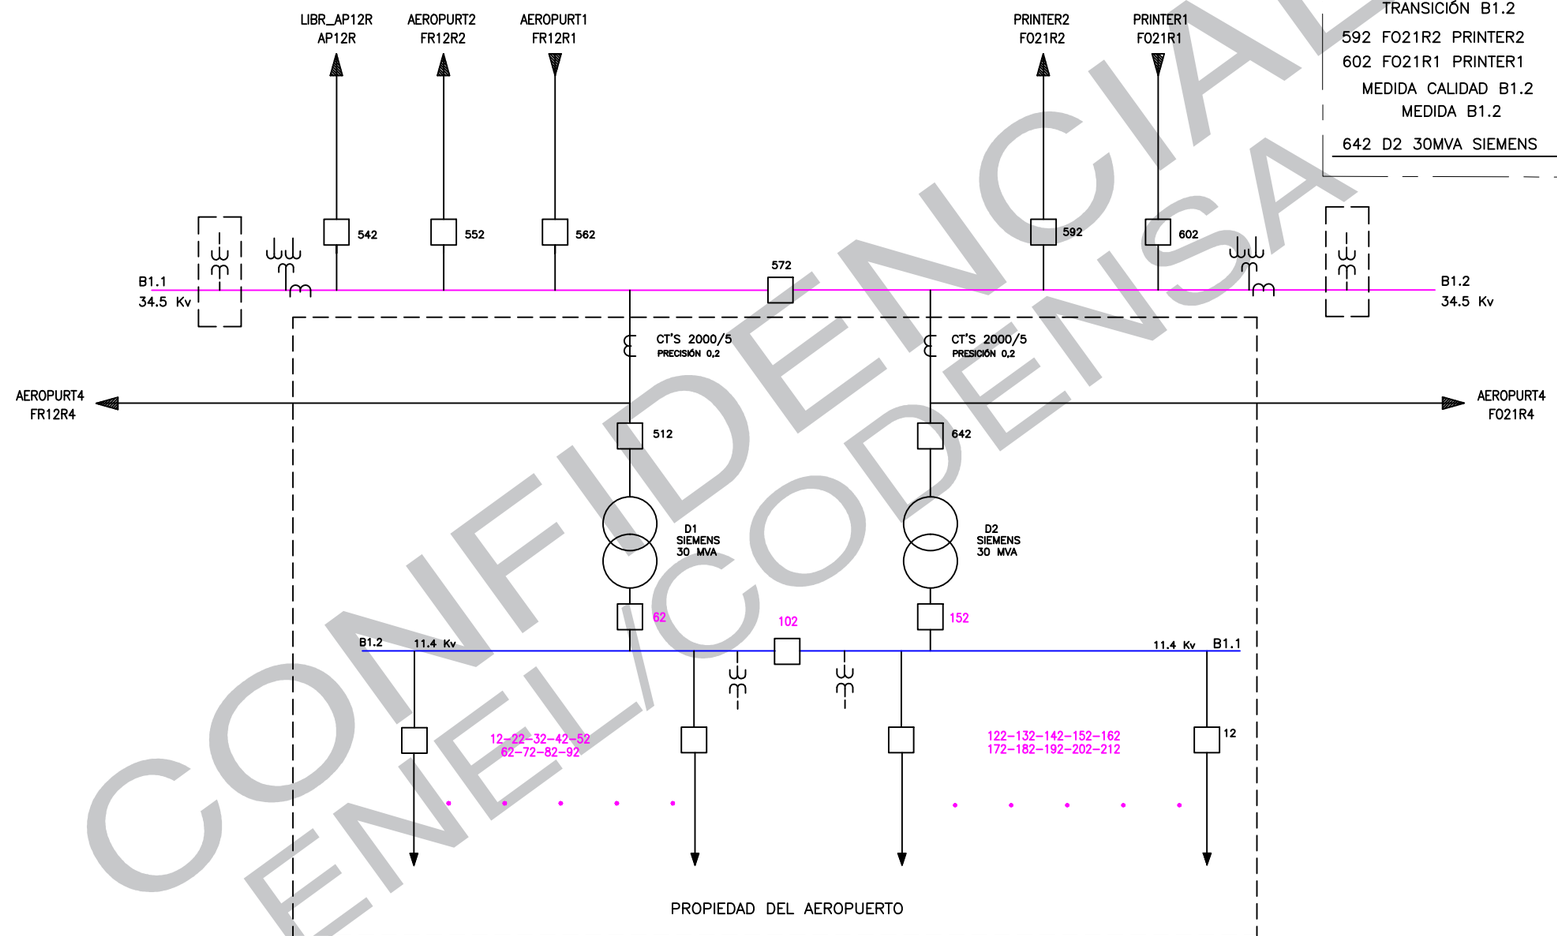

CONFIDENCIAL
ENEL/CODENSA

codensa Grupo Enel	Unidad Organizativa Administración Información Técnica Col.	REVISION No. 2 FECHA: MAYO/2020 ARCHIVO: AEROPU_TP.DWG \\COLCOD09FS01\FileServer\CONTROL UNIFILARES	DIAGRAMA UNIFILAR SUBESTACION AEROPUE_TP AEROPUERTO EL DORADO TERMINAL DE PASAJEROS AV CALLE 26 N° 115.–10 CODIGO: AP	136 HOJA: 1 DE: 1