


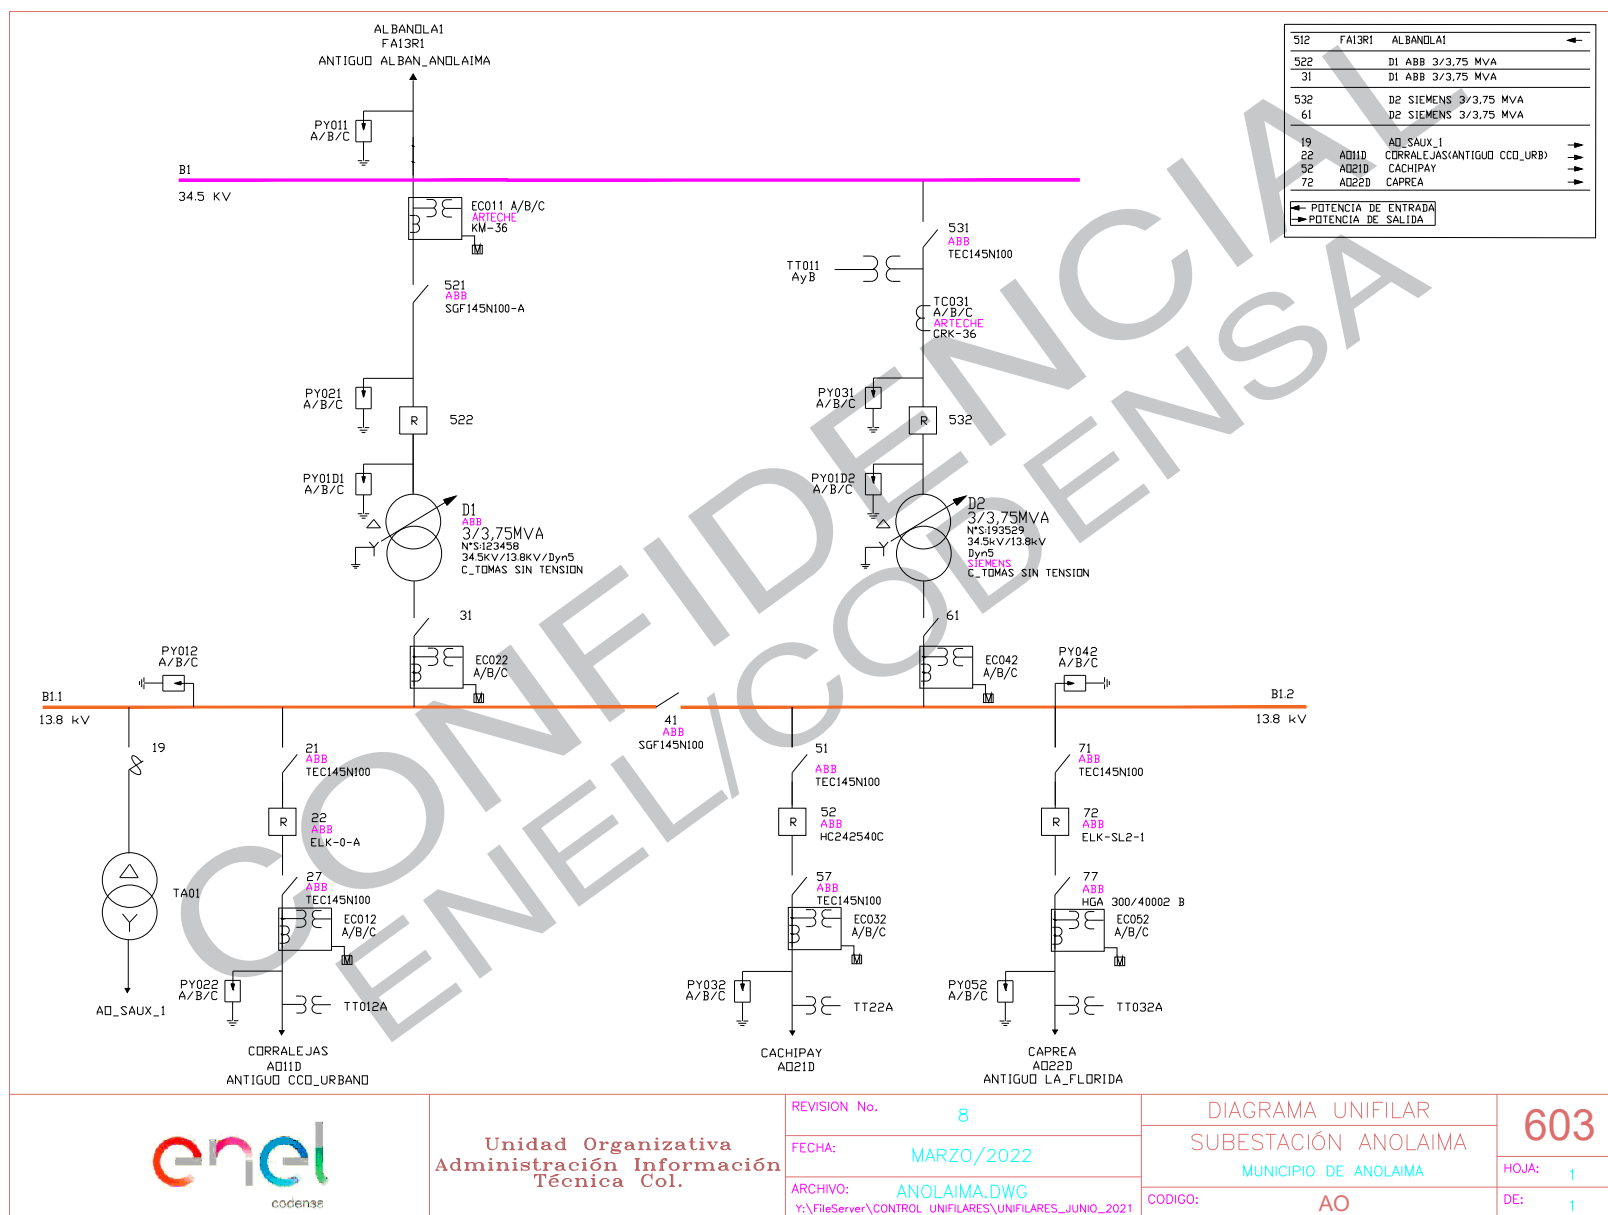

Unidad Organizativa
Administración Información
Técnica Col.

REVISION No. 8
FECHA: MARZO/2022
ARCHIVO: ANOLAIMA.DWG
Y:\FileServer\CONTROL UNIFILARES\UNIFILARES_JUNIO_2021

DIAGRAMA UNIFILAR
SUBESTACIÓN ANOLAIMA
MUNICIPIO DE ANOLAIMA
CODIGO: AO

603

HOJA: 1
DE: 1