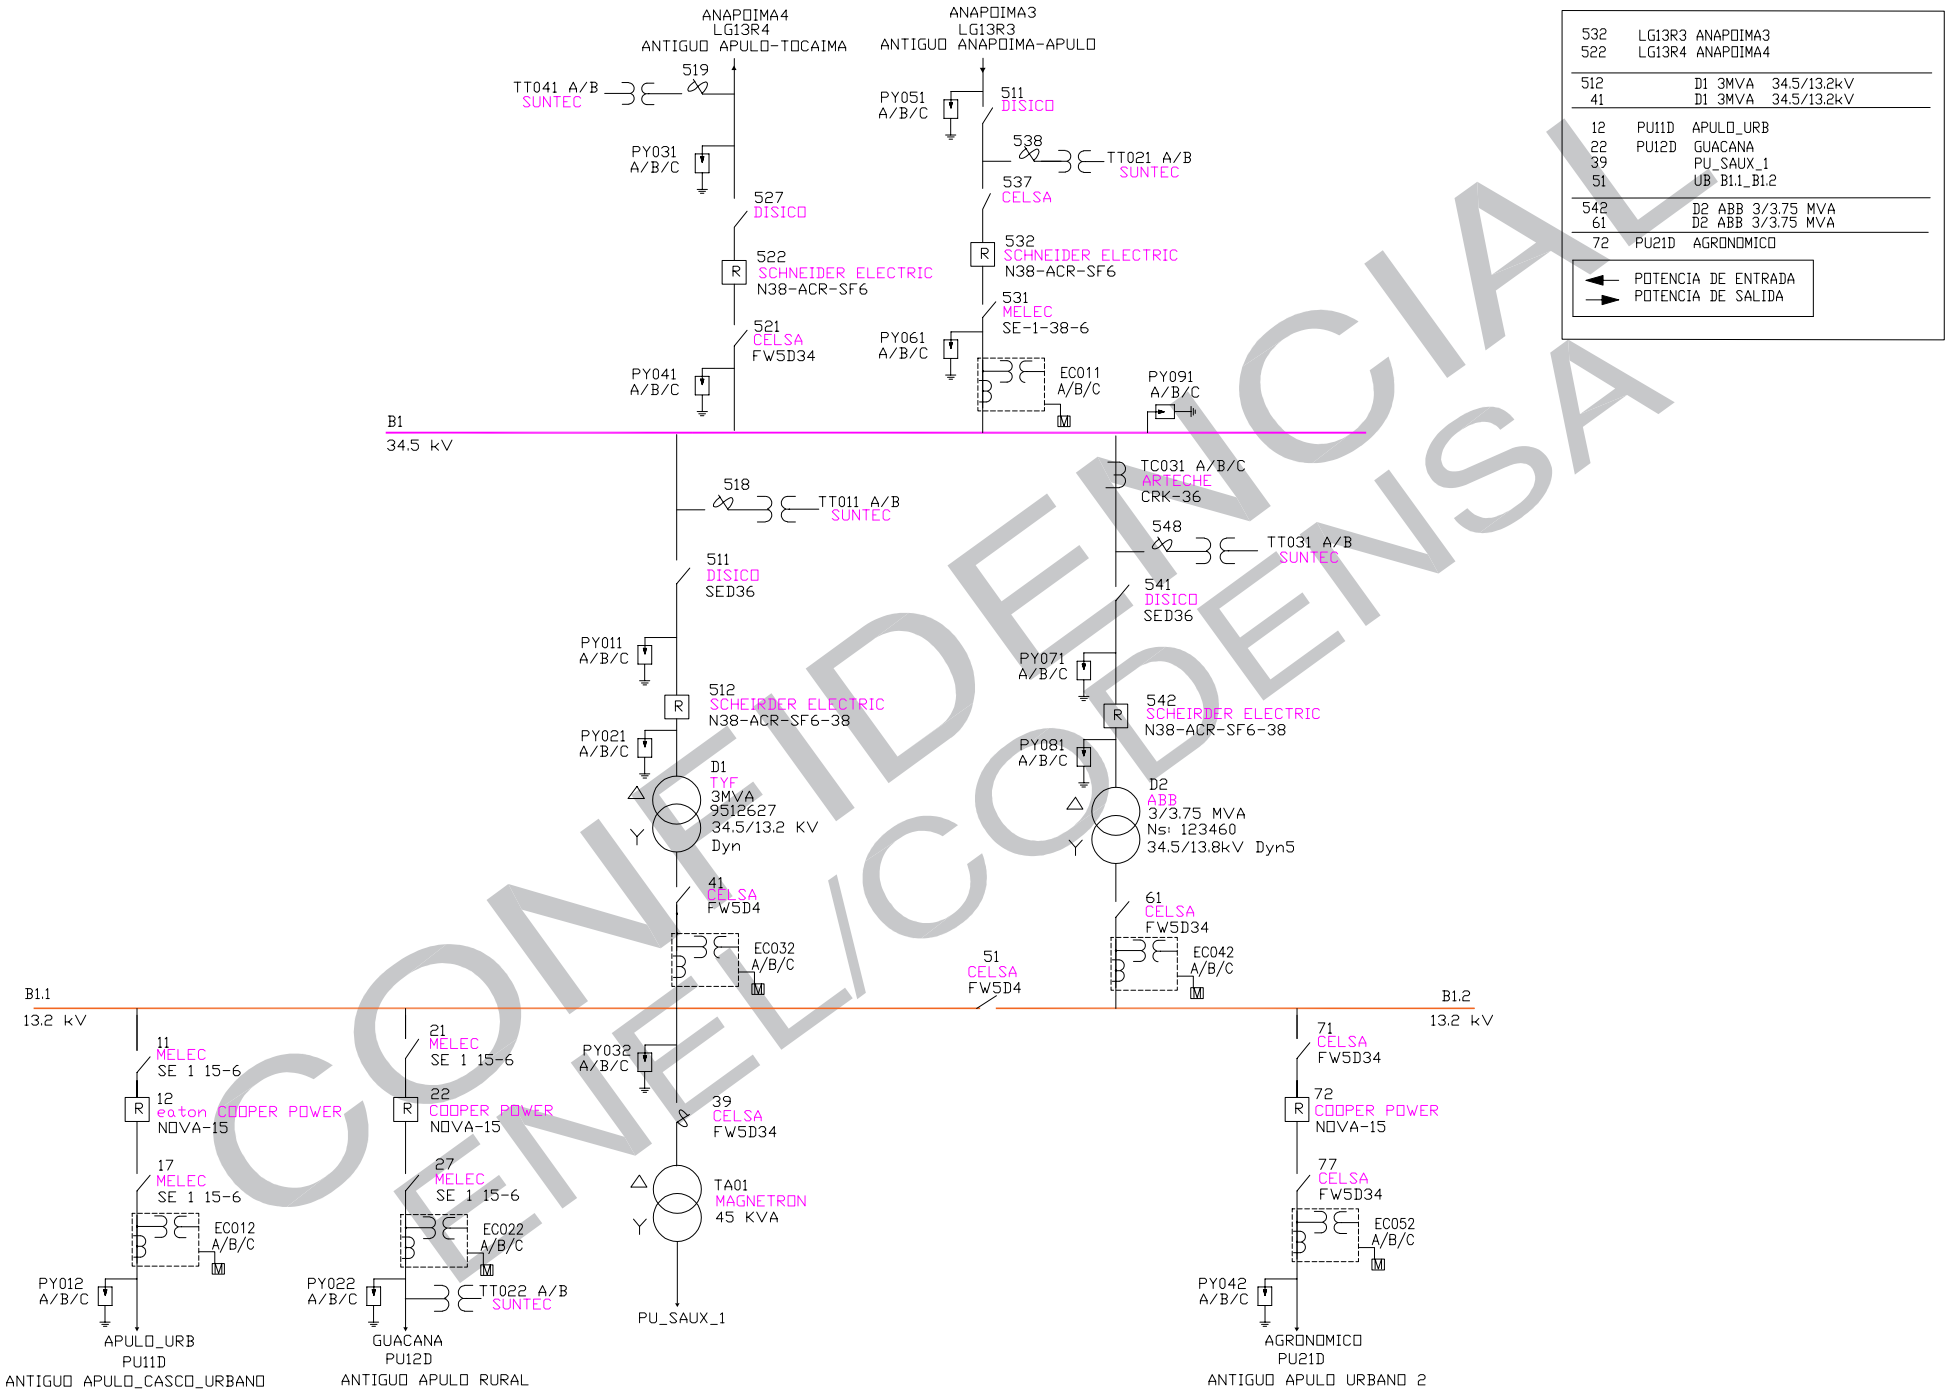


CONFIDENCIAL
ENEL/CODENSA

codensa

Unidad Organizativa
Administración Información
Técnica Col

| | |
|---|---|
| REVISION No. | 8 |
| FECHA: | JUNIO/2022 |
| ARCHIVO: | APULO.DWG |
| | C:\ESQUEMAS SUBESTACIONES\CONTROL UNIFILARES |

DIAGRAMA UNIFILAR
SUBESTACION APULO
MUNICIPIO DE APULO

CODIGO: PU

616

HOJA: 1

DE: 1