
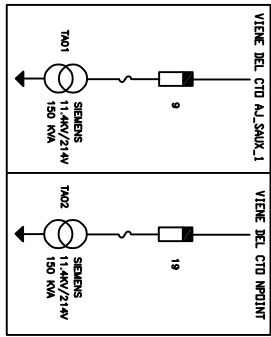


12	AJ21	BARRANCAS	C01
22	AJ22	LDS_CERROS	C02
32	AJ23	CEDRAL	C03
42		D2 MITSUBISHI 30 MVA	C04
52	AJ24	MILAN	C05
62	AJ25	BABILONIA	C06
72	AJ26	ALAMEDA	C07
82	AJ27	INPOINT	C08
92	AJ28	RANGEL	C09
		MEDIDA_B1.2	C10
112		UB B1.1-B1.2	C11
		MEDIDA_B1.1	C12
132	AJ11	ICATA	C13
142	AJ12	CANADA	C14
152	AJ13	GOLF	C15
162		D1 WEG 30 MVA	C16
172	AJ14	CONVENTOS	C17
182	AJ15	MARIELA	C18
192	AJ16	AJ_SAUJ_1	C19
202	AJ17	TOBERIN	C20
212	AJ18	SEGUVIA	C21

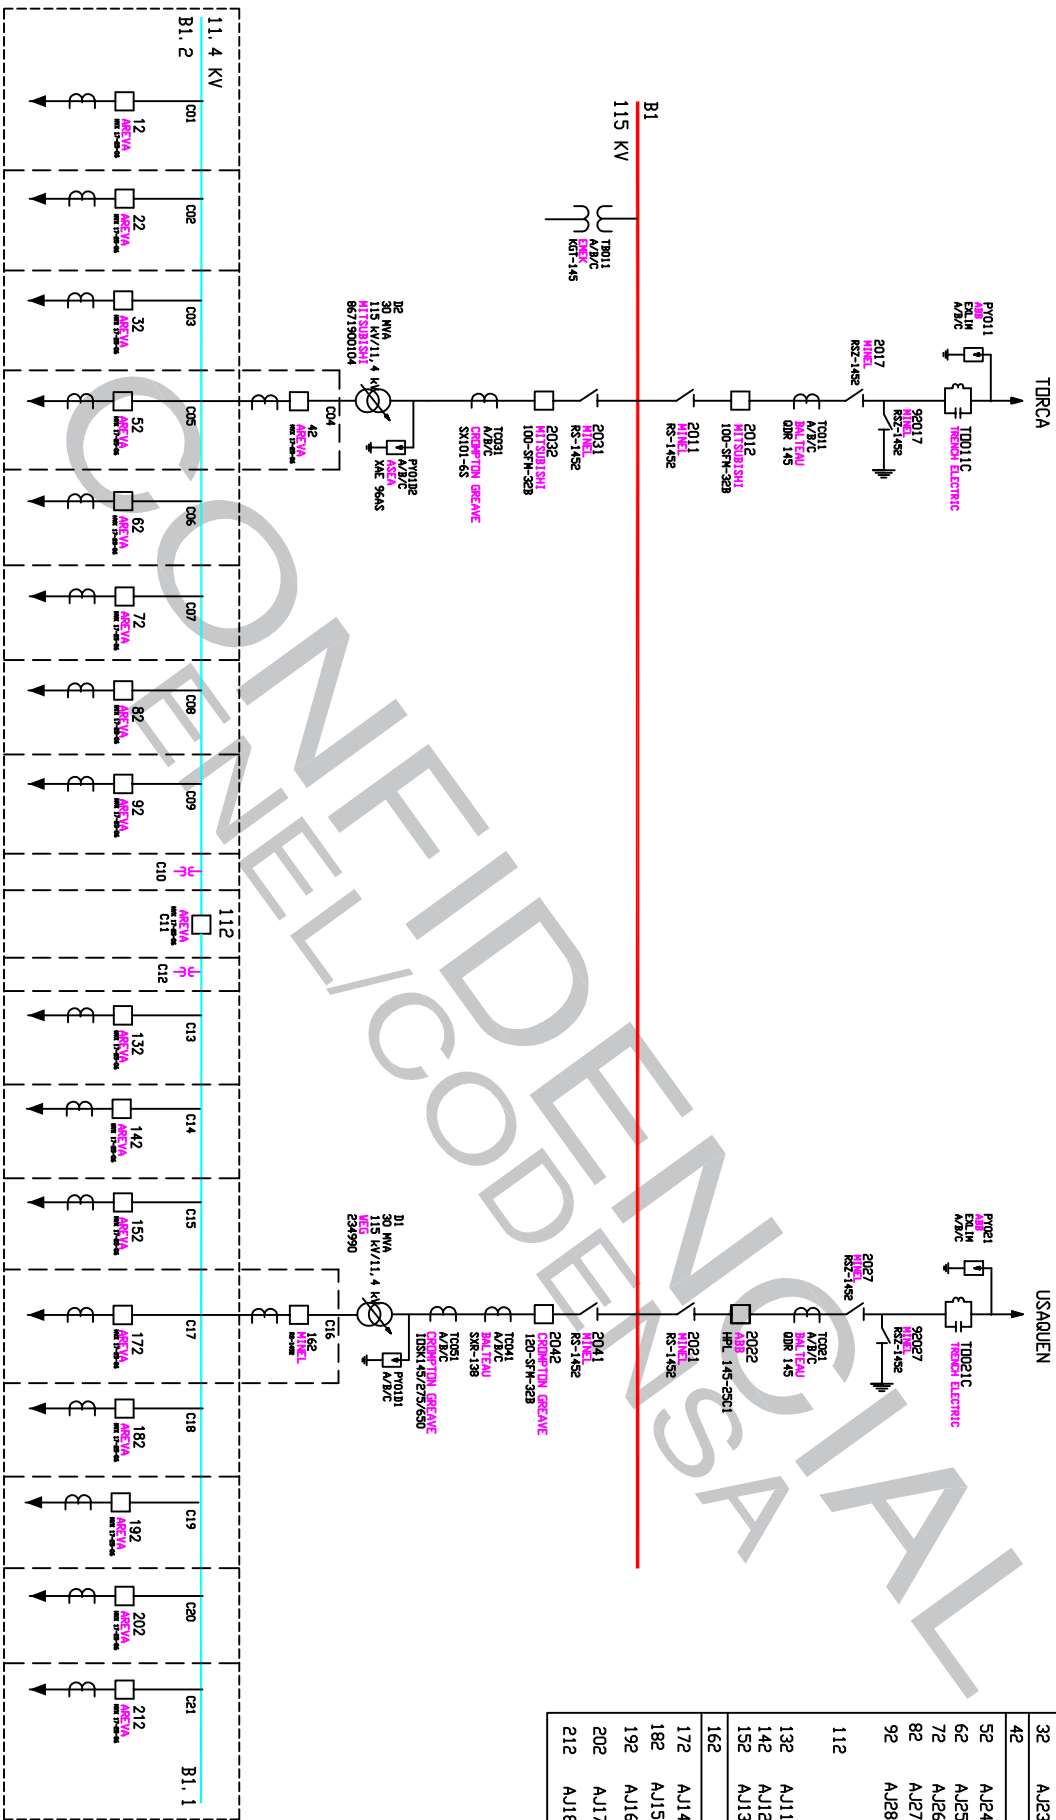

Unidad organizativa
Administración informática
Técnica Col.

REVISION NO. 20

FECHA: JUNIO/2022

ARCHIVO: ARANJUEZ.DWG
Y:\fisServer\CONTROL UNIFILARES\UNIFILARES_JUN20_2019

DIAGRAMA UNIFILAR

SUBESTACION ARANJUEZ
CRA 24 No. 159-80
TEL. 5261687/5261676 SIEMENS 6500

CODIGO: AJ