


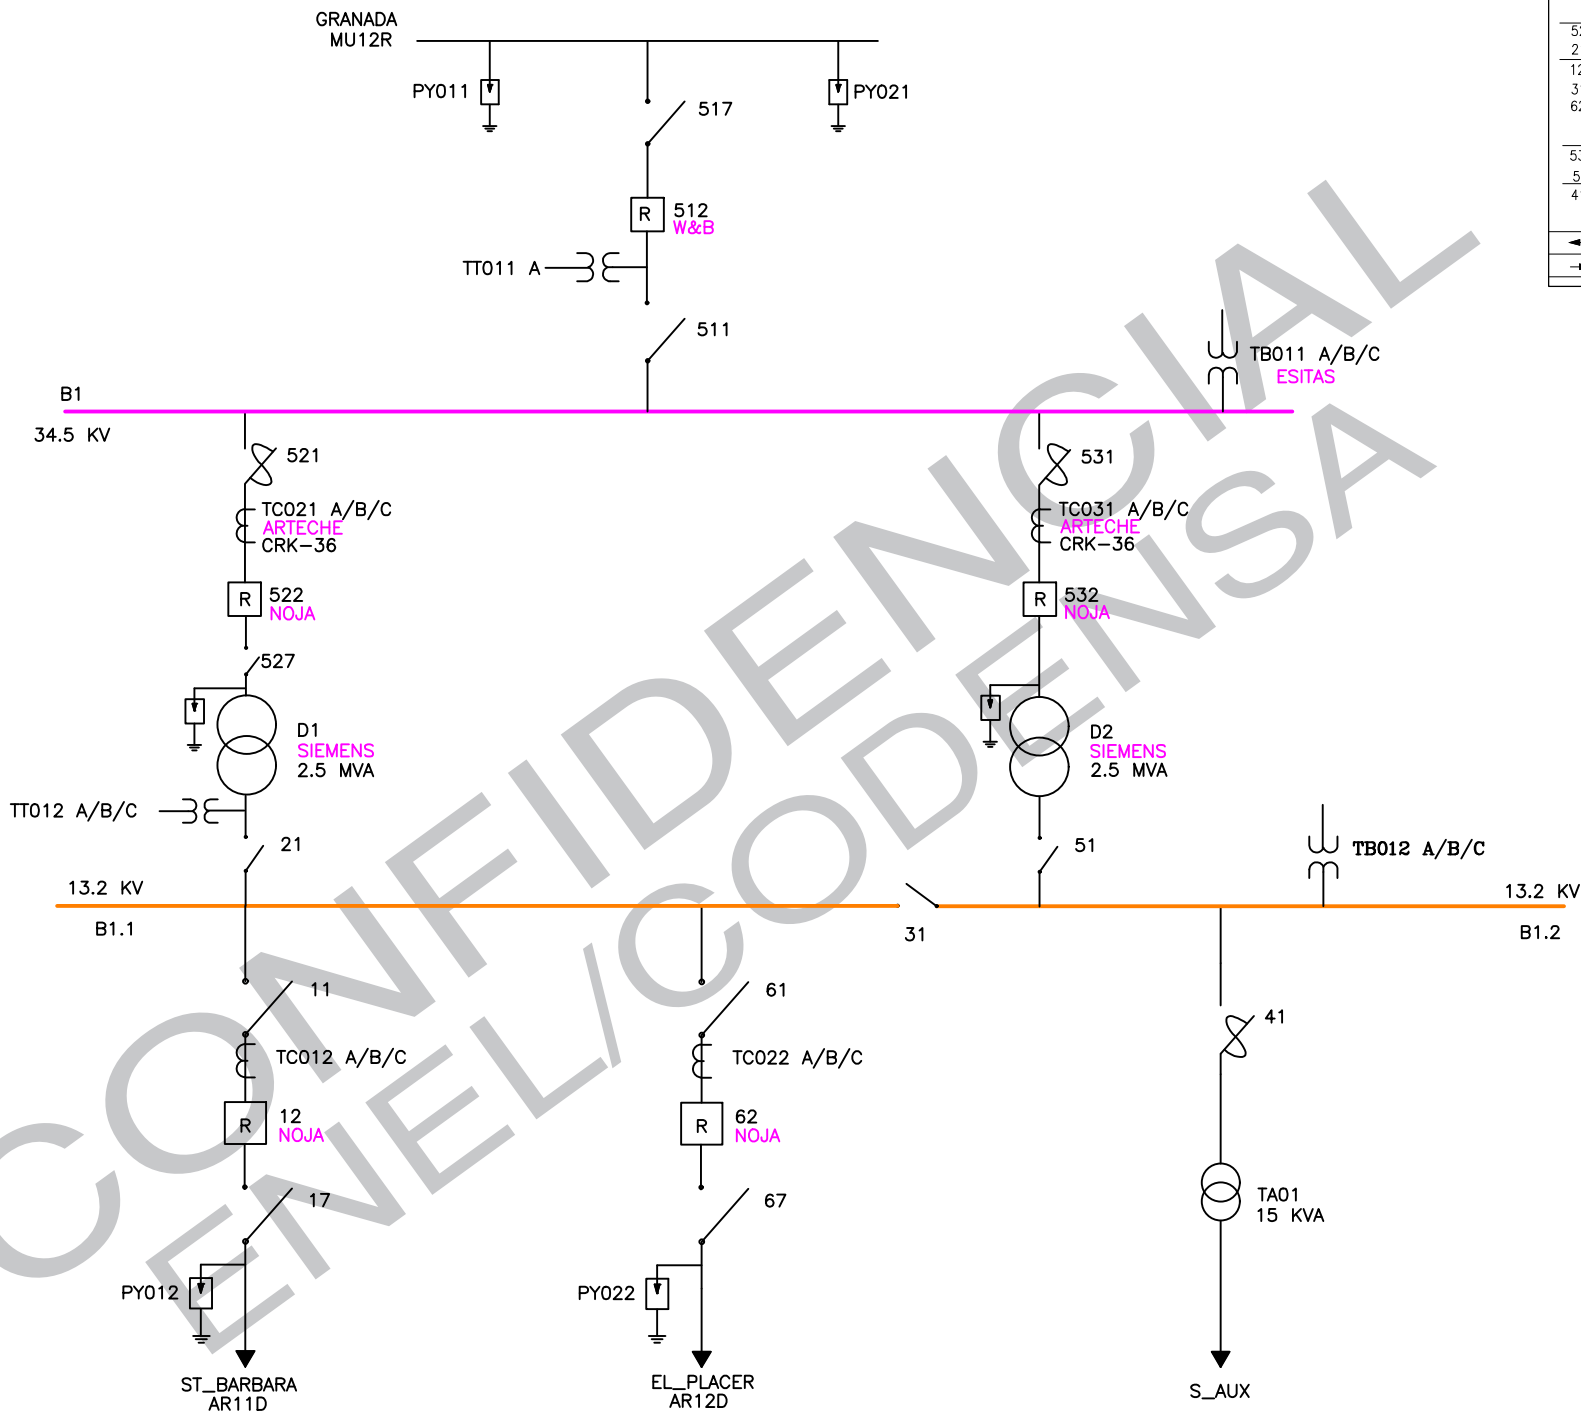

512	MU12R	GRANADA
		MEDIDA B1
522	D1	SIEMENS 2.5MVA
21	D1	SIEMENS 2.5MVA
12	AR11D	ST_BARBARA
31	ACOPL	B1.1-B1.2 13.2KV
62	AR12D	EL_PLACER
532	D2	SIEMENS 2.5MVA
51	D2	SIEMENS 2.5MVA
41	S_AUX	MEDIDA B1.2
← POTENCIA DE ENTRADA		
→ POTENCIA DE SALIDA		

C:\Users\Daniela\Desktop\Enel1.jPG

Unidad Organizativa
Administración Información
Técnica Col.

REVISION No.	11
FECHA:	ENERO/2022
ARCHIVO:	ARBELAEZ.DWG
	\\COLCOD09FS01\FileServer\CONTROL UNIFILARES

DIAGRAMA UNIFILAR	
SUBESTACION ARBELAEZ	
INSTALACIONES DEL ACUEDUCTO DEL MCIPIO DE ARBELAEZ	
CODIGO:	AR

63	
HOJA:	1
DE:	1