


512	FAIR1	EMPOCUNDI1	→
532	FAIR1	MOVAND1	→
532	DI SIEMENS 30VA	PRIMARIO	→
12	DI SIEMENS 30VA	SECUNDARIO	→
22	AD101	COMANDO	→
32	AD102	ESTAD10	→
542	DI SIEMENS 3/375MVA	PRIMARIO *	→
62	DI SIEMENS 3/375MVA	SECUNDARIO *	→
52	AD101	LASPIEDRAS	→
72	AD102	EL PORTAL	→
89	S_AUX		→
42	ACOPLE B11-B12	132KV	→
→ POTENCIA DE ENTRADA			
→ POTENCIA DE SALIDA			
* CAMBIADOR DE TORNOS PARA OPERAR SIN TENSION			

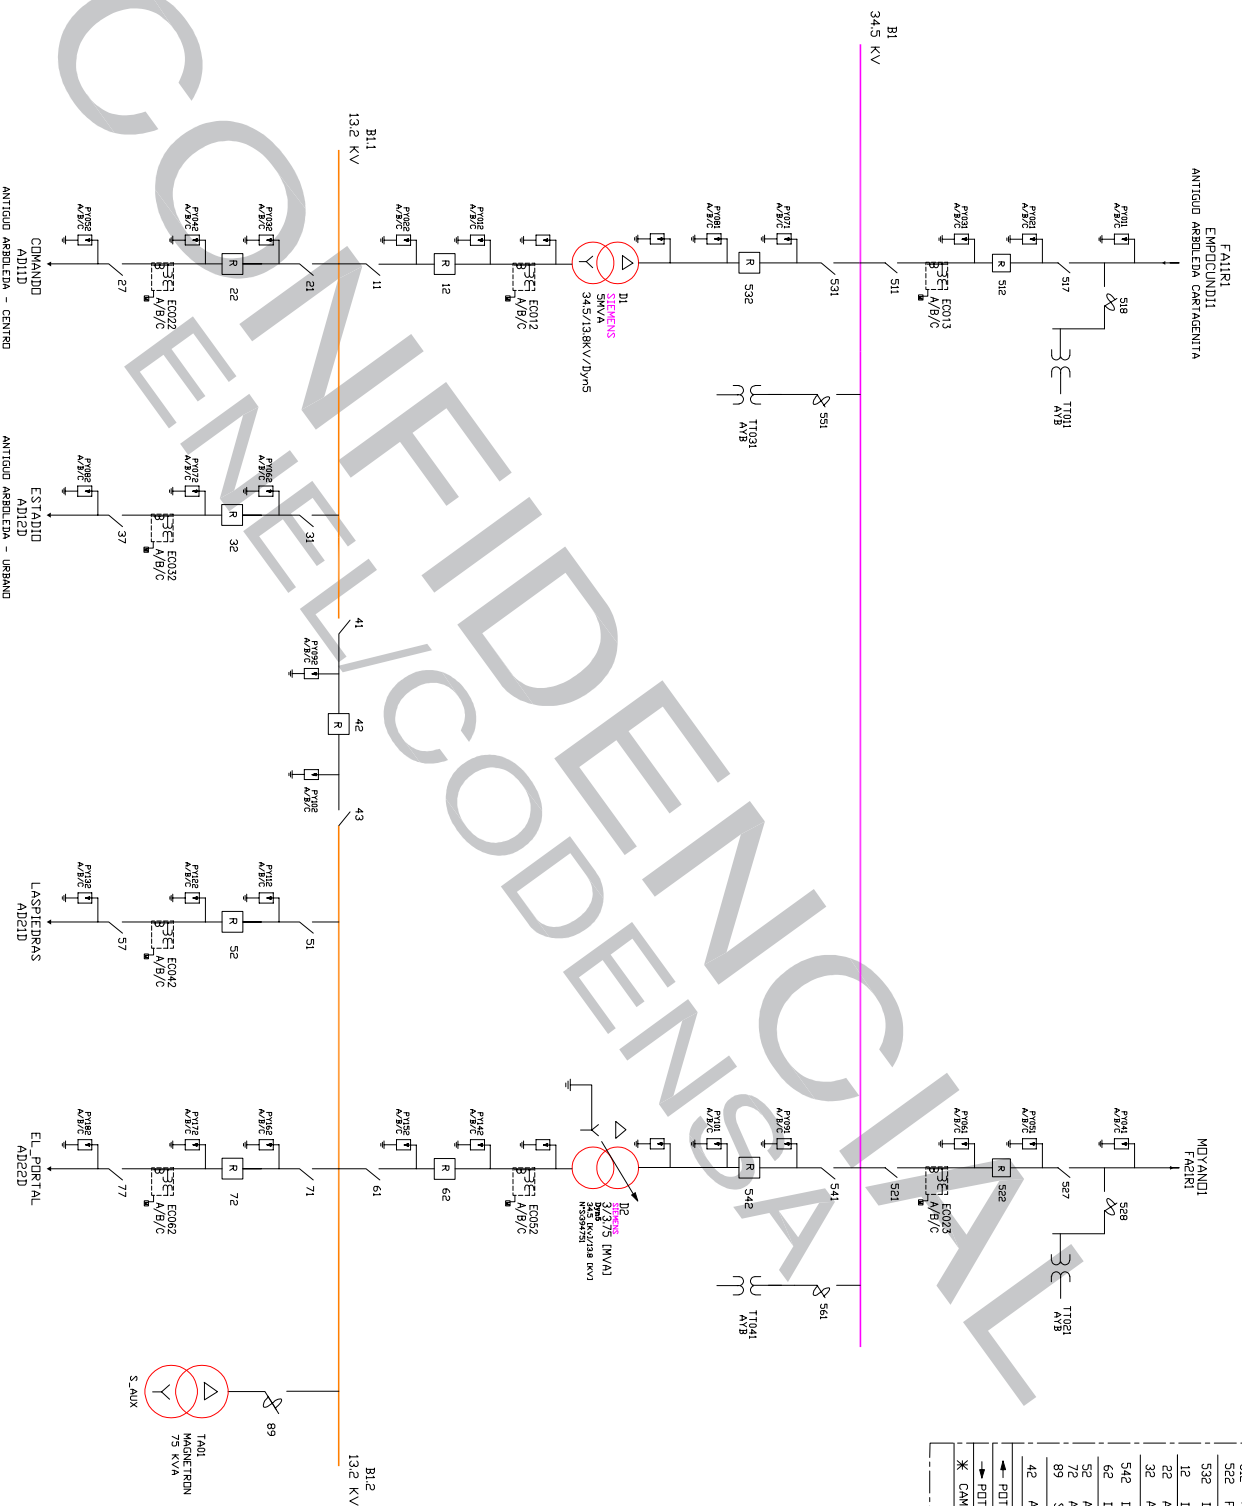

Unidad Organizativa
Administración Informacion
Técnica Col

REVISION No. 5
FECHA: NOVIEMBRE/2022
ARCHIVO: ARBOLEDA.DWG
Y:\FileServer\CONTROL UNIFILARES\UNIFILARES_SEPTIEMBRE_2020

DIAGRAMA UNIFILAR
SUBESTACION ARBOLEDA
MUNICIPIO DE ZIPAQUIRA

HOJA: 1
DE: 1

625