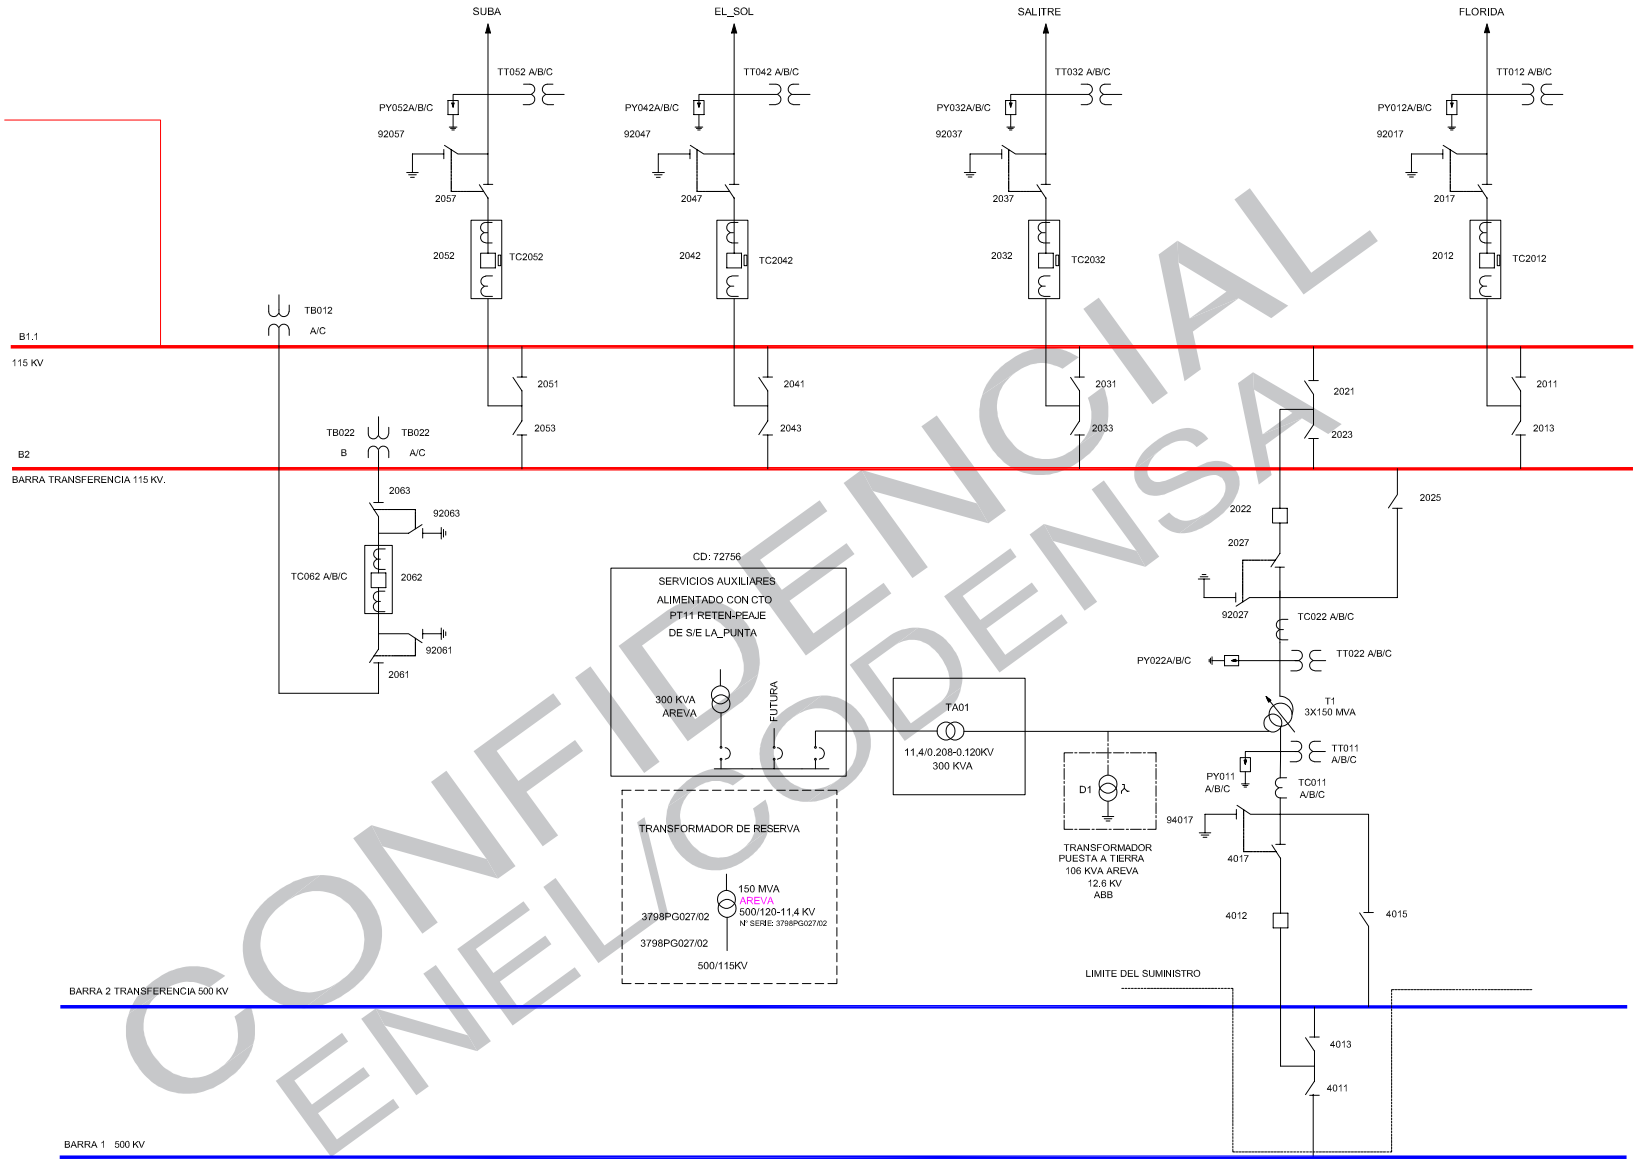


CONFIDENCIAL
ENEL/CODENSA

enel codensa	Unidad Organizativa Administración información Técnica Col.	REVISION No. 13	DIAGRAMA UNIFILAR SUBESTACION BACATA Z.R.TENJO VDA. LA PUNTA SECTOR JACALITO SIEMENS 6649	42
		FECHA: NOVIEMBRE/2022		HOJA: 1
		ARCHIVO: BACATA_1.DWG \\COLCOD09FS01\FileServer\CONTROL UNIFILARES	CODIGO: BT	DE: 2