



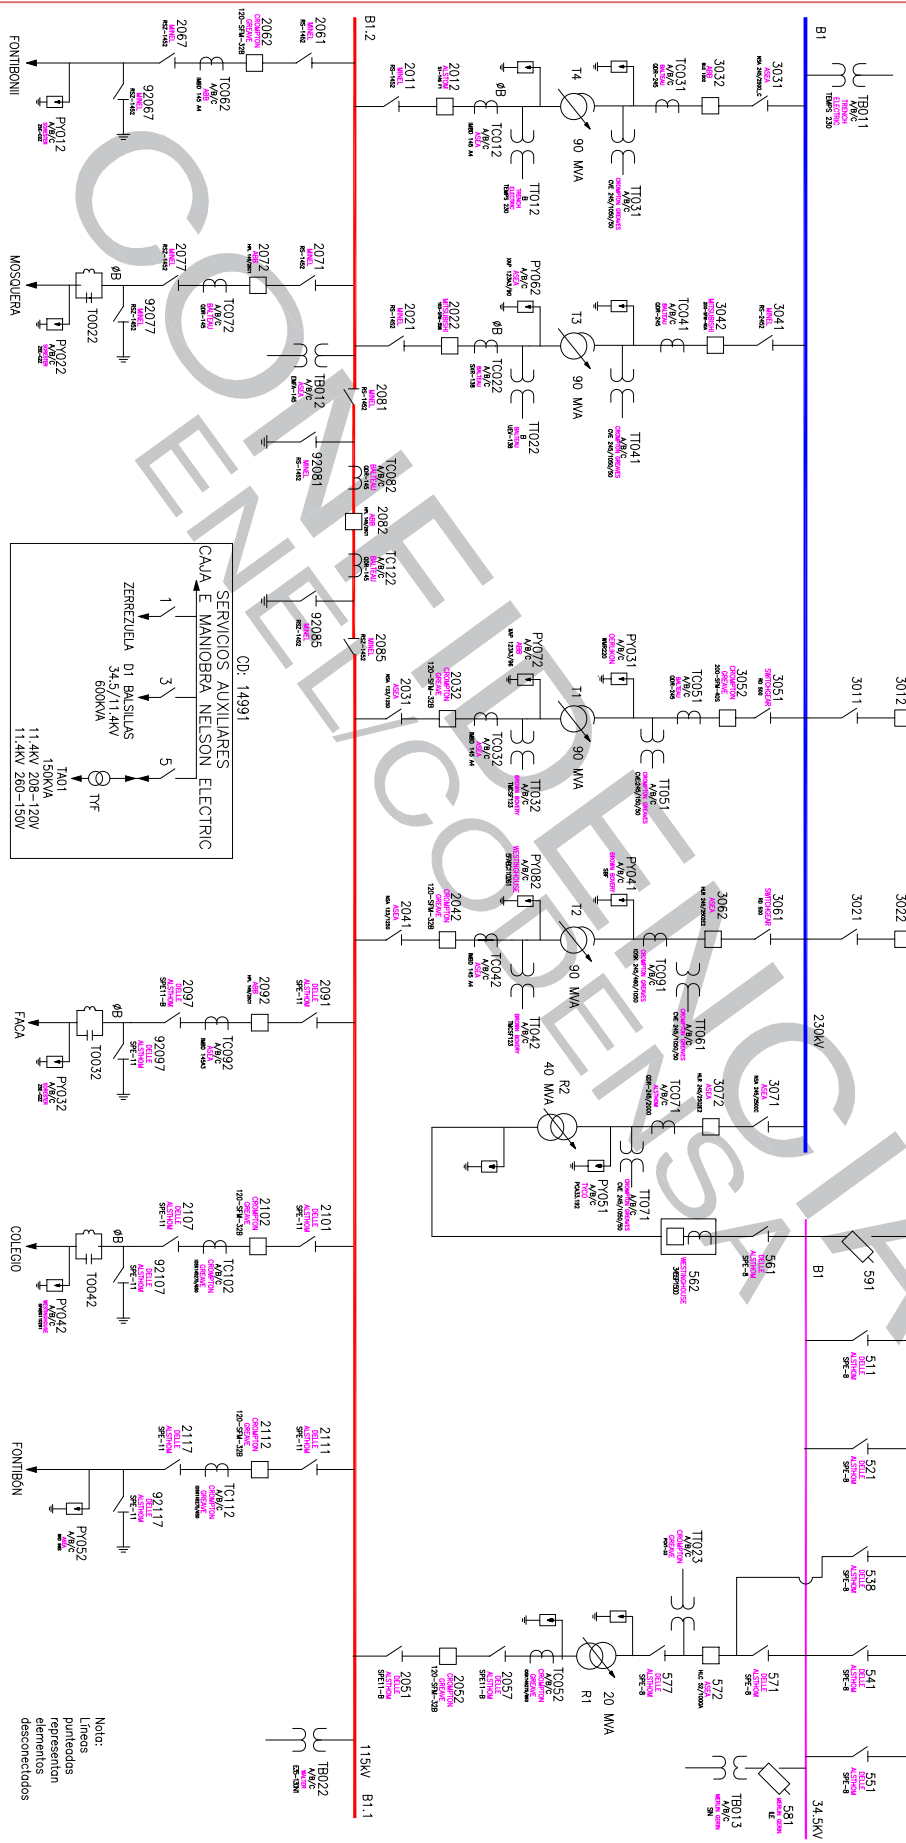

Nota:
Lineas
punteadas
representan
elementos
desconectados

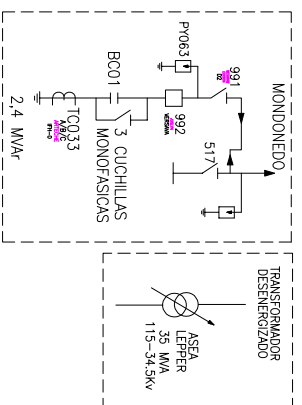

Unidad Organizativa
Administración Informativa
Técnica Col.

REVISION No.		DIAGRAMA UNIFILAR	
FECHA:	AGOSTO/2022	SUBESTACION BALSILLAS	3
ARCHIVO:	BALSILLAS.DWG	CALLETERA A LA MESA KM 14	HOLA: 1
Y:\FisServer\CONTROL UNIFILARES\UNIFILARES_AGO20_2019		TEL. 2574195/2674195 SIEMENS 6504	DE: 1
		CODIGO: BA	