
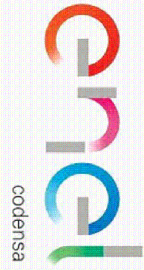
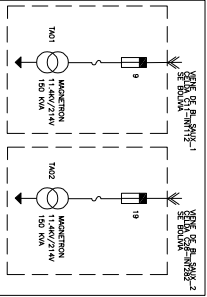
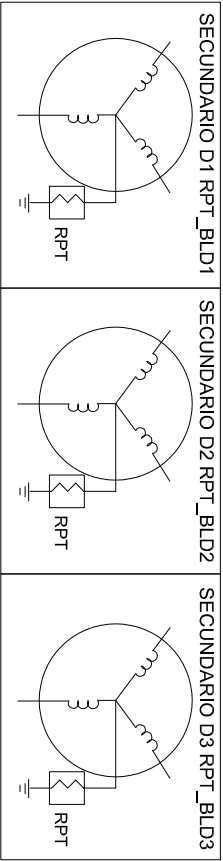


12	BL11	SAN_MARCOS	C01
22	BL12	AUMEDULLIN	C02
32	BL13	AMERIDONAL	C03
42	BL14	LIBRE_BL15	C04
52	BL15		C05
62	D1	OSAKA_30MVA	C06
72	BL16	CORTILLO	C07
82	BL17	SIBERIA	C08
92	BL18	MAORIGAL	C09
102	BL19	SAUTRAL	C10
112	BL1A	BL_SAIUX_1	C11
132		MEDIA-B1.1	C12
		UB B1.1_B1.2	C13
152		MEDIA-B1.2	C14
162	BL21	PO_OCCIDEN	C15
172	BL22	TV_CABLE	C16
182	BL23	FLORENCIA	C17
192	BL23	ZARZAMORA	C18
	BL23	CEREZOS	C19
202			C20
212			C21
232	UB B1.2_B1.3		C22
	MEDIA-B1.3		C23
242	BL26	PO_FLORIDA	C24
252	BL27	GARGES_NAV	C25
262	BL28	LA_PERLA	C26
272	BL29	BACHUE	C27
282	BL2A	BL_SAIUX_2	C28
292		UB B1.3_B1.4	C29
312	BL31	OMIGOLA	C30
322	BL32	EL_CEDRO	C31
332	BL33	VILLA_LUZ	C32
342	BL34	RONDEROETB	C33
352	BL35	LIBRE_B1.35	C34
			C35
362			C36
372	BL36	STA.ROSITA	C37
382	BL37	BOCHICALLI	C38
392	BL38	AFIPIO	C39
402	BL39	ENCATIVA	C40
412	BL4A	SIDAUO	C41

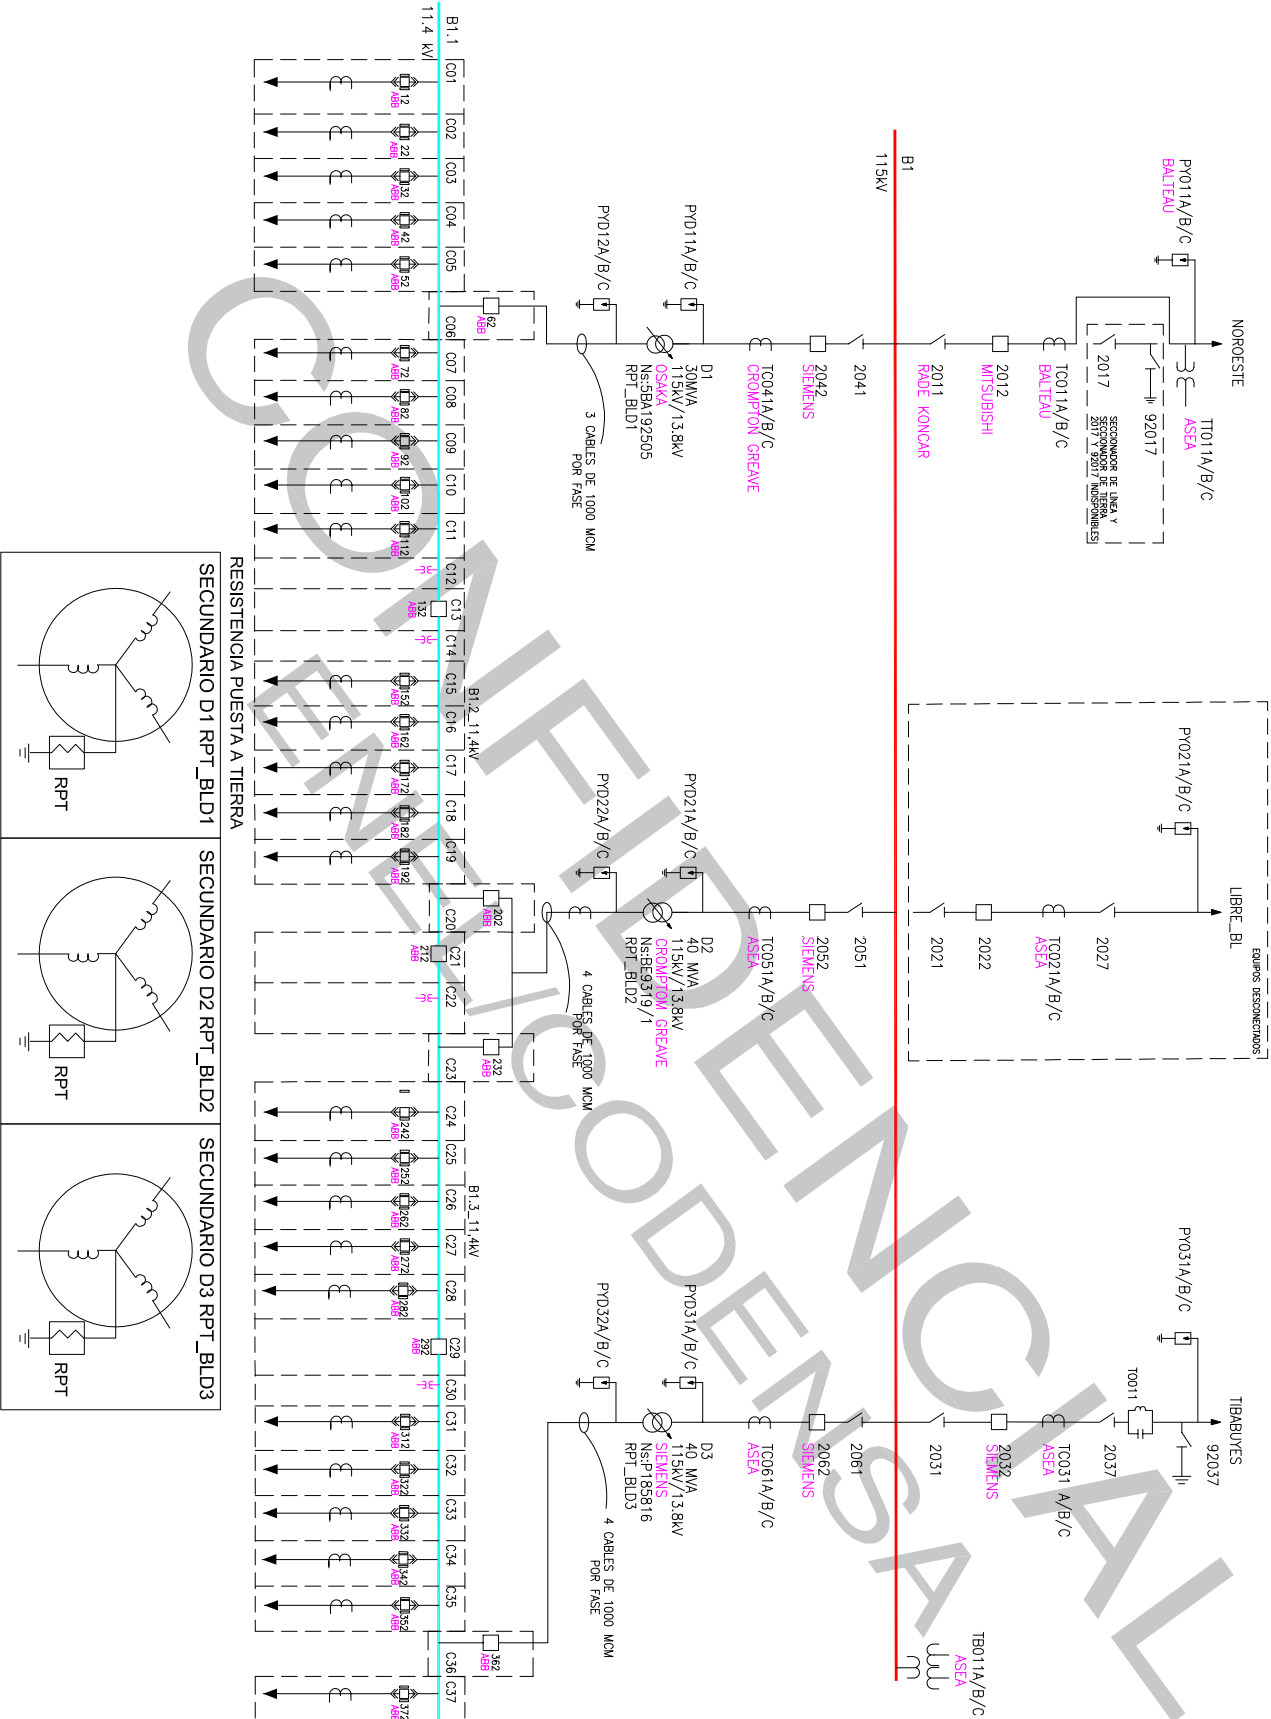

UNIDAD ORGANIZATIVA
ADMINISTRACION INFORMACION
TECNICA COL.

REVISION No. 34

FECHA: SEPTIEMBRE/2022

ARCHIVO: BOLIVIA.DWG
\\COLCOD09f501\FieServer\CONTROL UNIFILARES

CODIGO: BL

DIAGRAMA UNIFILAR

SUBESTACION BOLIVIA
AUTOPISTA MEDELIN CARRETA 100
TEL. 2275669 SIEMENS 6506

HOJA: 1

4