11	AC_SUAX_1	C01
22	CACICAZGO1	C02
32	CACICAZGO2	C03
42	CACICAZGO3	C04
52	CACICAZGO	C05
← POTENCIA ENTRADA		→ POTENCIA SALIDA

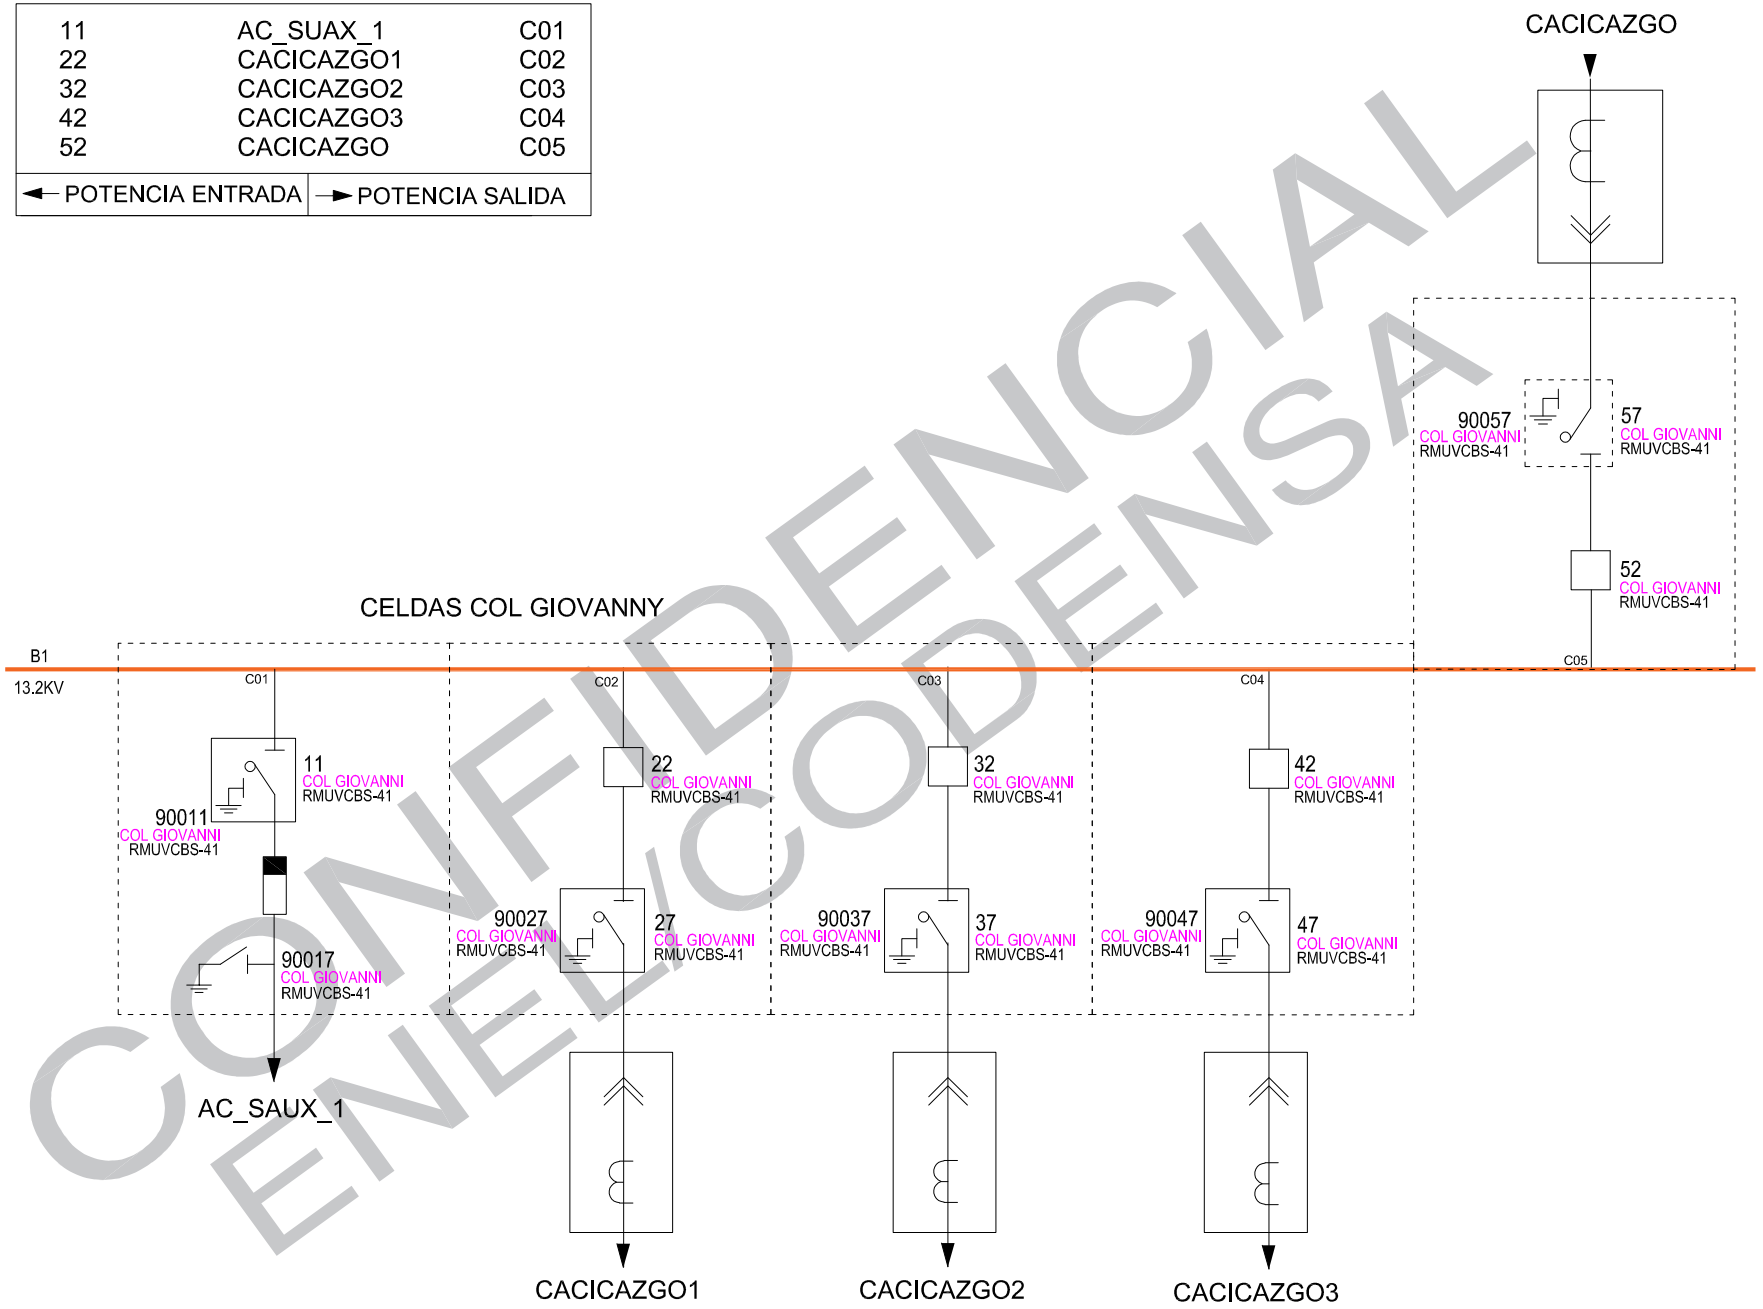

CONFIDENCIAL ENEL/CODENSA

codensa

Unidad Organizativa
Adminstraciòn Informaciòn
Técnica Col.

REVISION No.	2
FECHA:	MARZO/2022
ARCHIVO:	CACICAZGO.DWG
	Y:\\FileServer\CONTROL UNIFILARES\UNIFILARES_ABRIL_2020

DIAGRAMA UNIFILAR
SUBESTACIÓN SATÉLITE CACICAZGO
MPIO DE SUESCA CRA 5 N° 4-78
CODIGO: AC

174
HOJA: 1
DE: 1