


IA12R2	NOVOCIADO2	→
IA12R3	NOVOCIADO3	→
512	D2 SIEMENS 2MVA	→
522	D1 SUNTEC 5MVA	→
12	CY22 CERC_PIED	→
22	CY21 VARIANTE	→
31	D2 SIEMENS 2MVA	→
51	D2 SALIX 1B2.2	→
61	D1 SUNTEC 5MVA	→
72	CY12 LUCERNA	→
82	CY11 LA BALSA	→

→ POTENCIA DE SALIDA ← POTENCIA DE ENTRADA

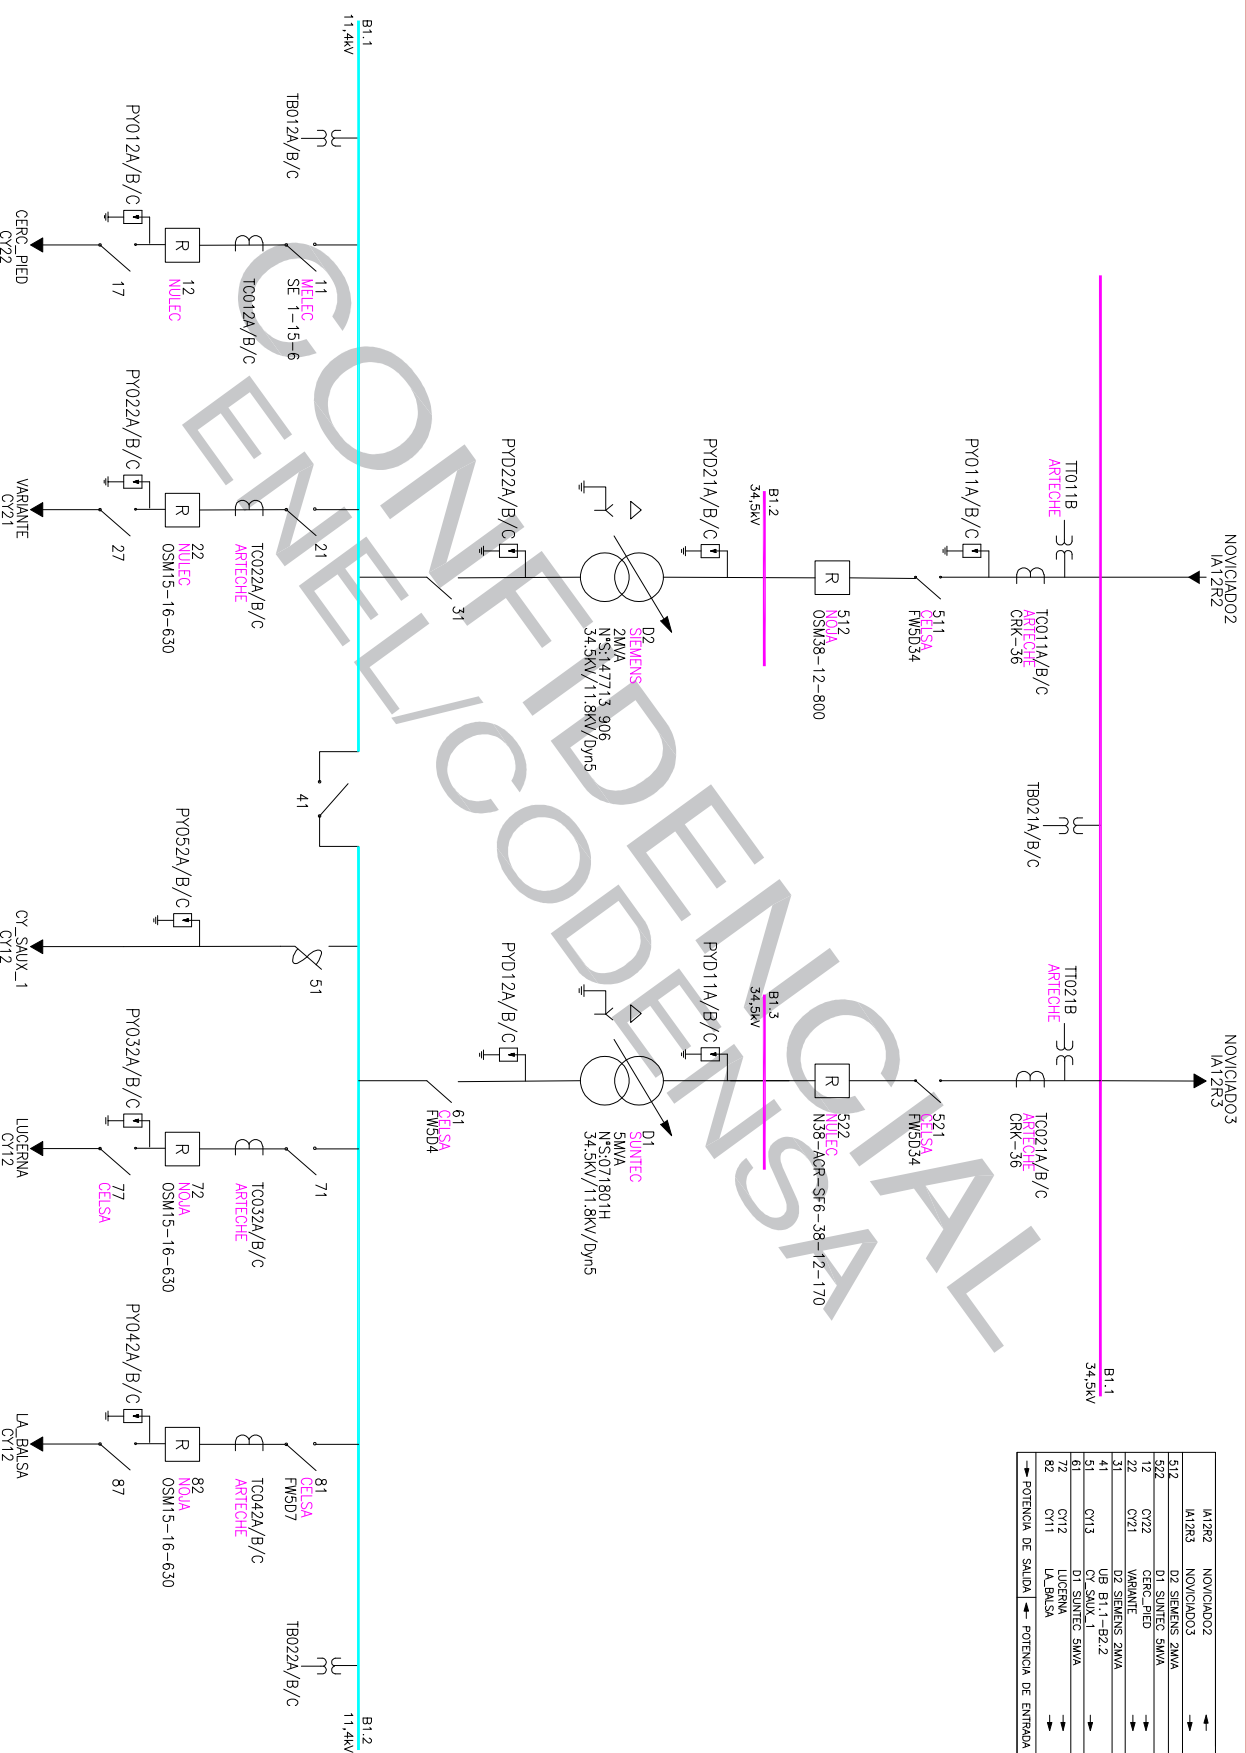

Unidad Organizativa
Administración Informática
Técnica Col.

REVISION No. 17
FECHA: ABRIL/2022
ARCHIVO: CACIQUE.DWG
Y:\FisServer\CONTROL_UNIFILARES\UNIFILARES_SEPTIEMBRE_2019

DIAGRAMA UNIFILAR
SUBESTACION CACIQUE
1 KM del municipio de Chilo en la vereda Cacique
200 metros hacia el costado izquierdo
de la Ma Chilo Coto

CODIGO: CY
DE: 1