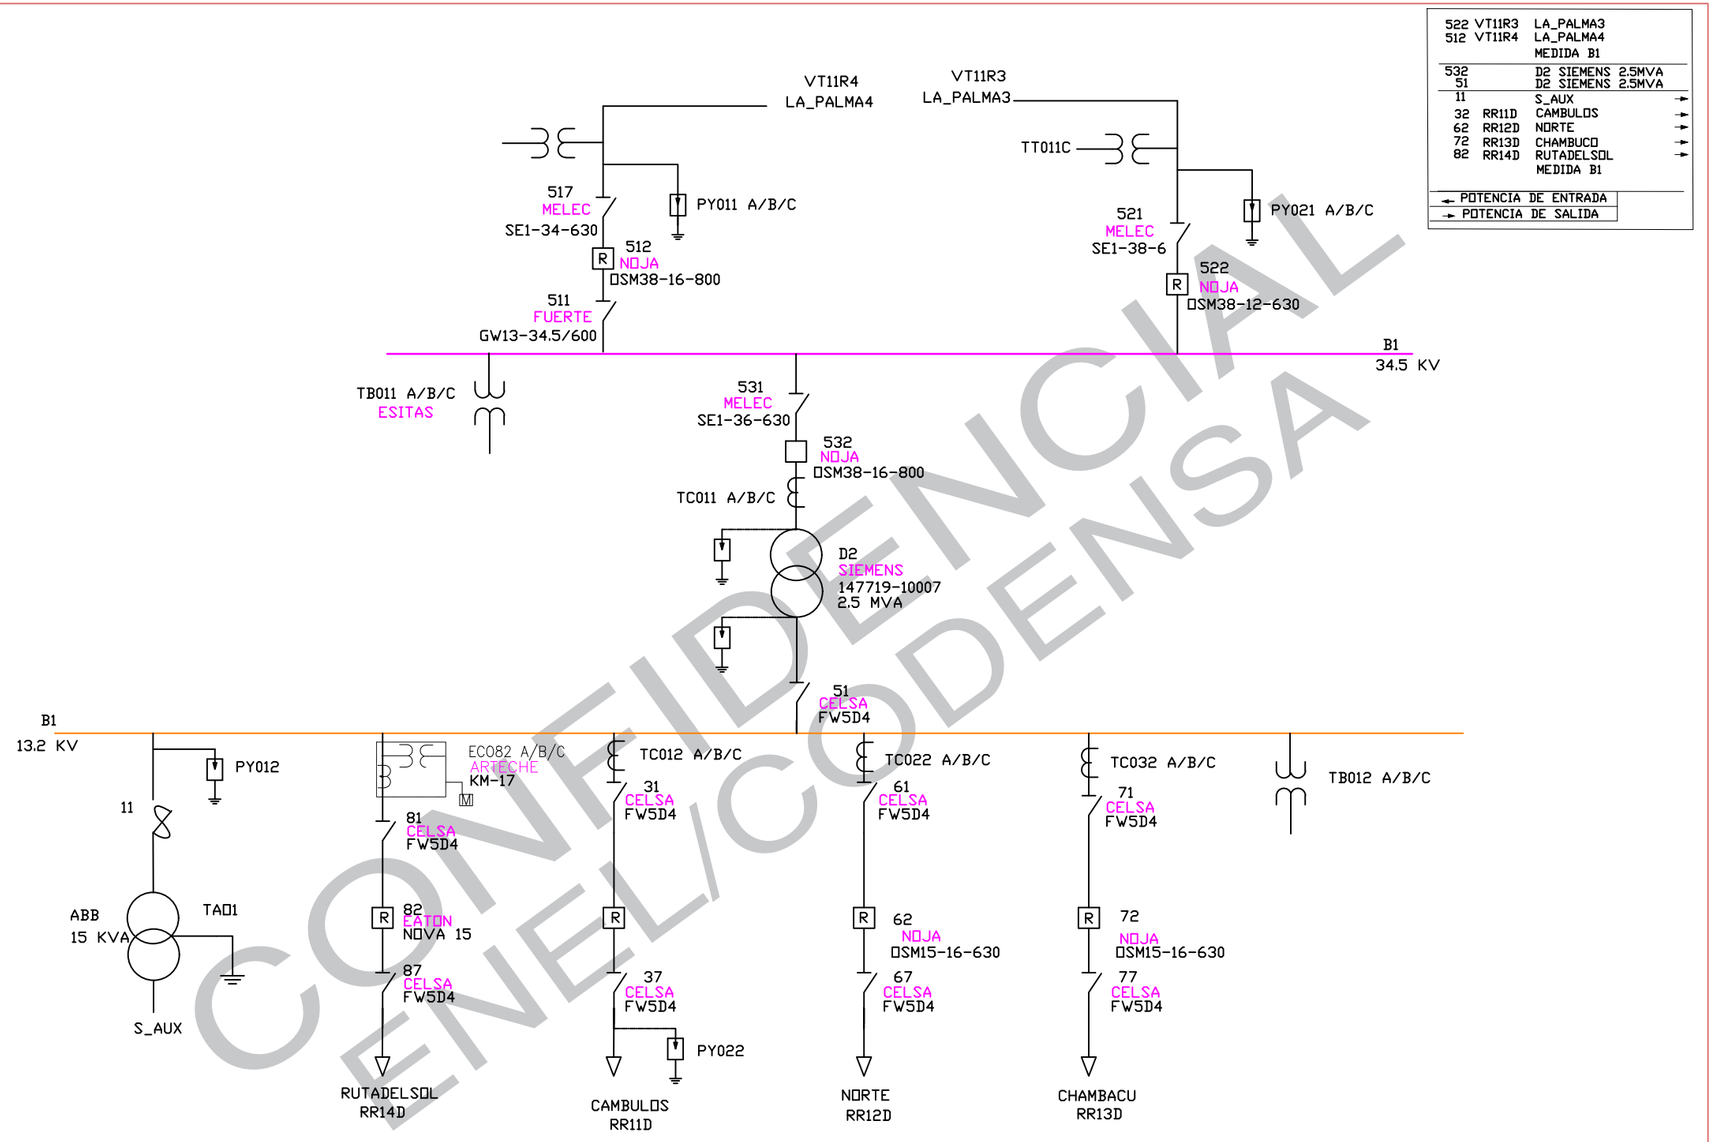

CONFIDENCIAL ENEL/CODENSA

codensa

Unidad Organizativa
Administración Información
Técnica Col.

REVISION No.	14
FECHA:	MARZO/2022
ARCHIVO:	CAPARRAPI.DWG
	\\COLCOD09FS01\FileServer\CONTROL UNIFILARES

DIAGRAMA UNIFILAR
SUBESTACIÒN CAPARRAPI
FRENTE A LOS TANQUES DEL ACUEDUCTO MUNICIPAL
CODIGO: RR

69

HOJA: 1
DE: 1