


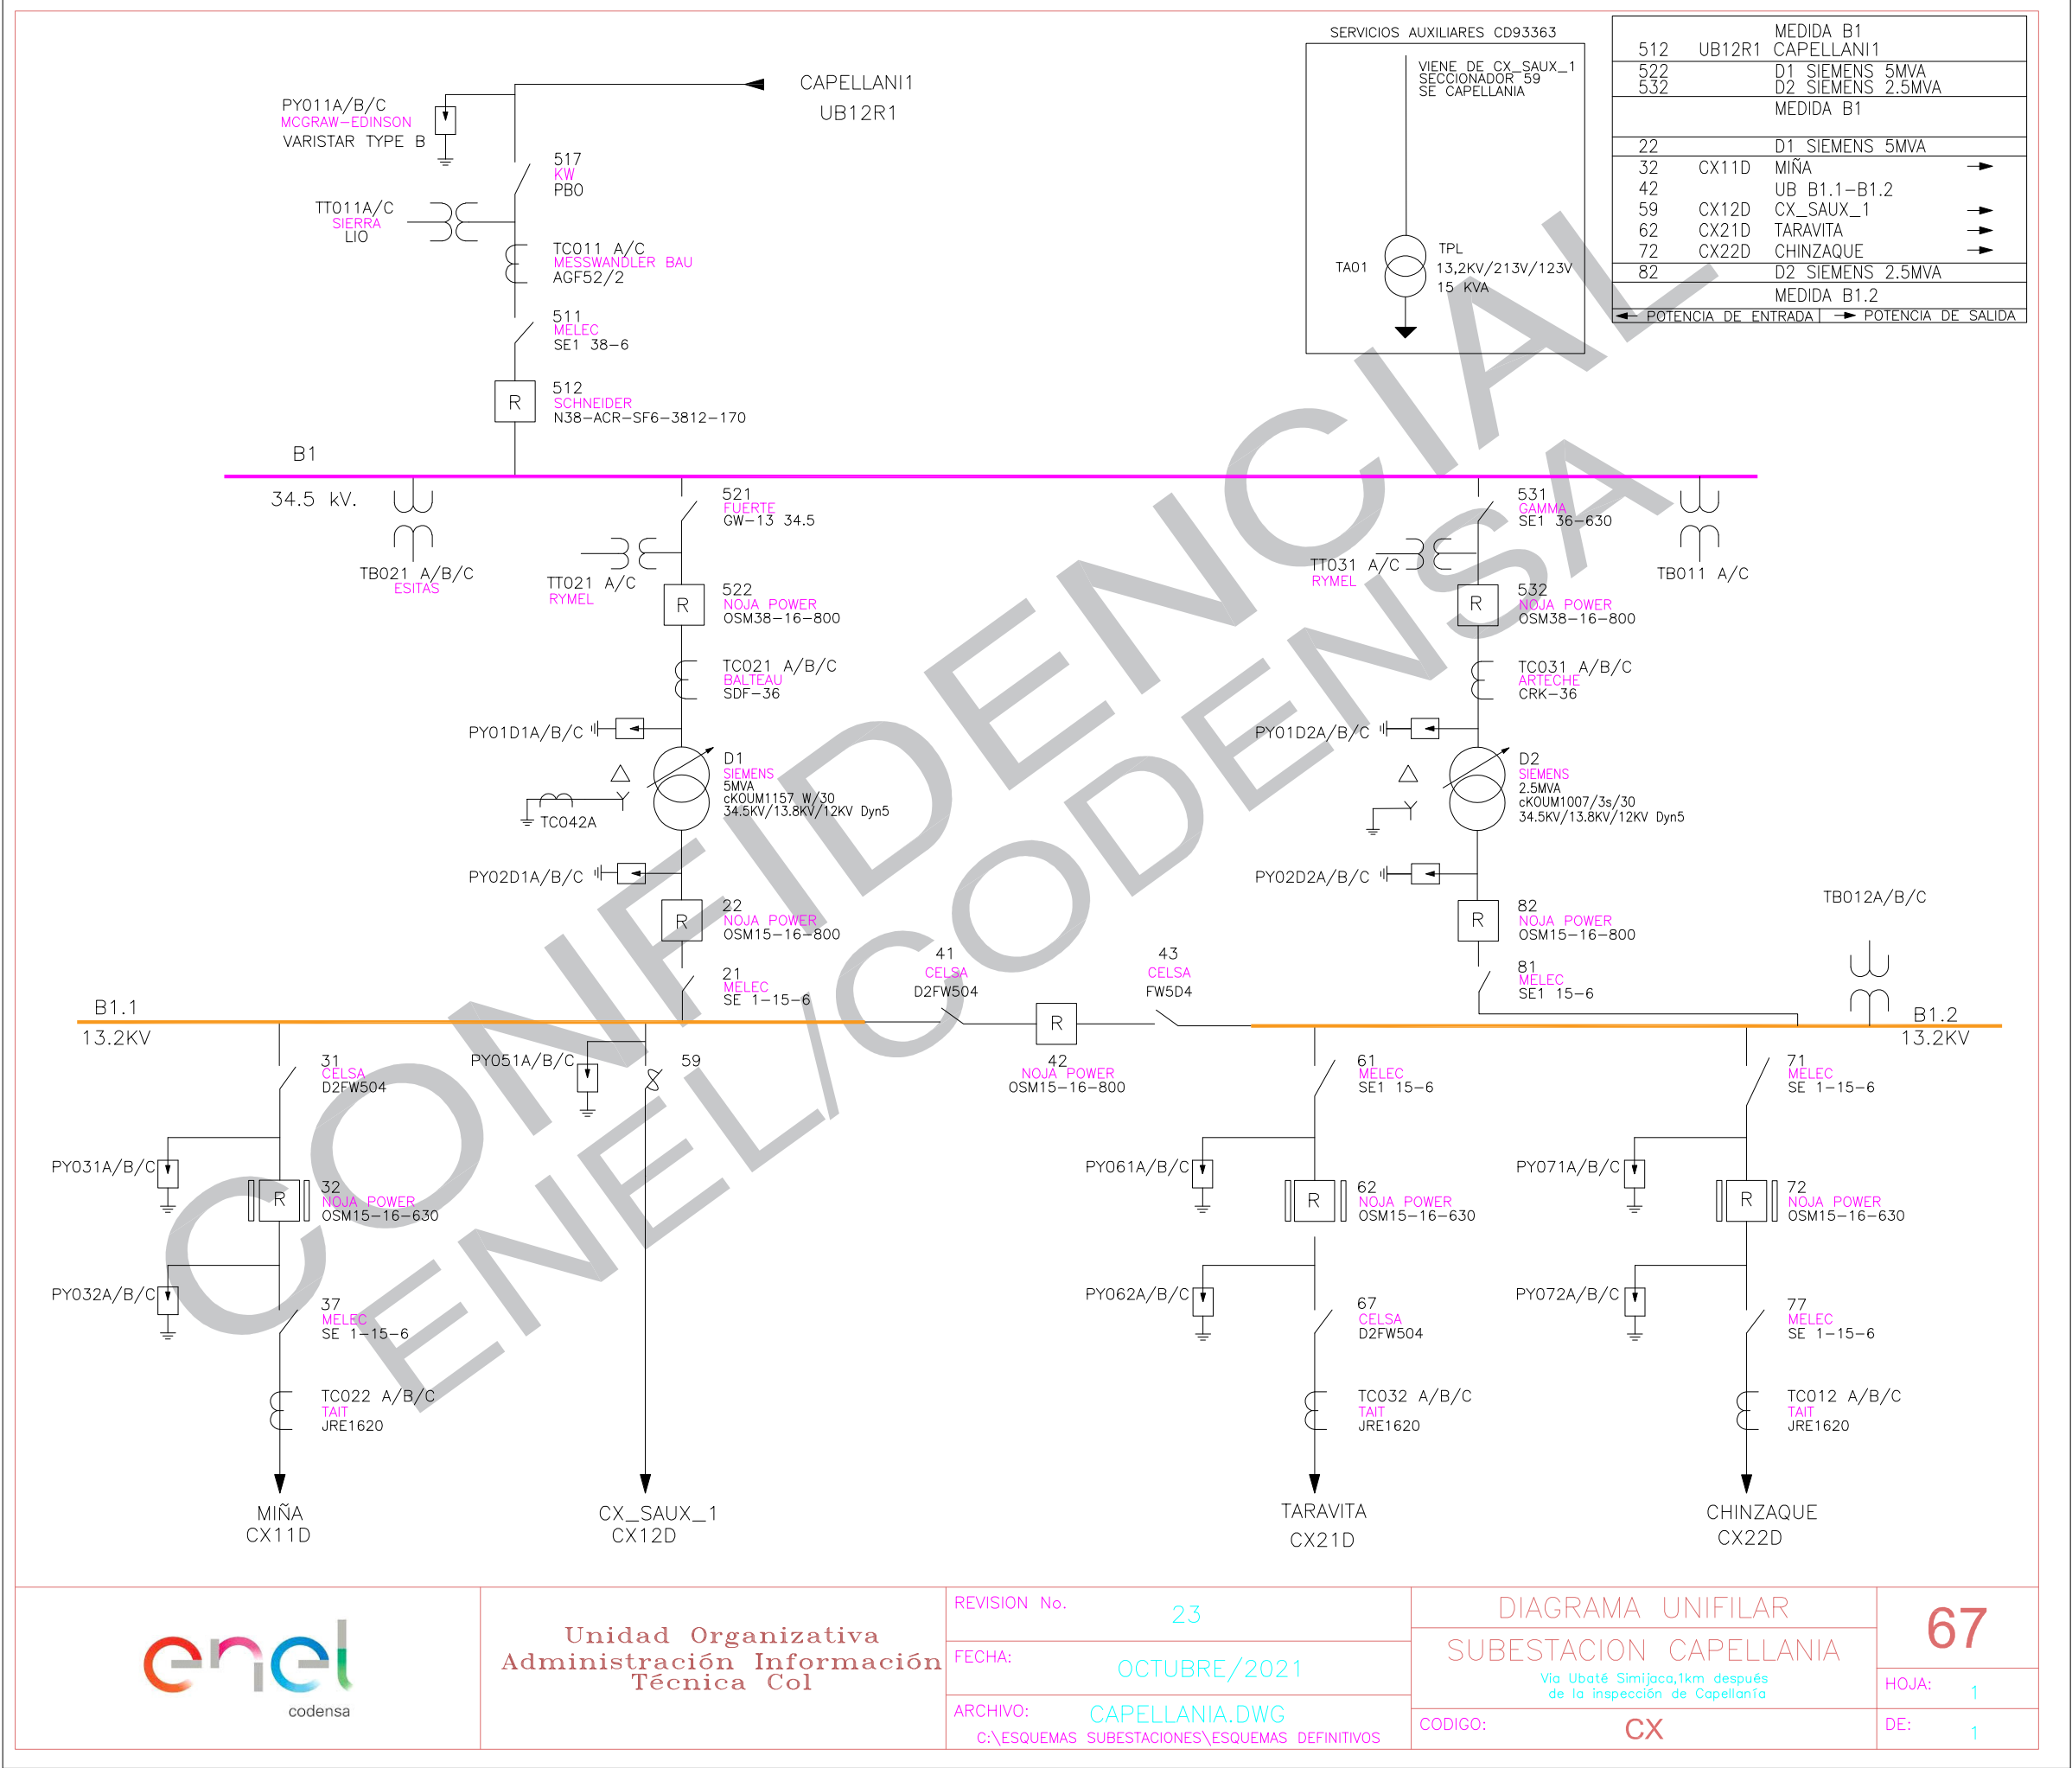

Unidad Organizativa
Administración Información
Técnica Col

REVISION No. 23
FECHA: OCTUBRE/2021
ARCHIVO: CAPELLANIA.DWG
C:\ESQUEMAS SUBESTACIONES\ESQUEMAS DEFINITIVOS

DIAGRAMA UNIFILAR
SUBESTACION CAPELLANIA
Via Ubaté Simijaca, 1km después de la inspección de Capellanía
CODIGO: CX

67

HOJA: 1
DE: 1