



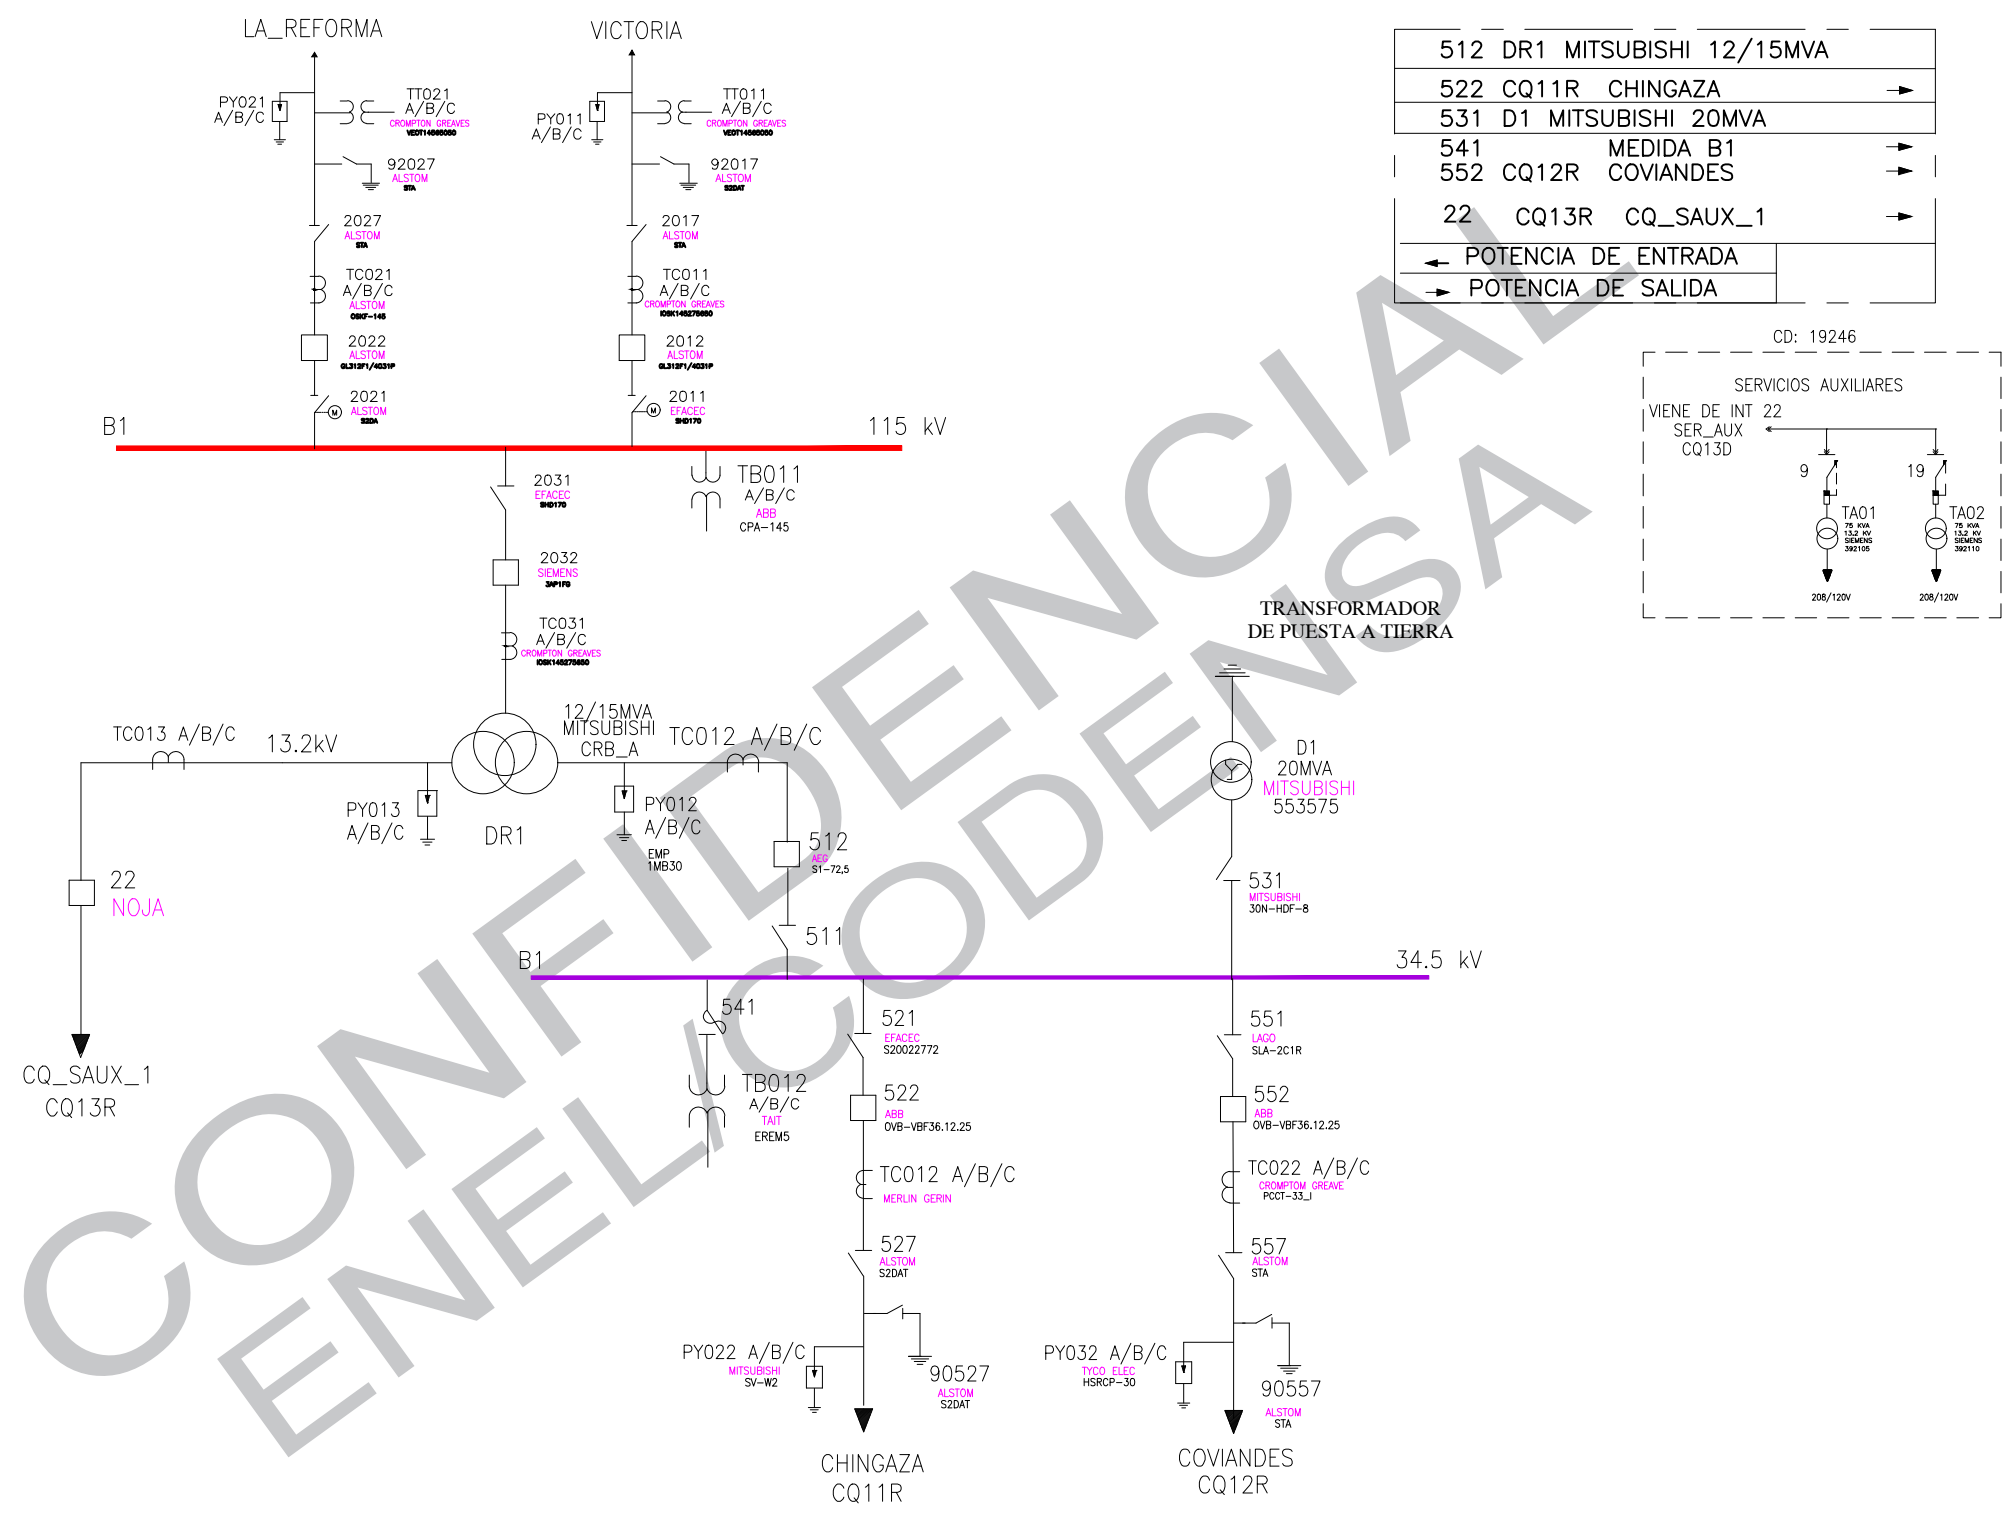

512	DR1	MITSUBISHI	12/15MVA	
522	CQ11R	CHINGAZA		→
531	D1	MITSUBISHI	20MVA	
541		MEDIDA	B1	→
552	CQ12R	COVIANDES		→
22	CQ13R	CQ_SAUX_1		→
← POTENCIA DE ENTRADA				
→ POTENCIA DE SALIDA				

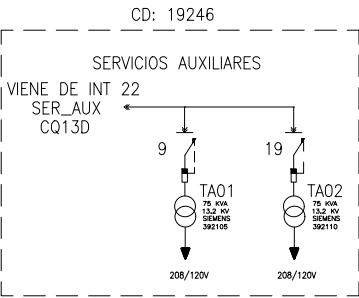

Unidad Organizativa
Administración Informacion
Técnica Col

REVISION No.	20
FECHA:	ENERO/2022
ARCHIVO:	CAQUEZA.DWG Y:\CONTROL UNIFILARES\ABRIL 2021

DIAGRAMA UNIFILAR
SUBESTACION CAQUEZA
V. JIRON DEL RESGUARDO M. DE CAQUEZA
TEL. 984 80269 SIEMENS 6537
CODIGO: CQ

10
HOJA: 1
DE: 1