| | | | |
|---|---|---|---|
| | | MEDIDA B1 | |
| 512 | | D1 JEUMONT 7.5MVA | |
| 522 | | D2 SIEMENS 7.5MVA | |
| | | MEDIDA B1 | |
| 532 | VT22R2 | VILLETA2 | → |
| | VT22R7 | VILLETA7 | → |
| 552 | VT22R1 | VILLETA1 | ← |
| 562 | VT22R5 | VILLETA5 | → |
| | | MEDIDA B1 | |
| 39 | | AY_SAUX_1 | C01 |
| 42 | | D2 SIEMENS 7.5MVA | C02 |
| 52 | AY12D | BAGAZAL | C03 |
| 62 | AY13D | SASAIMA | C04 |
| 72 | AY14D | CIUDADULCE | C05 |
| 82 | | D1 JEUMONT 7.5MVA | C06 |
| 14 | | D1 JEUMONT 7.5MVA | C01 |
| | | MEDIDAP | C02 |
| 34 | | LIBRE_2P | C03 |
| 44 | | LIBRE_1P | C04 |
| 54 | | AY_SAUX_1P | C05 |
| 64 | | SASAIMAP | C06 |
| 74 | | CIUDADULCP | C07 |
| 84 | | BAGAZALP | C08 |
| 94 | AY17D | CUNEP | C09 |
| 104 | | D2 SIEMENS 7.5MVA | C10 |

← POTENCIA DE ENTRADA | → POTENCIA DE SALIDA

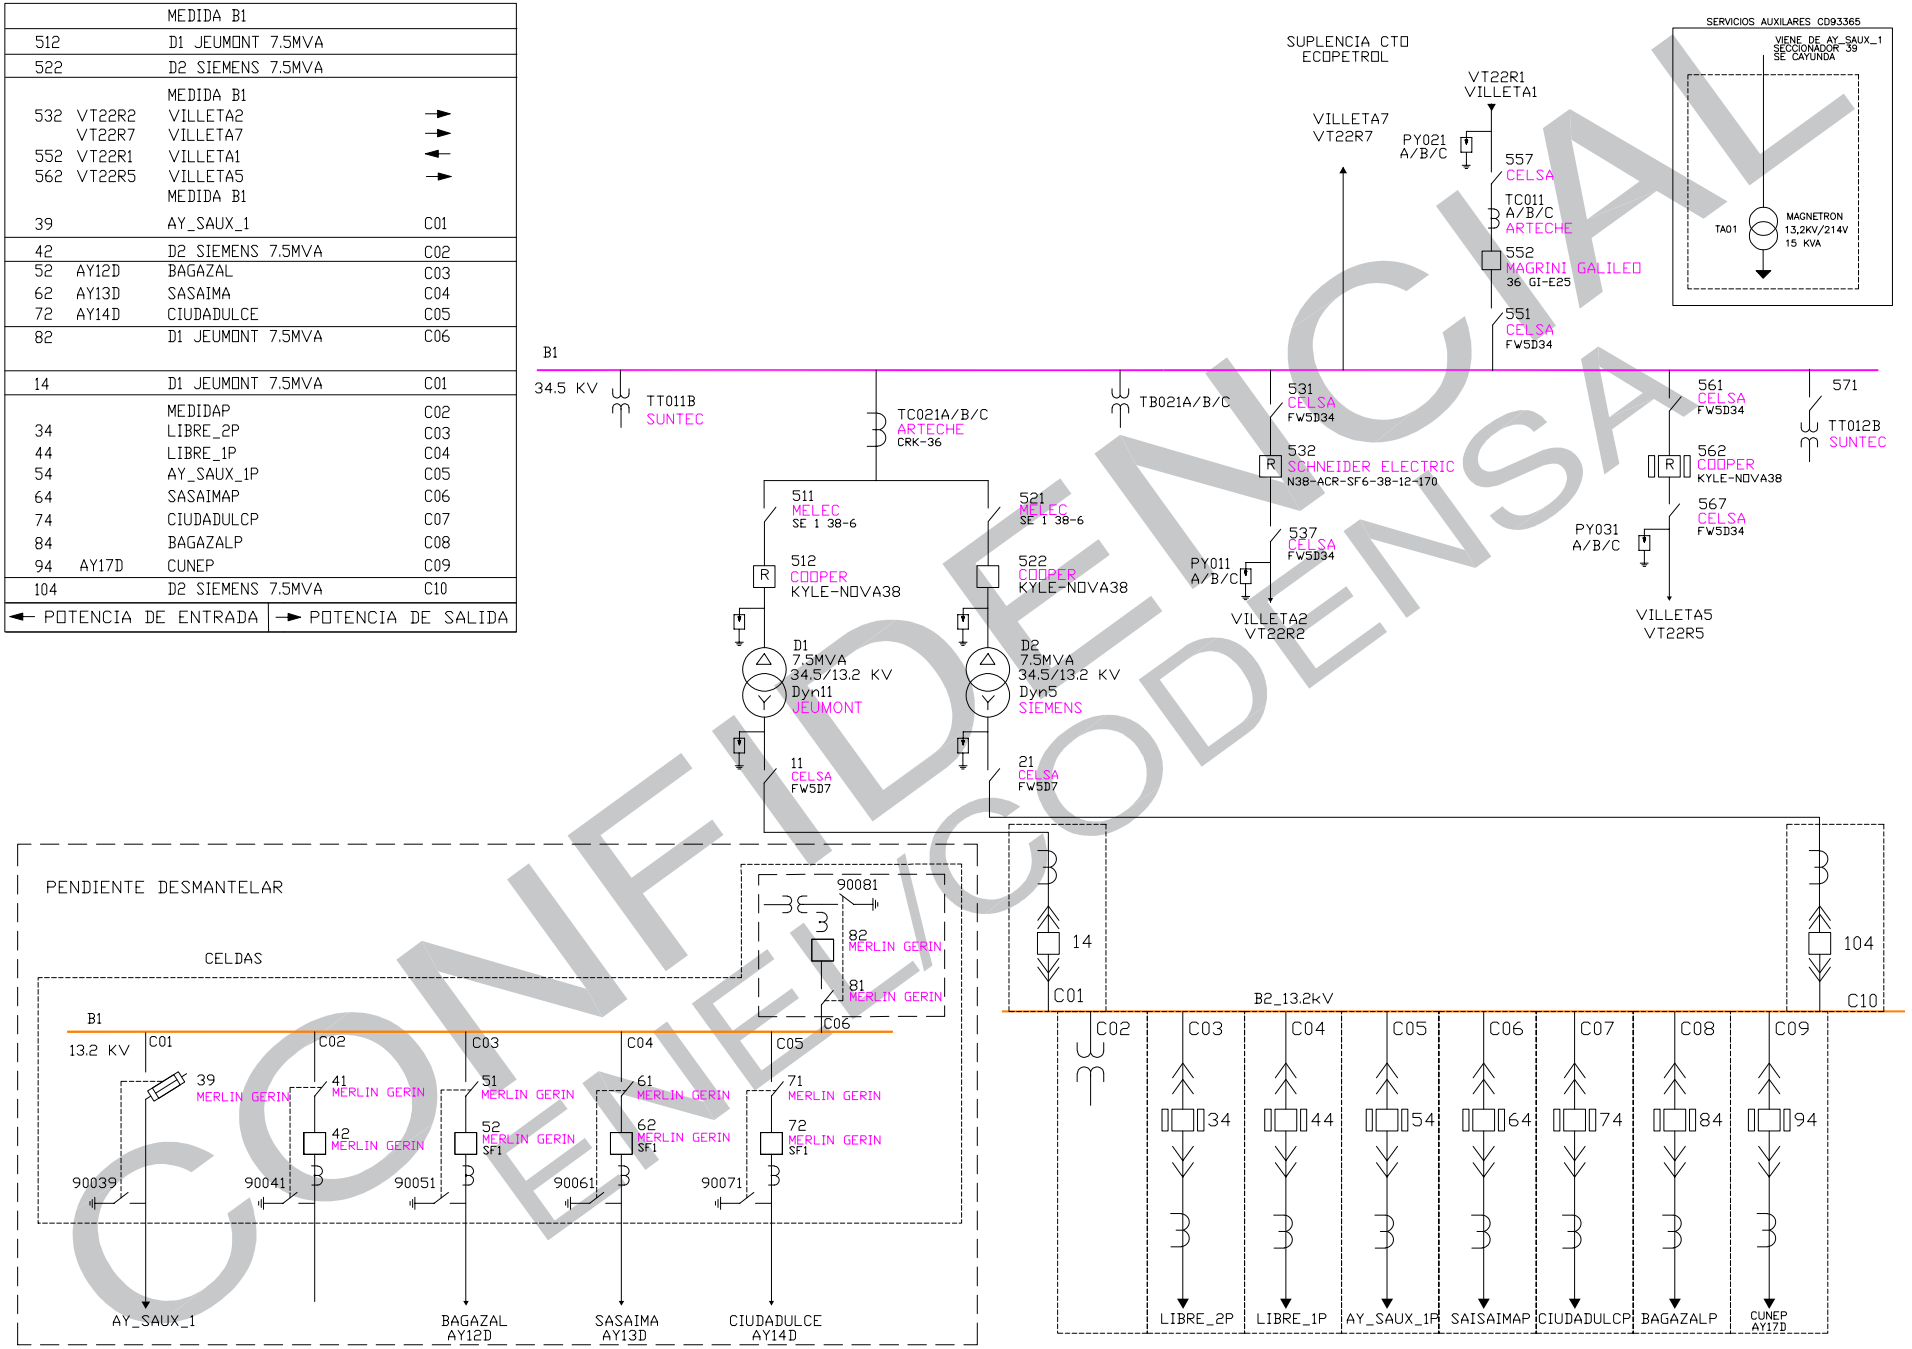


CONFIDENCIAL ENEL/CODENSA

codensa

Unidad Organizativa
Administración Información
Técnica Col

| | |
|---|---|
| REVISION No. | 11 |
| FECHA: | NOVIEMBRE/2022 |
| ARCHIVO: | CAYUNDA.DWG |
| | \\10.185.40.28\FileServer\CONTROL UNIFILARES |

DIAGRAMA UNIFILAR

SUBESTACION CAYUNDA
ANTIGUO VILLETA
MUNICIPIO DE VILLETA

CODIGO: AY

129

HOJA: 1

DE: 1