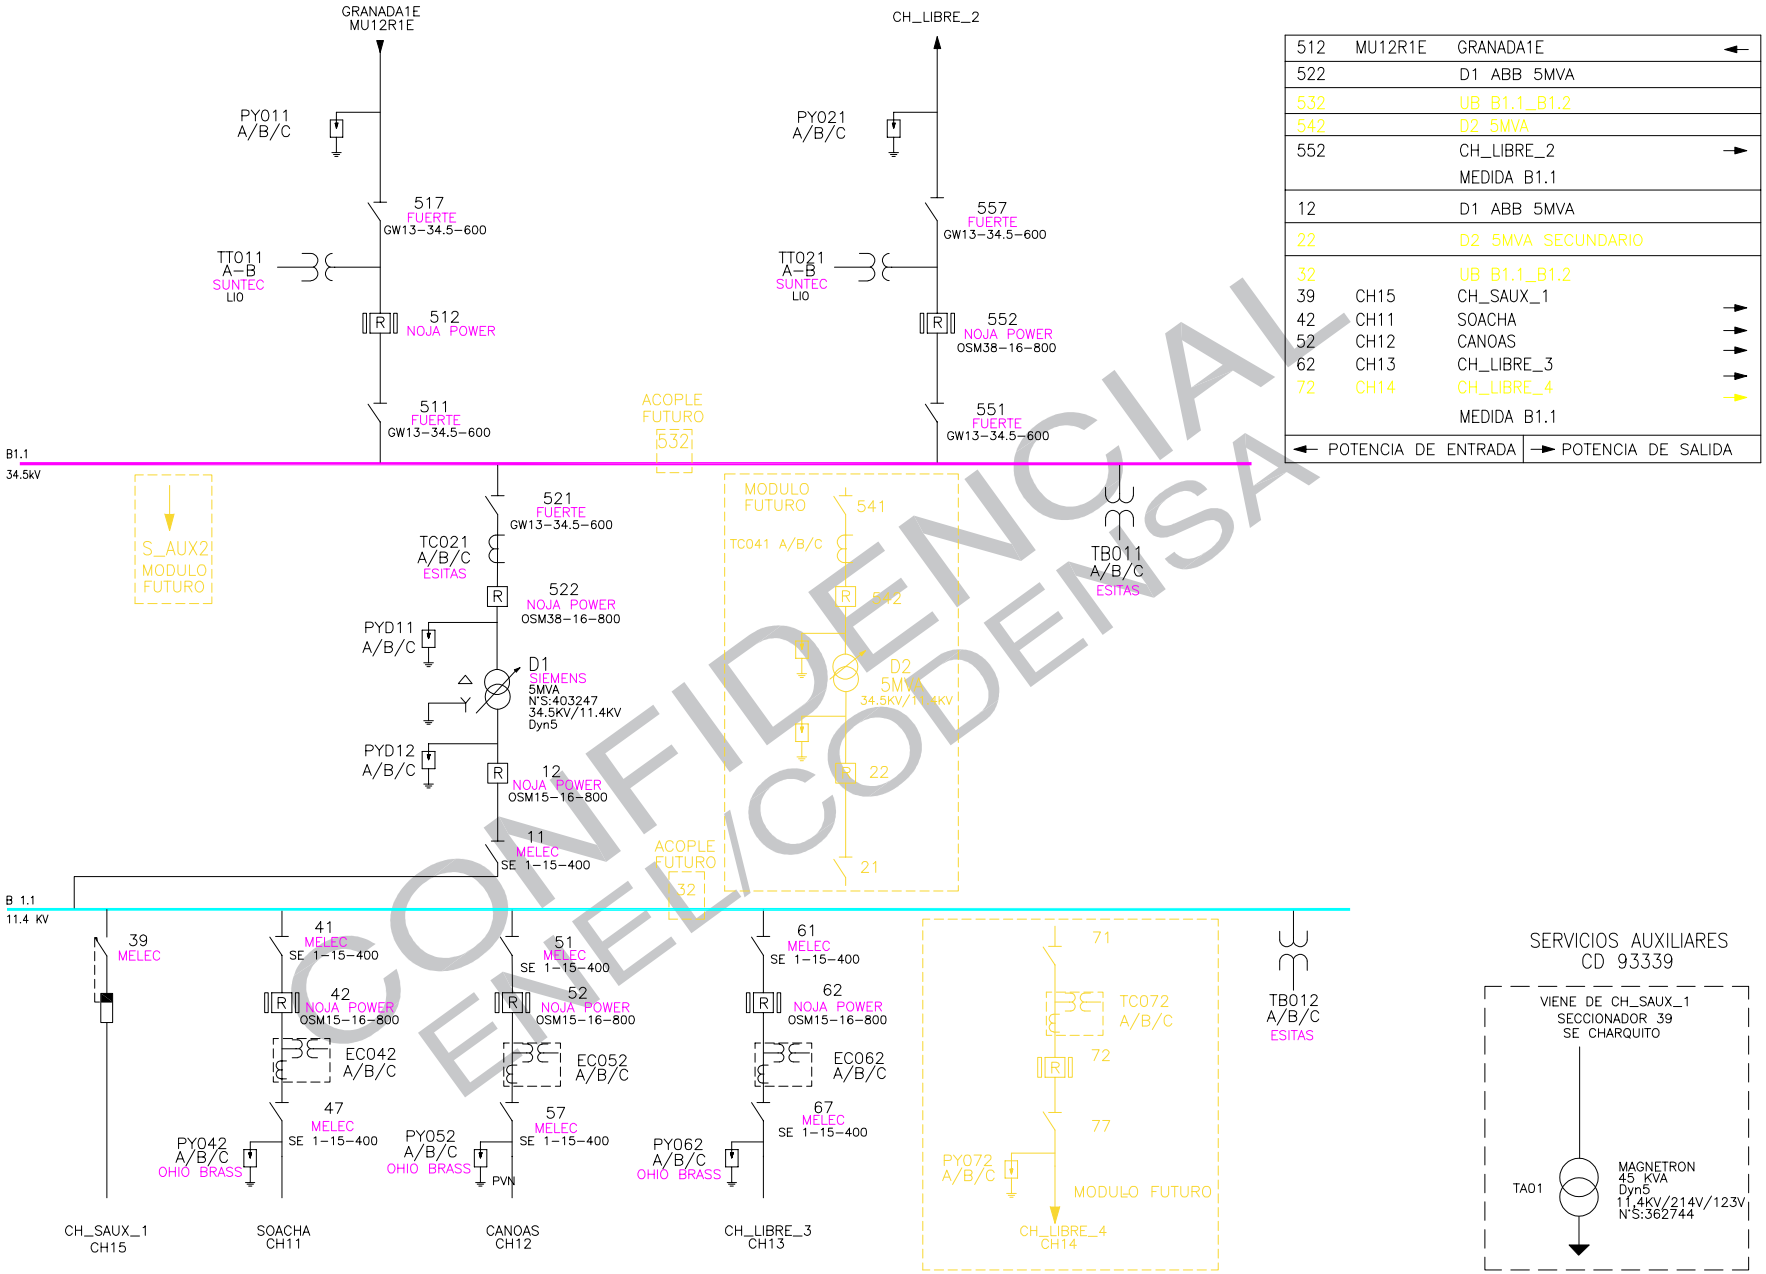

512	MU12R1E	GRANADA1E	←
522		D1 ABB 5MVA	
532		UB B1.1_B1.2	
542		D2 5MVA	
552		CH_LIBRE_2	→
		MEDIDA B1.1	
12		D1 ABB 5MVA	
22		D2 5MVA SECUNDARIO	
32		UB B1.1_B1.2	
39	CH15	CH_SAUX_1	
42	CH11	SOACHA	→
52	CH12	CANOAS	→
62	CH13	CH_LIBRE_3	→
72	CH14	CH_LIBRE_4	→
		MEDIDA B1.1	

← POTENCIA DE ENTRADA | → POTENCIA DE SALIDA

CONFIDENCIAL
ENEL/CODENSA

codensa

Unidad Organizativa
Administración Información
Técnica Col.

REVISION No.	13
FECHA:	AGOSTO/2022
ARCHIVO:	CHARQUITO.DWG
	Y:\FileServer\CONTROL UNIFILARES\UNIFILARES_ENERO_2019

DIAGRAMA UNIFILAR

SUBESTACION CHARQUITO
Z.R. DE SOACHA VEREDA EL CHARQUITO
TEL. 7198011 ABB 123547

CODIGO: CH

12

HOJA: 1

DE: 1