

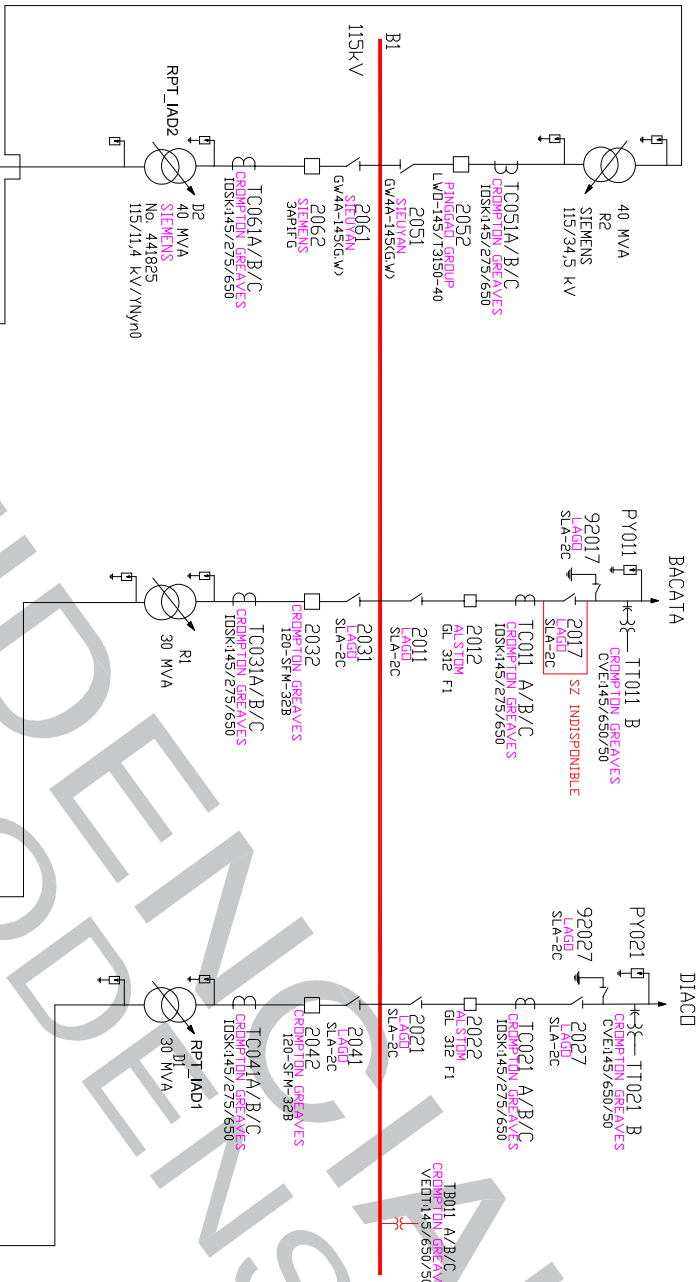
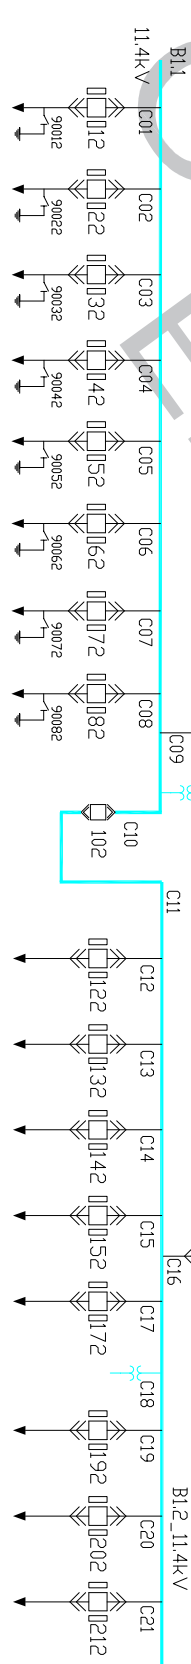


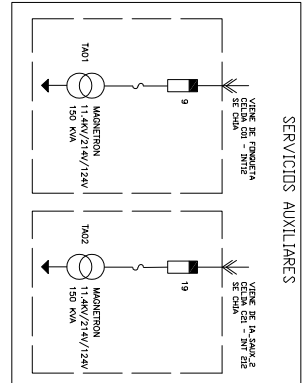

12	IA11	FONQUETA	CO1
22	IA12	CENT COMER	CO2
32	IA13	LA CAJAS	CO3
42	IA14	SANABAS	CO4
52	IA15	STA. LUCIA	CO5
62	IA16	FAJALGRENIA	CO6
72	IA17	FONFAMAR	CO7
82	IA18		CO8
92			
102	IB1	UB B1-B2, 4 MEDIDA, B11	CO9
112	IA21	PELA RENDITE	CO10
122	IA22	PRADILLA	CO11
132	IA23	LIBRE-IA23	CO12
142	IA24		CO13
152	IA25	UB B1-B2, 4 MEDIDA, B12	CO14
162	IA26	LA CARO	CO15
172	IA27	LA CAJAS	CO16
182	IA28	LA CAJAS	CO17
192	IA29	LA CAJAS	CO18
202	IA30	LA CAJAS	CO19
212	IA31	LA CAJAS	CO20
222	IA32	LA CAJAS	CO21

512	IA2R	NOVICIANO	CO2R
522	IA2R	CC CHIA	CO2R
532	IA2R	RE SIEMENS 40 MVA (15/24.5KV)	CO2R
542	IA2R	VITEVCO	CO2R
552	IA2R	MEIDIA B11	CO2R
562	IA2R	UB B1-B12	CO2R
572	IA2R	PELA RENDITE	CO2R
582	IA2R	LIBRE-IA2R	CO2R
592	IA2R	LIBRE-IA2R	CO2R
602	IA2R	RE SIEMENS 30 MVA	CO2R
612	IA2R		CO2R
622	IA2R	LIBRE-IA2R	CO2R
632	IA2R	LIBRE-IA2R	CO2R

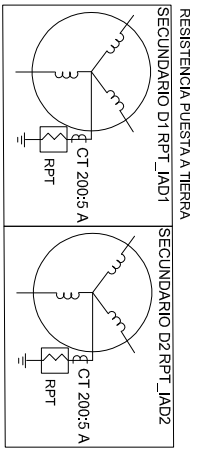

Unidad Organizativa
Administración Informática
Técnica Col.

REVISION NO. 19
FECHA: NOVIEMBRE/2022
ARCHIVO: CHIA.DWG
C:\ESQUEMAS SUBESTACIONES\ESQUEMAS DEFINITIVOS

DIAGRAMA UNIFILAR
SUBESTACION CHIA
V. Fonqueta / M. Chia SIEMENS 6645
CODIGO: IA

68
HOLAJE: 1
DE: 1