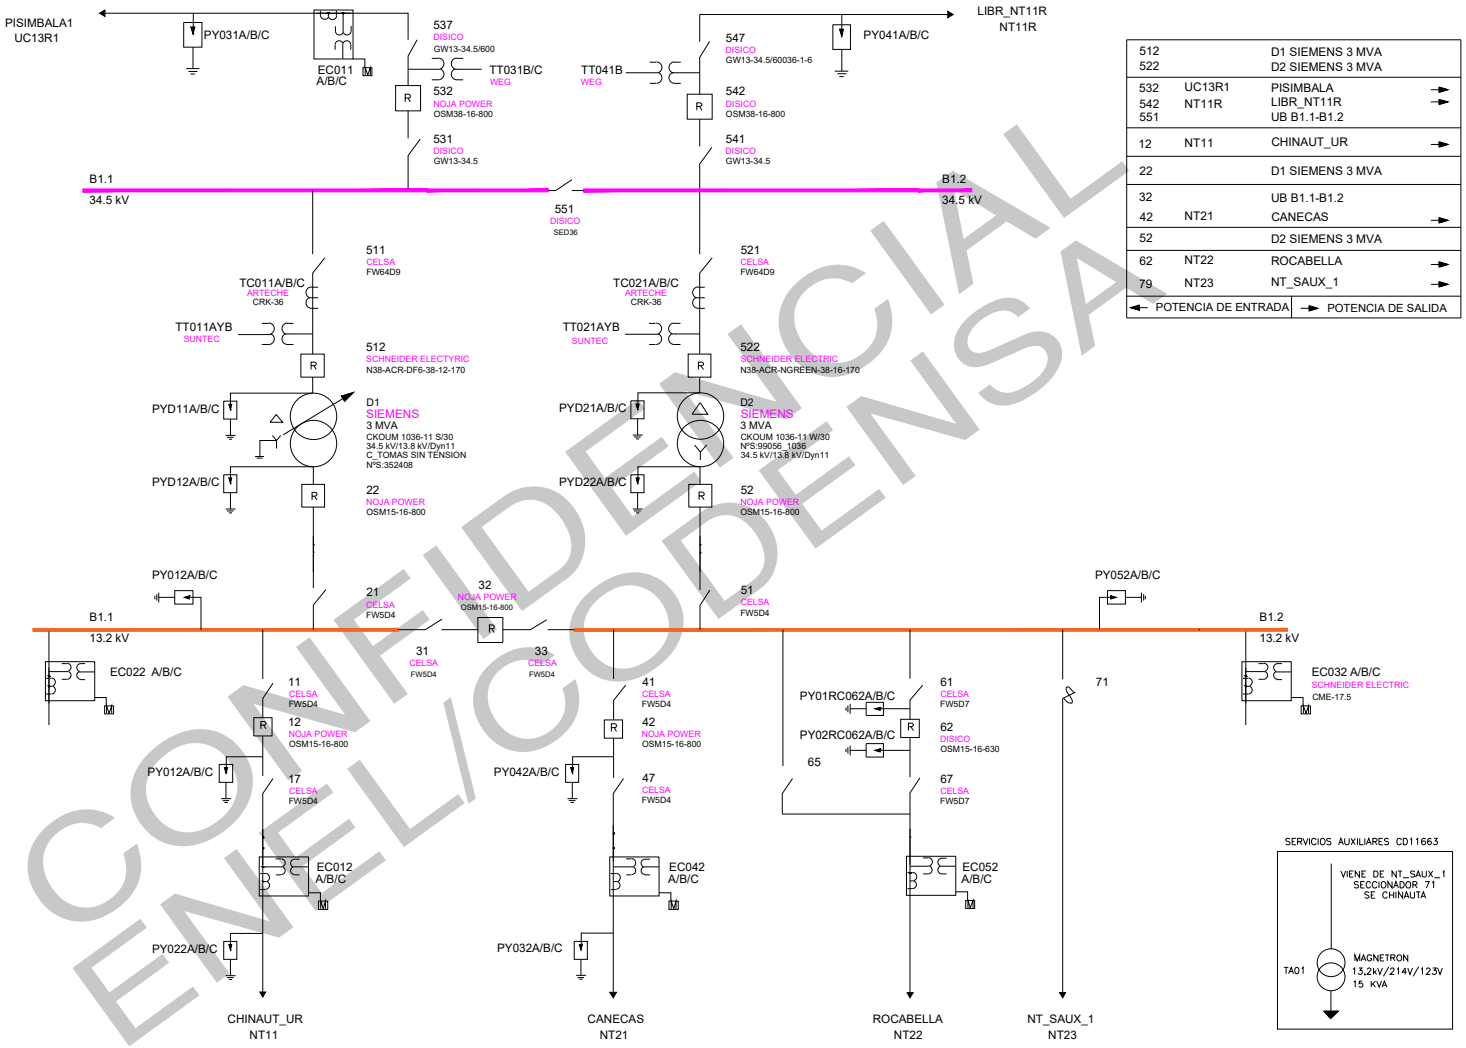


512		D1 SIEMENS 3 MVA
522		D2 SIEMENS 3 MVA
532	UC13R1	PISIMBALA →
542	NT11R	LIBR_NT11R →
551		UB B1.1-B1.2
12	NT11	CHINAUT_UR →
22		D1 SIEMENS 3 MVA
32		UB B1.1-B1.2
42	NT21	CANECAS →
52		D2 SIEMENS 3 MVA
62	NT22	ROCABELLA →
79	NT23	NT_SAUX_1 →

← POTENCIA DE ENTRADA | → POTENCIA DE SALIDA

CONFIDENCIAL
ENEL/CODENSA

enel codensa	Unidad Organizativa Administracion Informacion Tecnica Col	REVISION No. 6	DIAGRAMA UNIFILAR
		FECHA: NOVIEMBRE / 2022	SUBESTACION CHINAUTA
		ARCHIVO: CHINAUTA.DWG	MUNICIPIO DE FUSAGASUGA
		Y:\FileServer\CONTROL UNIFILARES\UNIFILARES_MARZO_2019	CODIGO: NT

602

HOJA: 1

DE: 1