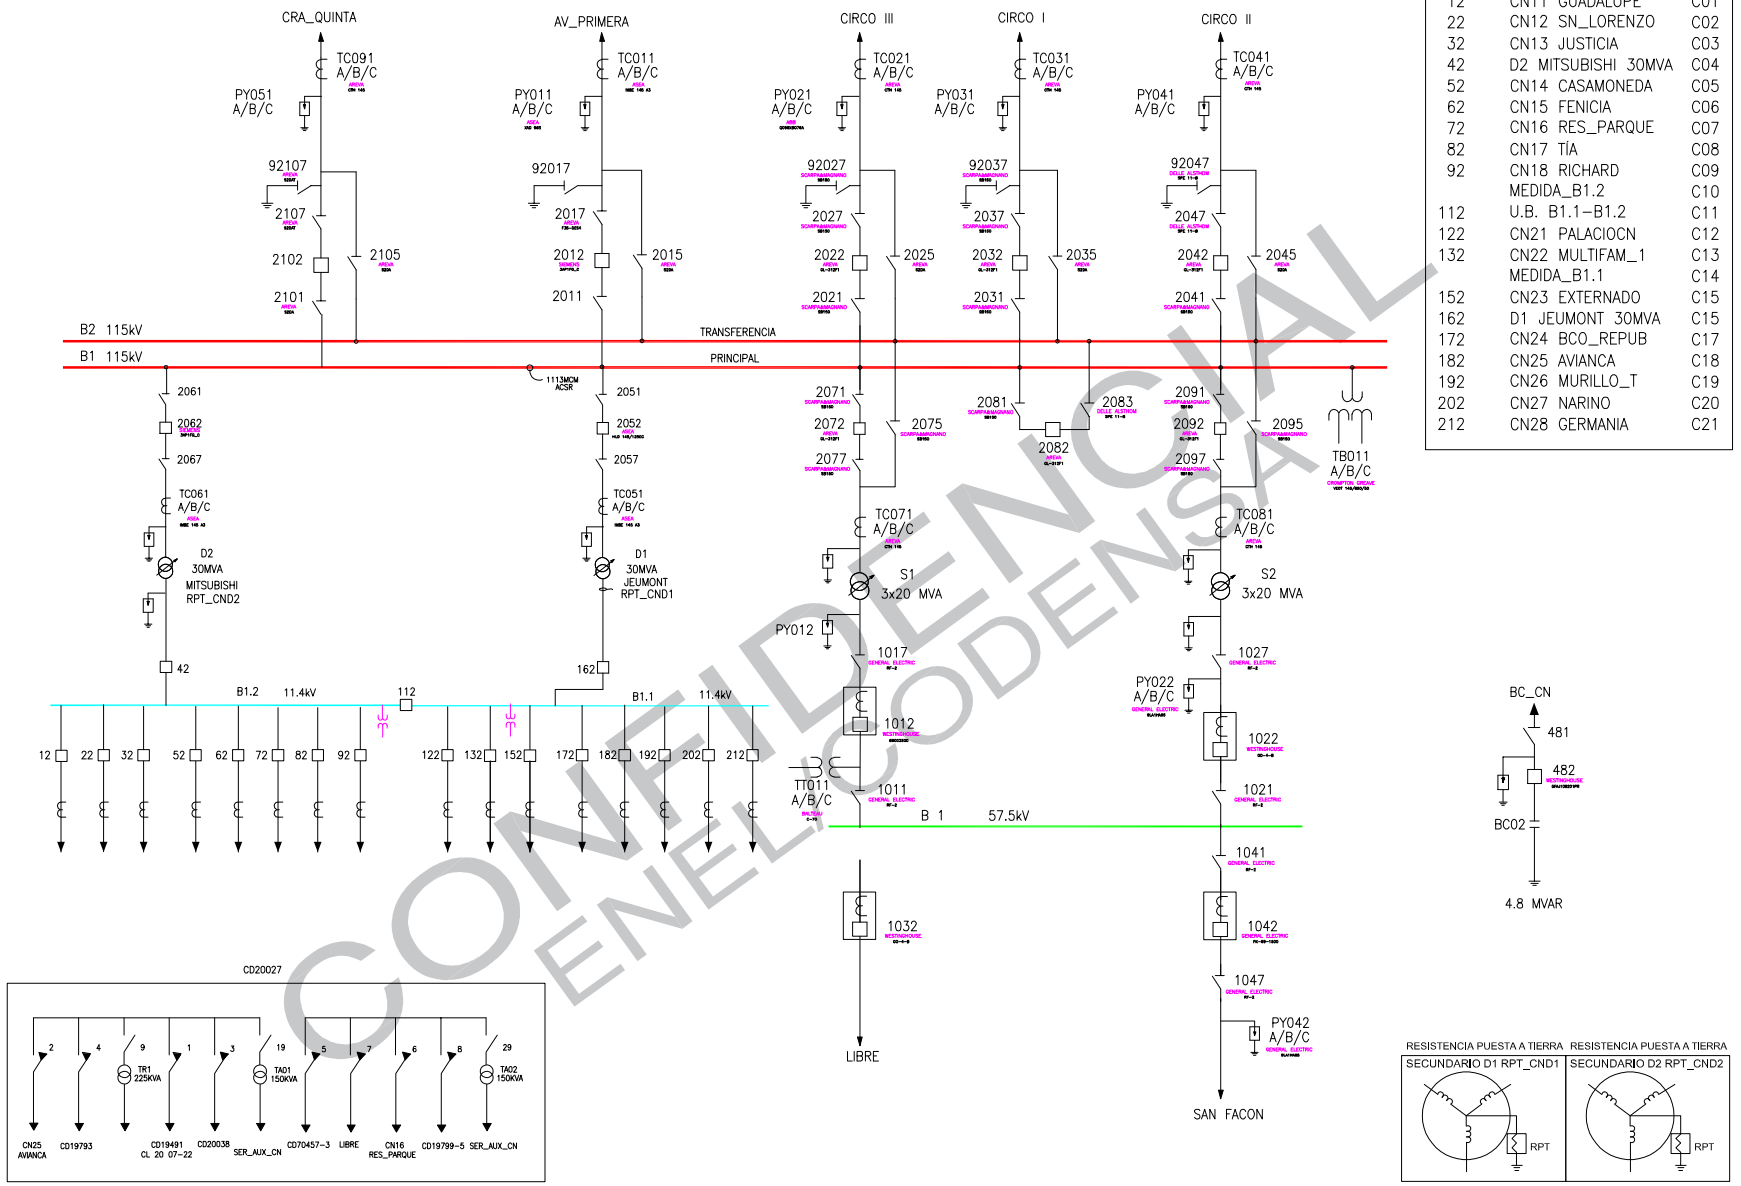


12	CN11 GUADALUPE	C01
22	CN12 SN_LORENZO	C02
32	CN13 JUSTICIA	C03
42	D2 MITSUBISHI 30MVA	C04
52	CN14 CASAMONEDA	C05
62	CN15 FENICIA	C06
72	CN16 RES_PARQUE	C07
82	CN17 TÍA	C08
92	CN18 RICHARD	C09
	MEDIDA_B1.2	C10
112	U.B. B1.1–B1.2	C11
122	CN21 PALACIOCN	C12
132	CN22 MULTIFAM_1	C13
	MEDIDA_B1.1	C14
152	CN23 EXTERNADO	C15
162	D1 JEUMONT 30MVA	C15
172	CN24 BCO_REPUB	C17
182	CN25 AVIANCA	C18
192	CN26 MURILLO_T	C19
202	CN27 NARINO	C20
212	CN28 GERMANIA	C21

CONFIDENCIAL
ENEL CODENSA

UNIDAD ORGANIZATIVA
ADMINISTRACION INFORMACION
TECNICA COL.

REVISION No. 23
FECHA: DICIEMBRE/2022
ARCHIVO: CONCORDIA.DWG
Y:\FileServer\CONTROL UNIFILARES\UNIFILARES_MARZO_2019

DIAGRAMA UNIFILAR
SUBESTACION CONCORDIA
CARRERA 1 No.13–48
TEL. 2438069/2437953 SIEMENS 6532
CODIGO: CN

15
HOJA: 1
DE: 1