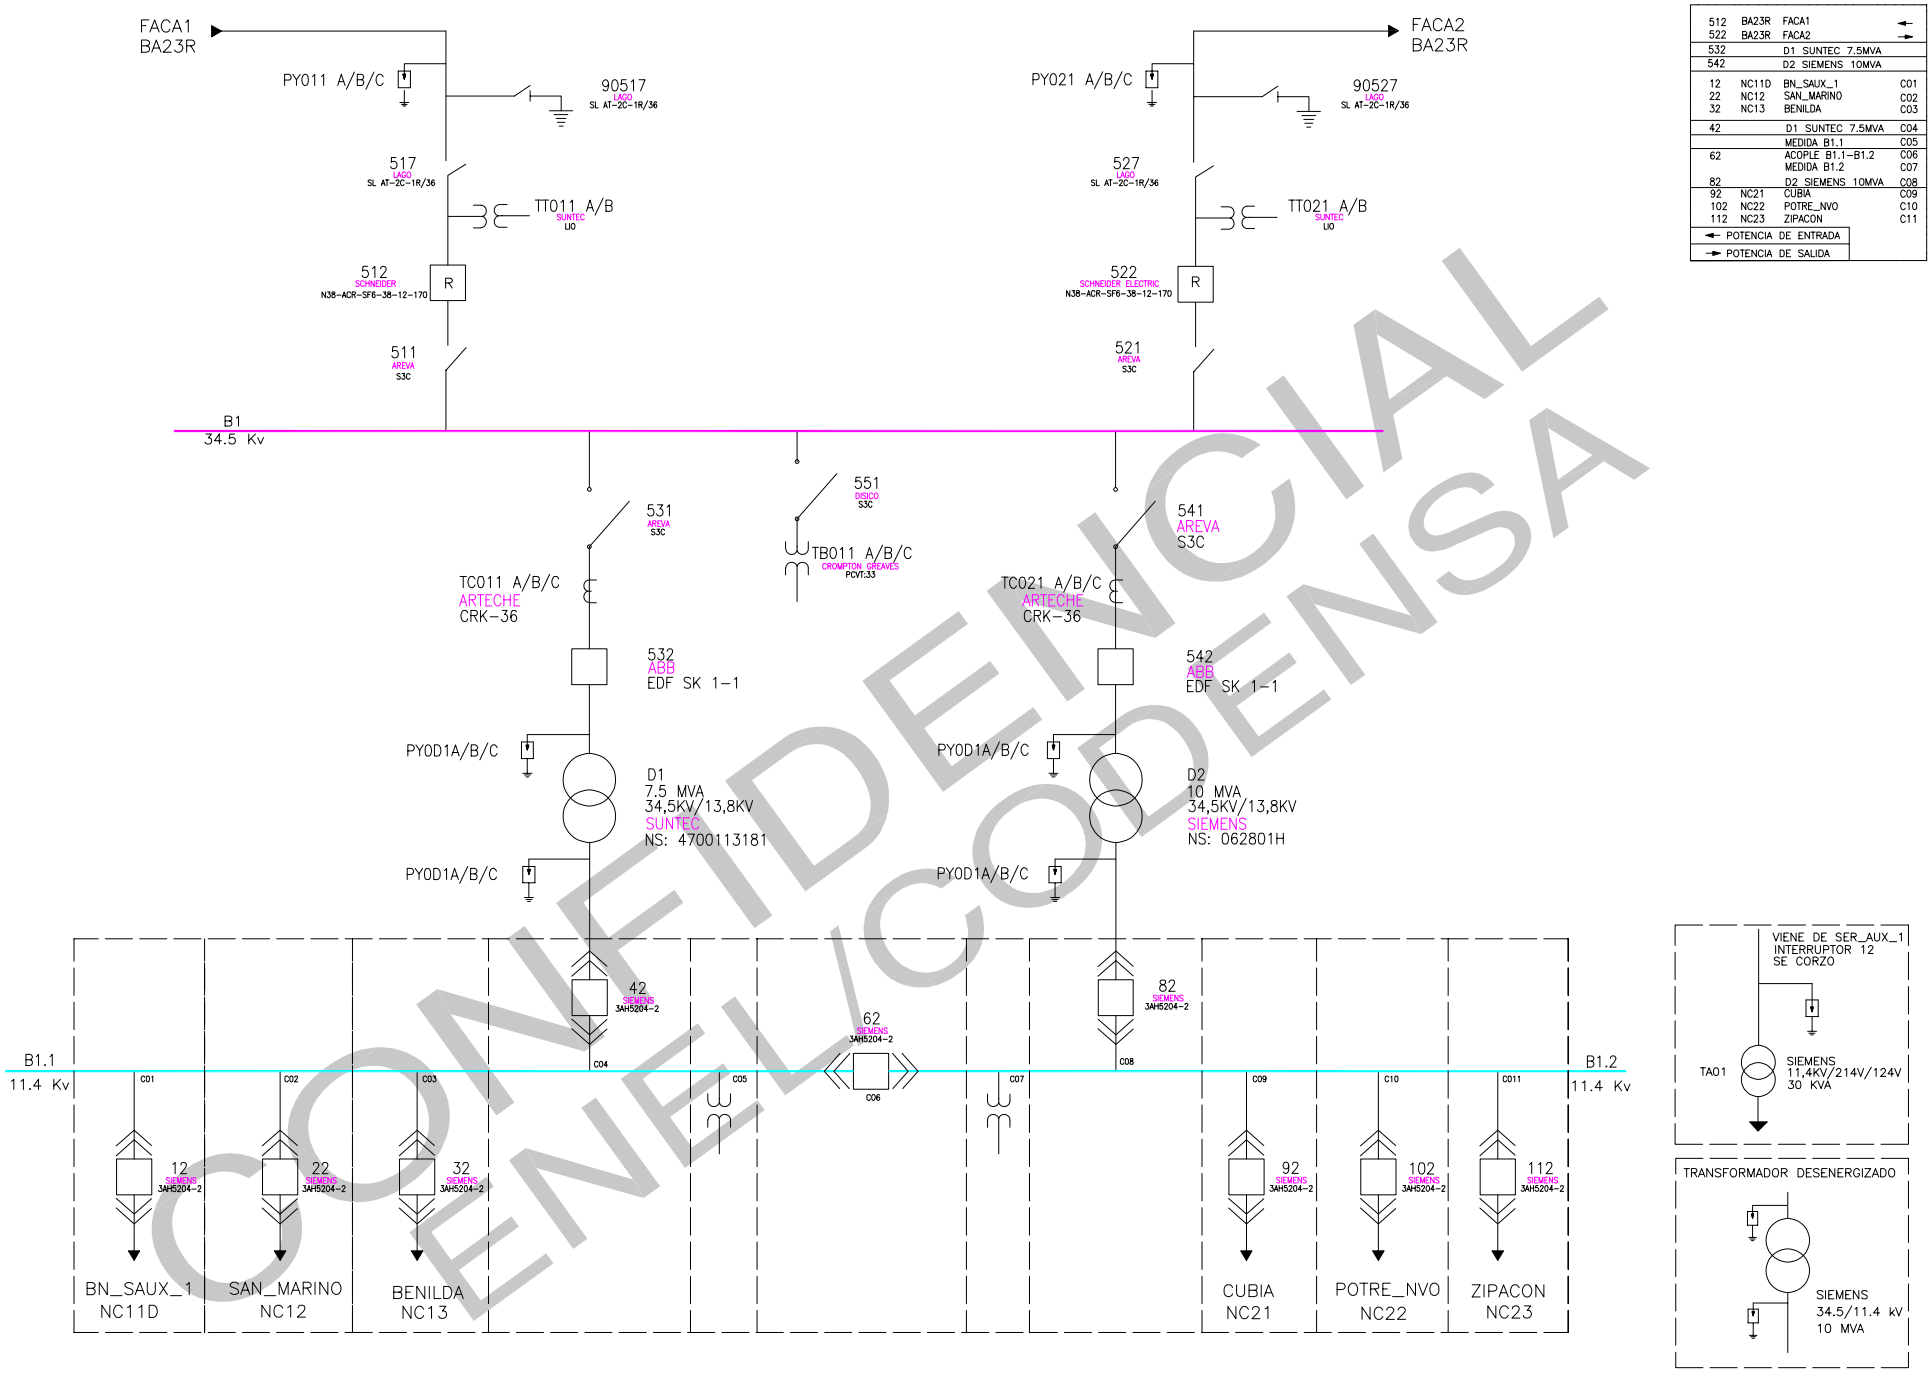

CONFIDENCIAL
ENEL/CODENSA

enel codensa	Unidad Organizativa Administración Información Técnica Col.	REVISION No. 19	DIAGRAMA UNIFILAR
		FECHA: MAYO/2022	SUBESTACION NUEVO CORZO
		ARCHIVO: CORZO_NUEVA.DWG \\COLCOD09FS01\FileServer\CONTROL UNIFILARES	Sobre la vía principal que conduce de Madrid a faca 1500m antes de la entrada al municipio de Bojaca
			CODIGO: NC
			70
			HOJA: 1
			DE: 1