


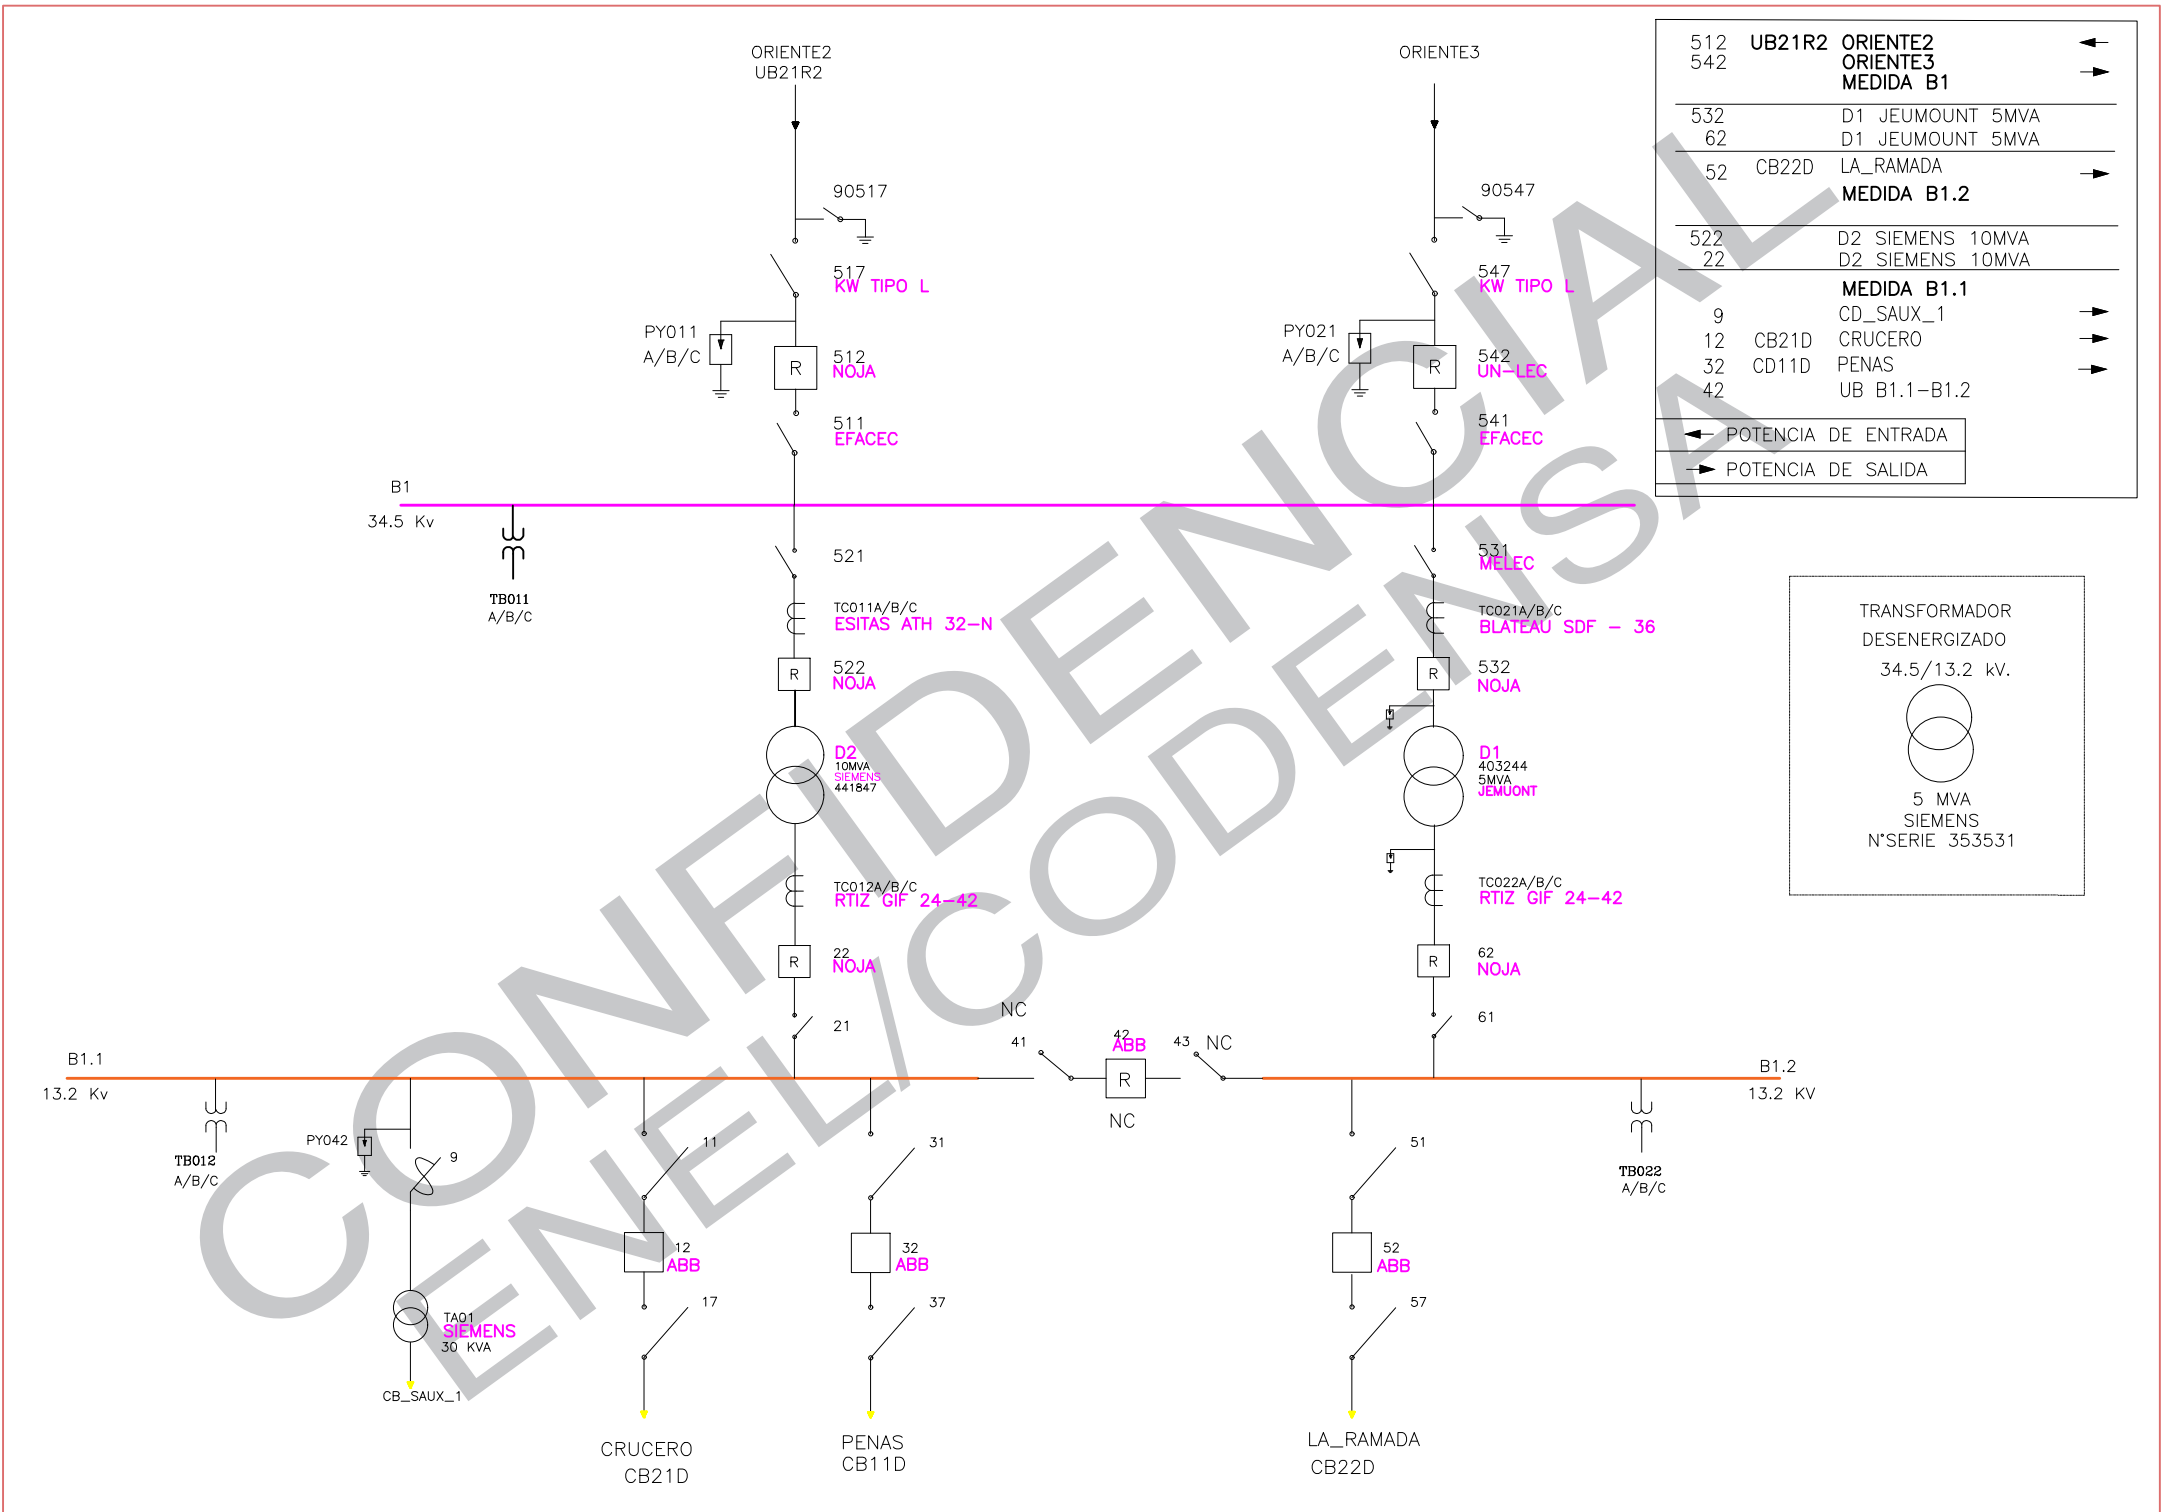

|                       |              |               |   |
|-----------------------|--------------|---------------|---|
| 512                   | UB21R2       | ORIENTE2      | ← |
| 542                   |              | ORIENTE3      | → |
| 532                   | D1           | JEUMOUNT 5MVA |   |
| 62                    | D1           | JEUMOUNT 5MVA |   |
| 52                    | CB22D        | LA_RAMADA     | → |
| MEDIDA B1.2           |              |               |   |
| 522                   | D2           | SIEMENS 10MVA |   |
| 22                    | D2           | SIEMENS 10MVA |   |
| MEDIDA B1.1           |              |               |   |
| 9                     | CD_SAUX_1    |               | → |
| 12                    | CB21D        | CRUCERO       | → |
| 32                    | CD11D        | PENAS         | → |
| 42                    | UB B1.1-B1.2 |               |   |
| ← POTENCIA DE ENTRADA |              |               |   |
| → POTENCIA DE SALIDA  |              |               |   |



Unidad Organizativa  
Administración Informática  
Técnica Col.

|                                                        |              |
|--------------------------------------------------------|--------------|
| REVISION No.                                           | 17           |
| FECHA:                                                 | MARZO/2022   |
| ARCHIVO:                                               | CUCUNUBA.DWG |
| Y:\FileServer\CONTROL UNIFILARES\UNIFILARES_MARZO_2019 |              |

|                                          |
|------------------------------------------|
| DIAGRAMA UNIFILAR                        |
| SUBESTACION CUCUNUBA                     |
| Entrada del municipio,via Ubate Cucunuba |
| CODIGO: CB                               |

|         |
|---------|
| 72      |
| HOJA: 1 |
| DE: 1   |