

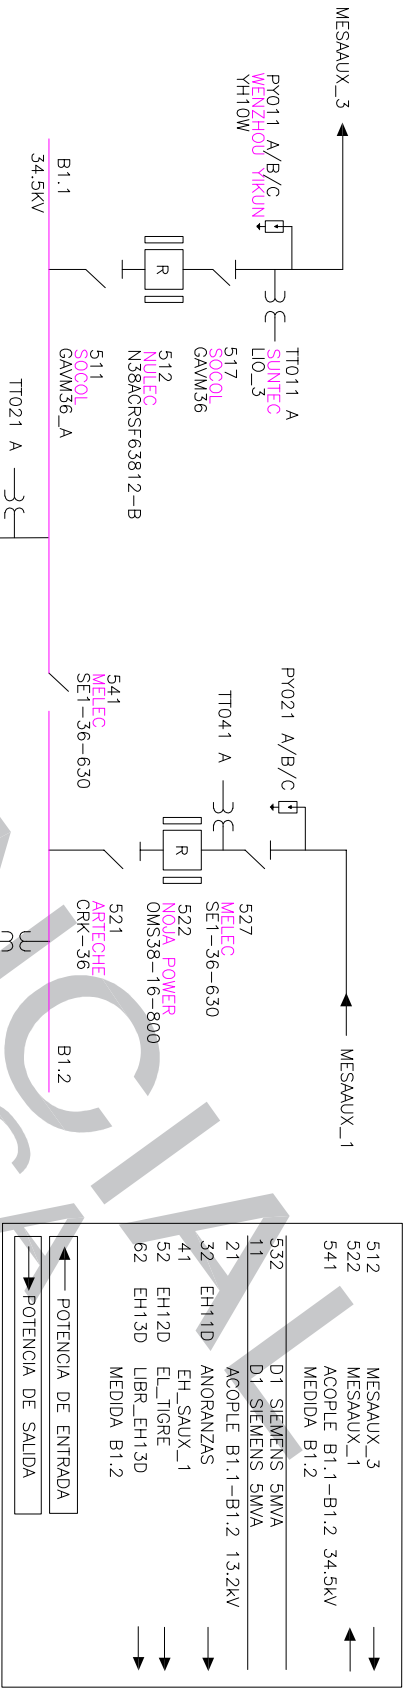


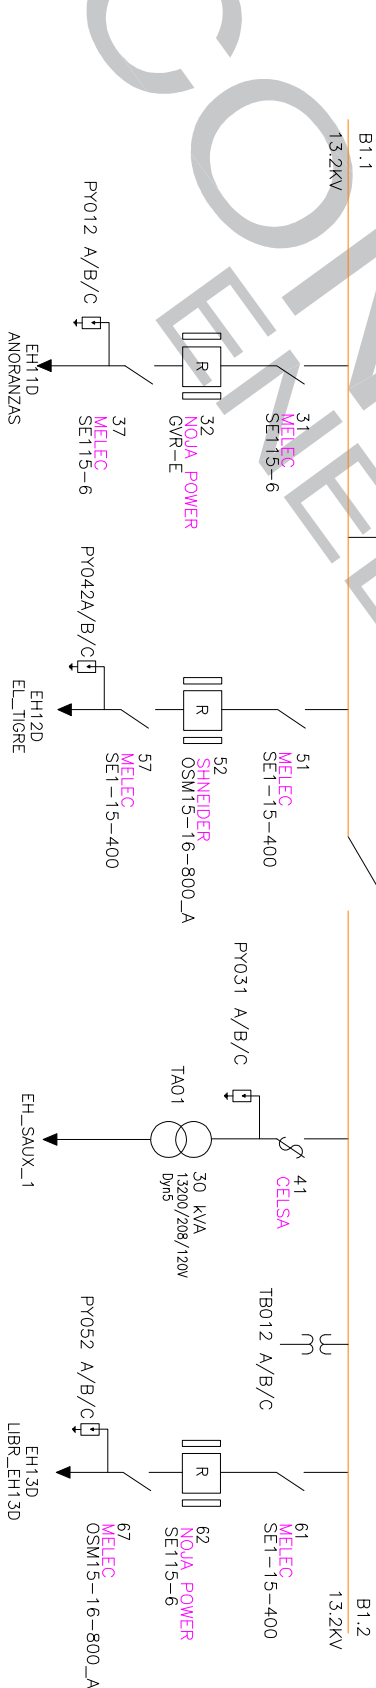

512	MESAUX_3	→
522	MESAUX_1	→
541	ACOPLE B1.1 - B1.2 34.5kV	→
	MEDIDA B1.2	→
532	D1 SIEMENS 5MVA	→
11	ACOPLE B1.1 - B1.2 13.2kV	→
32	EH11D	→
41	EH_SAUX_1	→
52	EH12D	→
62	LIBR_EH13D	→
	MEDIDA B1.2	→

SER. AUX CD93376

VIENE DE
BARRA 1.2 - 13.2[kV]

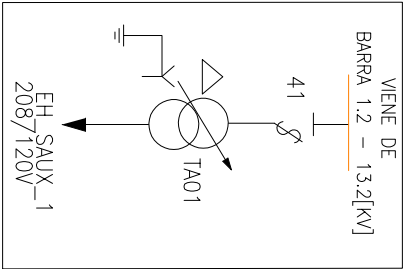

REVISION No. 11

DIAGRAMA UNIFILAR

126

Unidad Organizativa
Administración Informática
Técnica Col.

FECHA: NOVIEMBRE/2022

SUBESTACION EL HATO
M/CIPLO DE LA MESA VEREDA EL HATO
VIA A SSEE ISA 230KV

HOJA: 1

ARCHIVO: EL_HATO.DWG

CODIGO:

EH

DE: 1

C:\Users\Daniel\Desktop\Unifilar.dwg