



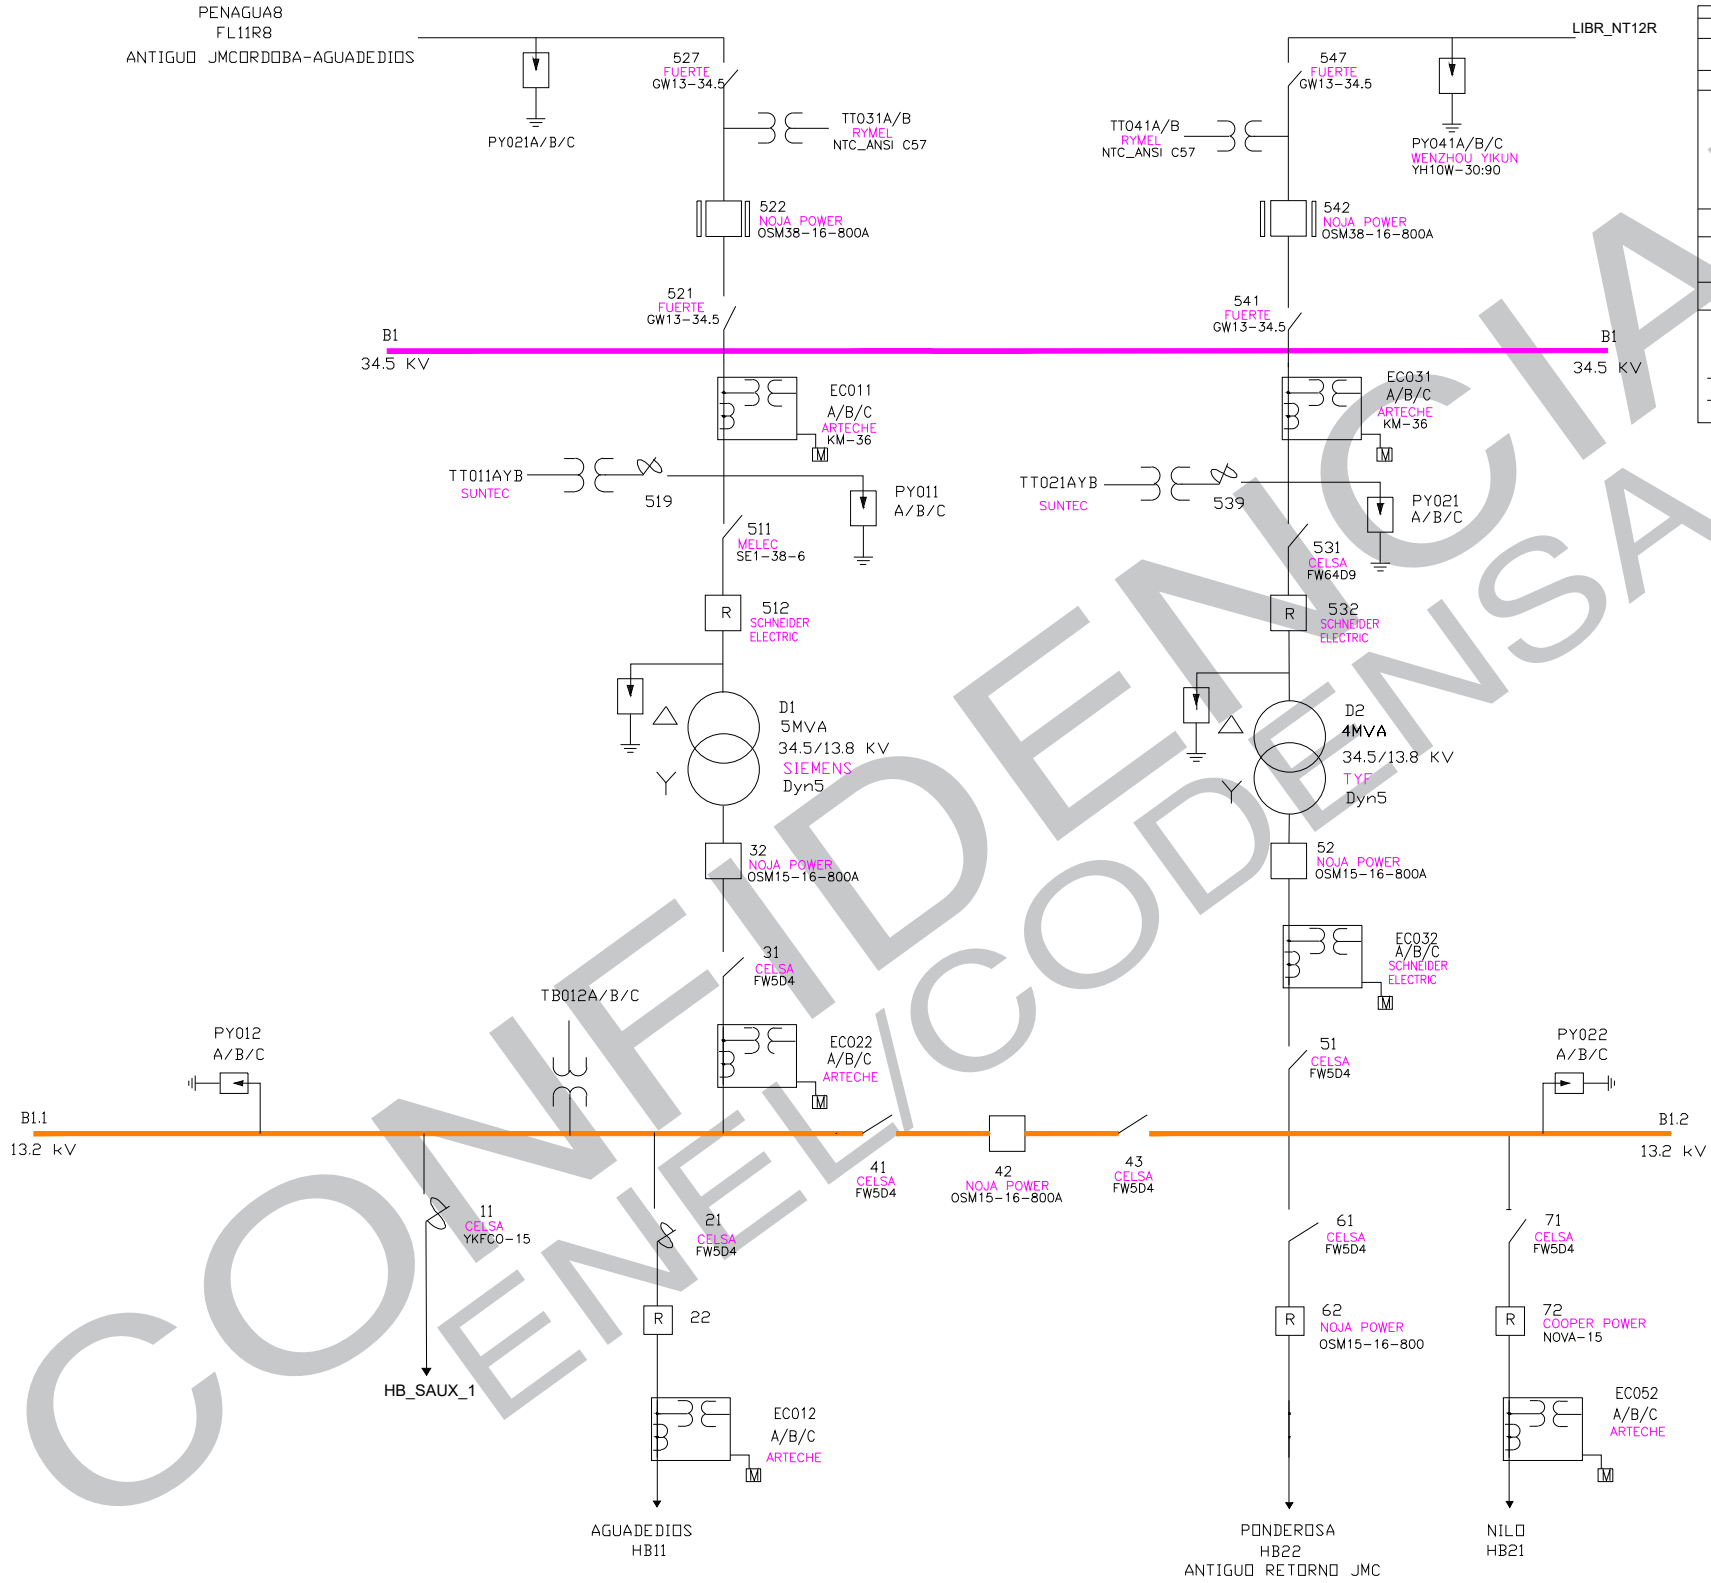

512	D1 SIEMENS	5 MVA
522 F11R8	PANAGUA8	
532	D2 TYF 4	MVA
542	LIBR_NT12R	
11	HB_SAUX_1	→
22	HB11D	→
32	D1 SIEMENS	5 MVA
42	UB B1.1-B1.2	
52	D2 TYF 4	MVA
62	HB22D	PONDEROSA →
72	HB21D	NILO →
← POTENCIA DE ENTRADA		
→ POTENCIA DE SALIDA		

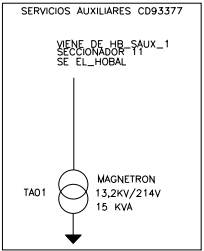

Unidad Organizativa
Administración Información
Técnica Col.

REVISION No. 10

FECHA: MARZO/2022

ARCHIVO: EL_HOBAL.DWG

Y:\FileServer\CONTROL UNIFILARES\UNIFILARES_MARZO_2019

DIAGRAMA UNIFILAR
SUBESTACION EL_HOBAL
MUNICIPIO DE GIRARDOT

CODIGO: HB

701

HOJA: 1

DE: 1