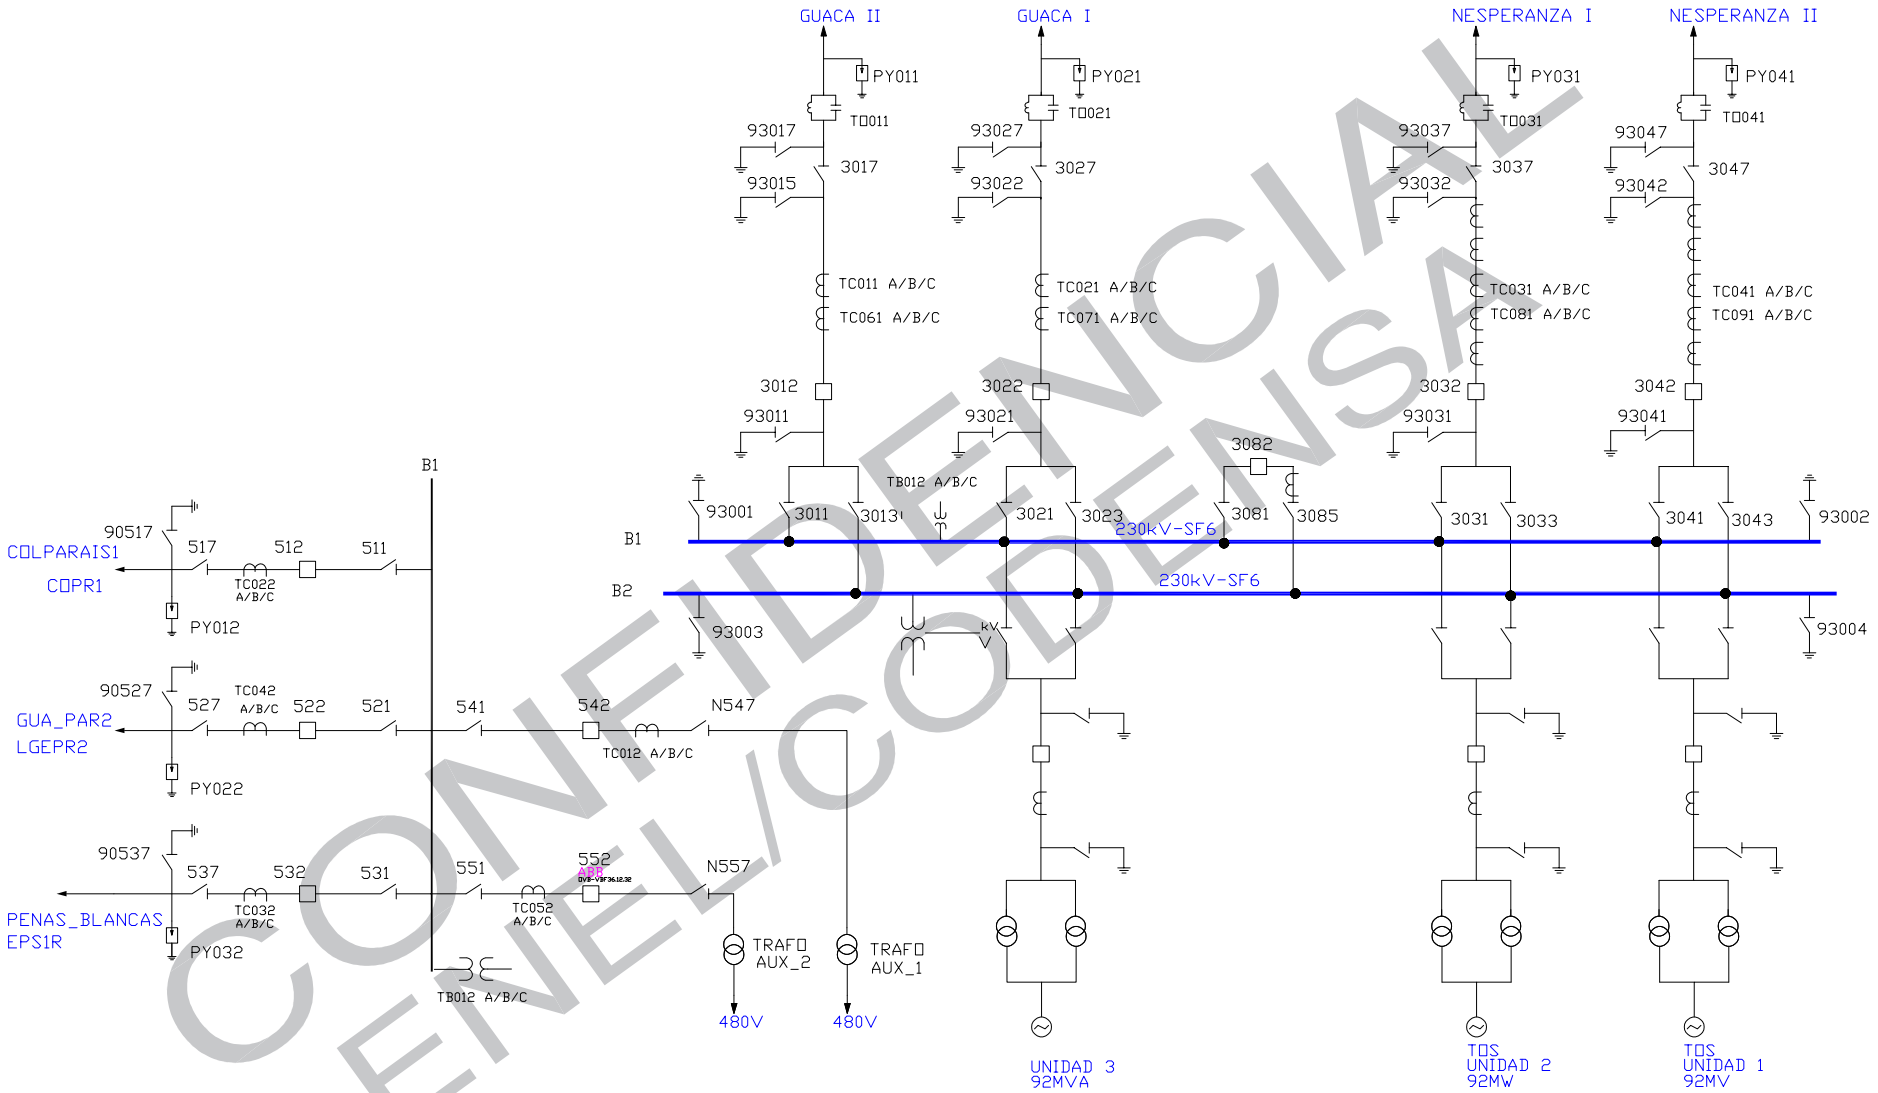

CONFIDENCIAL
ENEL/CODENSA

enel codensa	DEPARTAMENTO GESTION DE LA INFORMACION	REVISION No. 10	DIAGRAMA UNIFILAR
		FECHA: OCTUBRE/2022	SUBESTACION EL_PARAISO
		ARCHIVO: EL PARAISO.DWG	TEL 6274712/4733 PLC219 SIEMENS6536
		C:\ESQUEMAS SUBESTACIONES\ESQUEMAS DEFINITIVOS	Z.R. MPO. EL COLEGIO VDA. EL PARAISO
			CODIGO: EP

18

HOJA: 1

DE: 1