


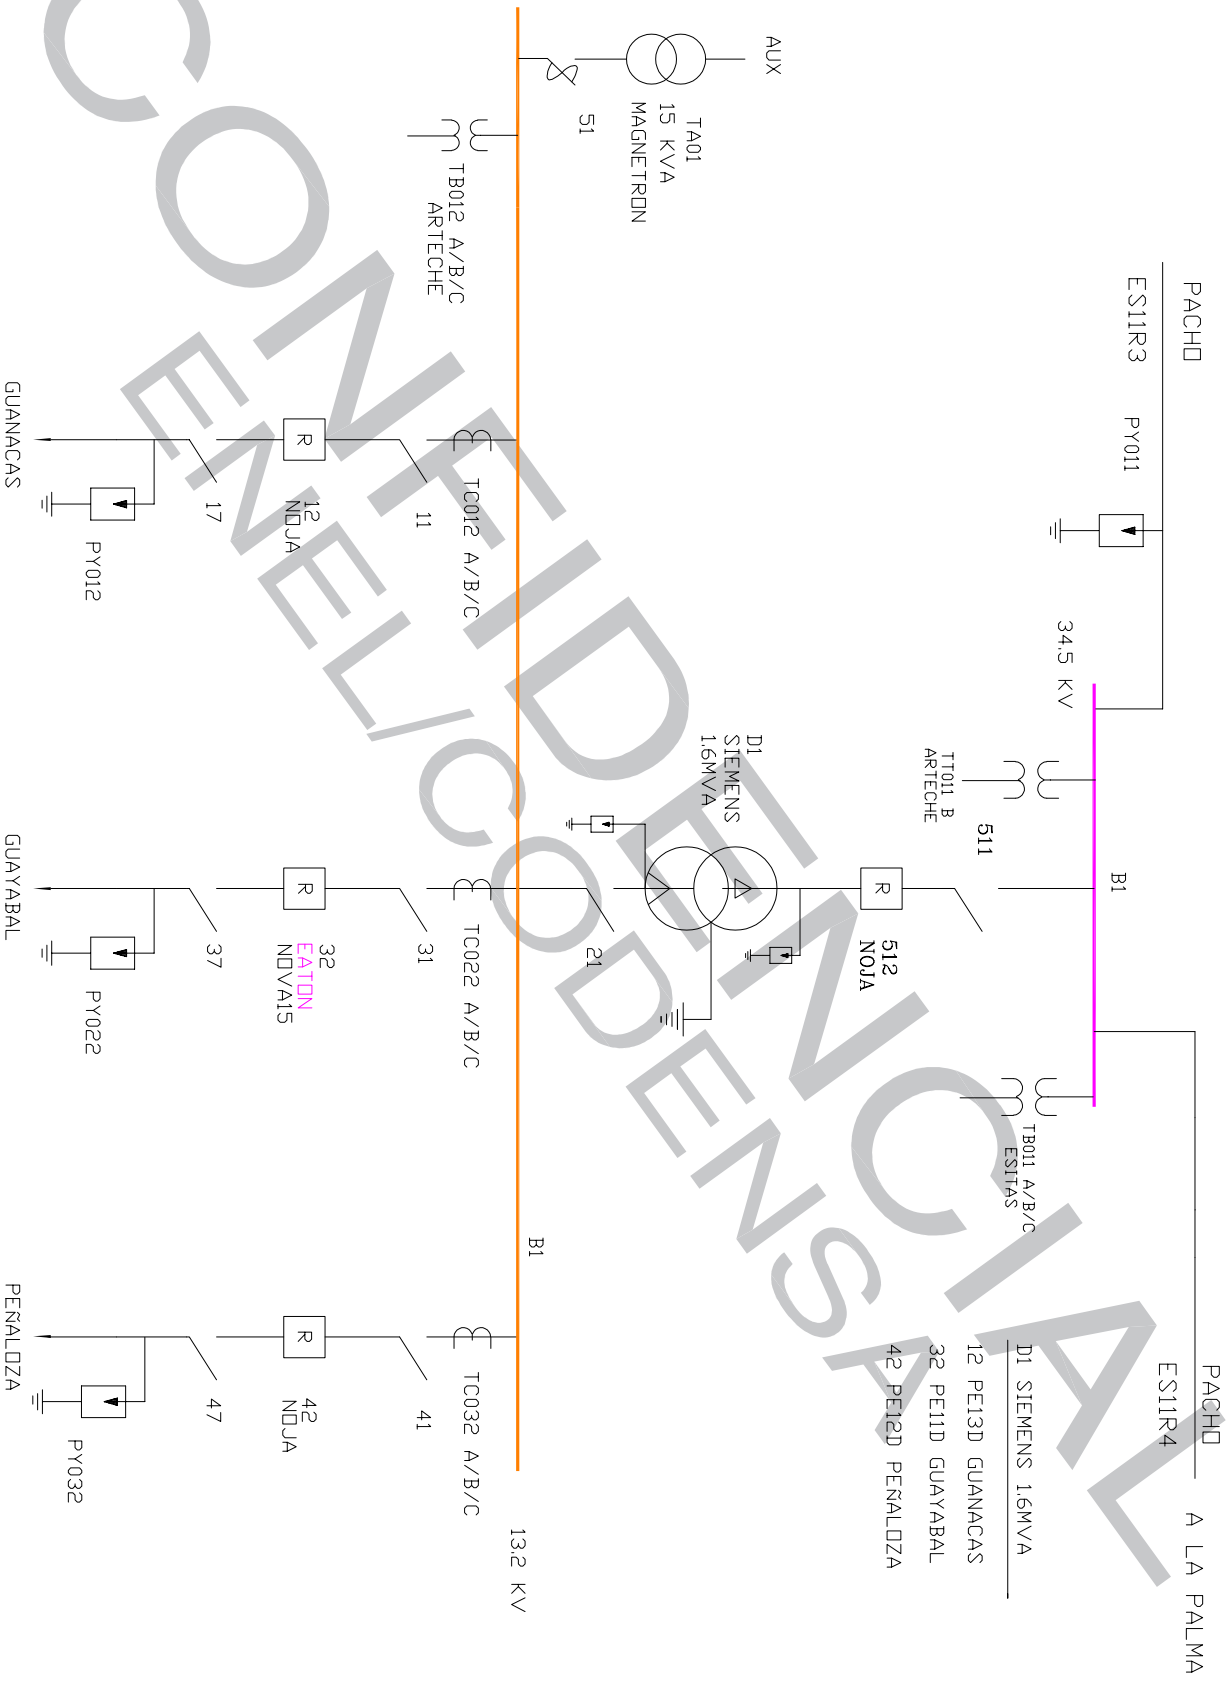

		DEPARTAMENTO INFORMACION TECNICA	
REVISION No.	14	DIAGRAMA UNIFILAR	
FECHA:	SEPTIEMBRE//2022	SUBESTACION EL PENON	
ARCHIVO:	EL PENON.DWG	AFUERAS DEL MPO. EL PENON	
Y:\FisServer\CONTROL UNIFILARES\UNIFILARES_MARZO_2019		LADO DEL MATAOERO	
CODIGO:	PE	DE:	
		HOJA: 1	
		DE: 1	