
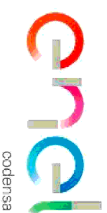


512	D1 SIEMENS 10MA	→
522	D2 SIEMENS 10MA	→
532	M021R1 LA-PAMPA1	→
542	TU11R3 BM03	→
552	UB B1.1-B1.2	→
12	ER13 A.ESQUINAS	→
19	ER12 ER SAUX 2	→
22	D1 SIEMENS 10MA	→
32	ER14 SARMETA	→
42	UB B1.1-B1.2	→
51	ER21 ER SAUX 1	→
62	ER22 CRUZ VERDE	→
72	ER23 LA PINUELA	→
82	D2 SIEMENS 10MA	→
92	ER11 LIBRE-ER11	→
102	ER24 LIBRE-ER24	→
ME04	B1.1	→
ME04	B1.2	→

← POTENCIA DE ENTRADA → POTENCIA DE SALIDA

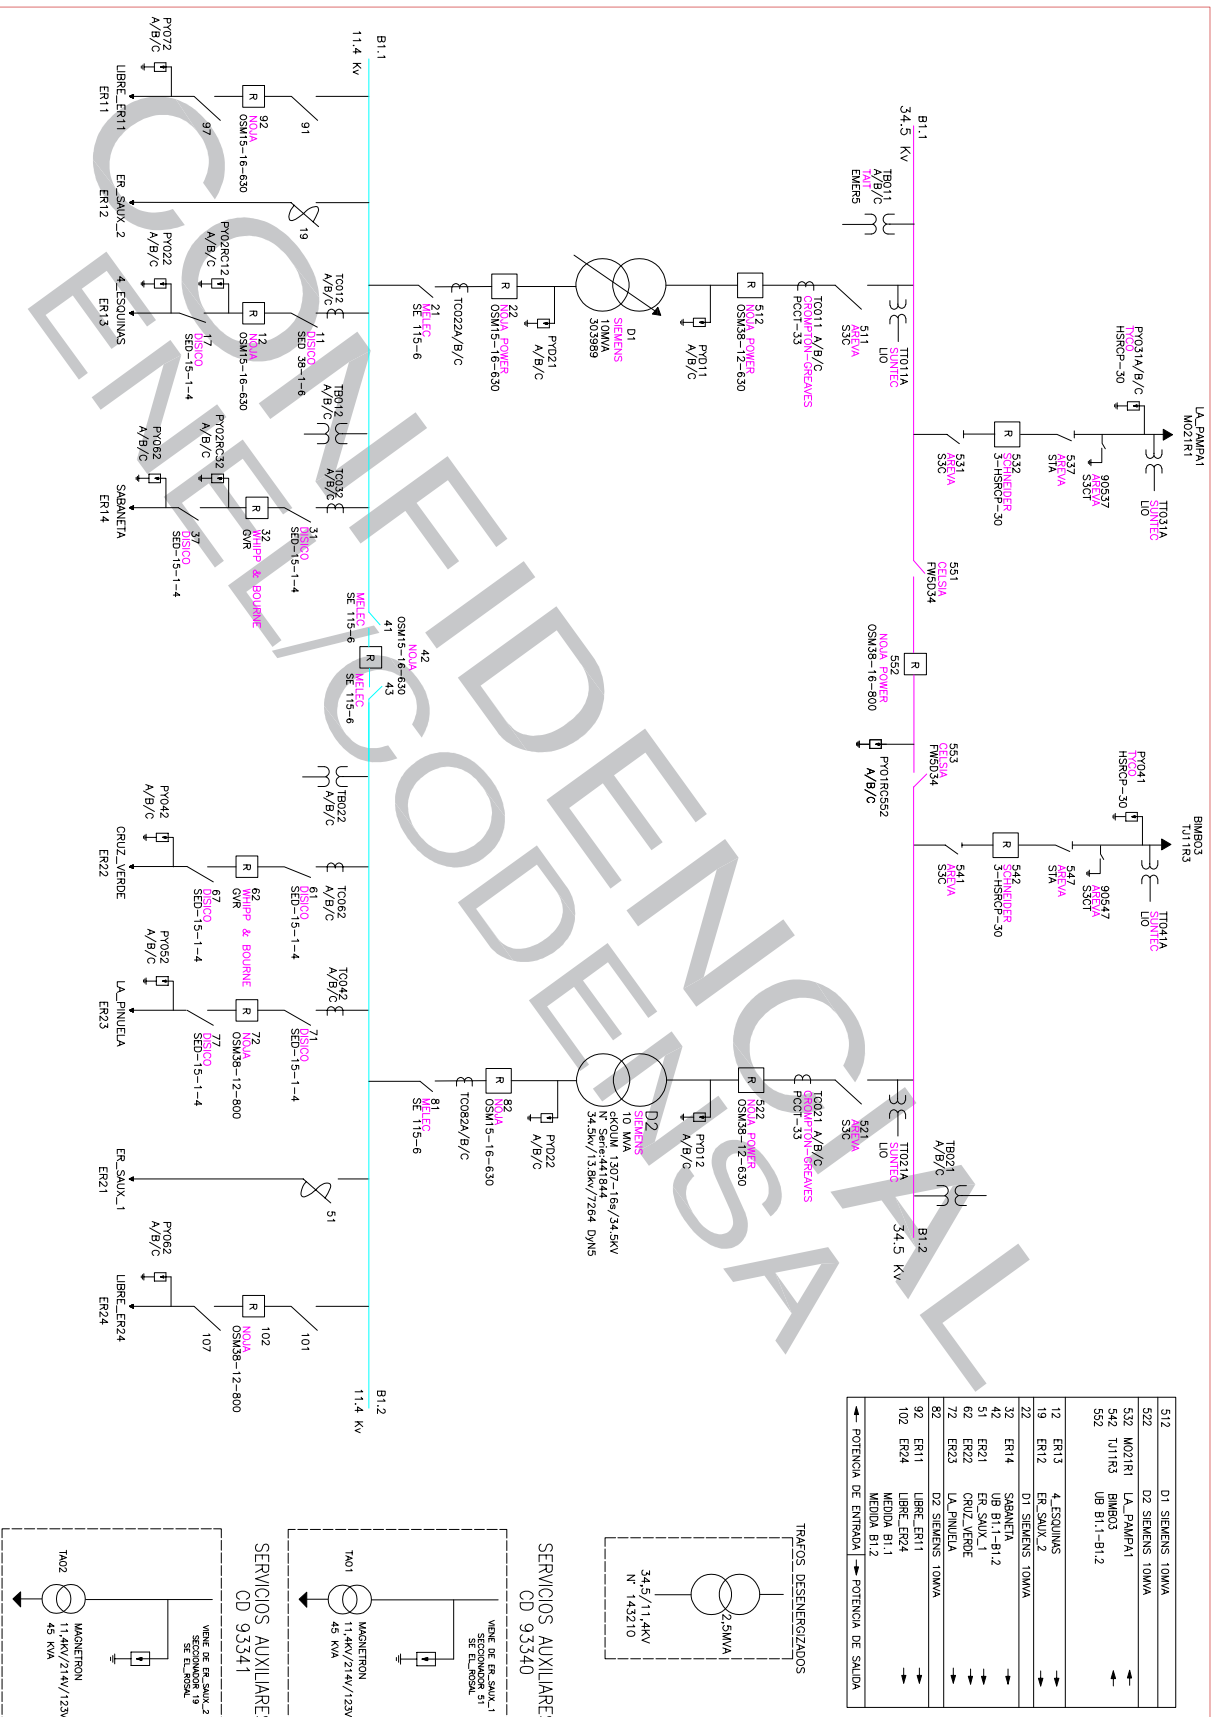

Unidad Organizativa
Administración Informática Col

REVISION No. 19

FECHA: SEPTIEMBRE/2022

ARCHIVO: EL_ROSAL.DWG
Y:\FisServer\CONTROL UNIFILARES\UNIFILARES_ABRIL_2019

DIAGRAMA UNIFILAR

SUBESTACION EL_ROSAL

Entrega municipio el Rosal No principal que se desprende de la autogestión Mediana

CODIGO: ER

75

HOLAJ: 1

DE: 1