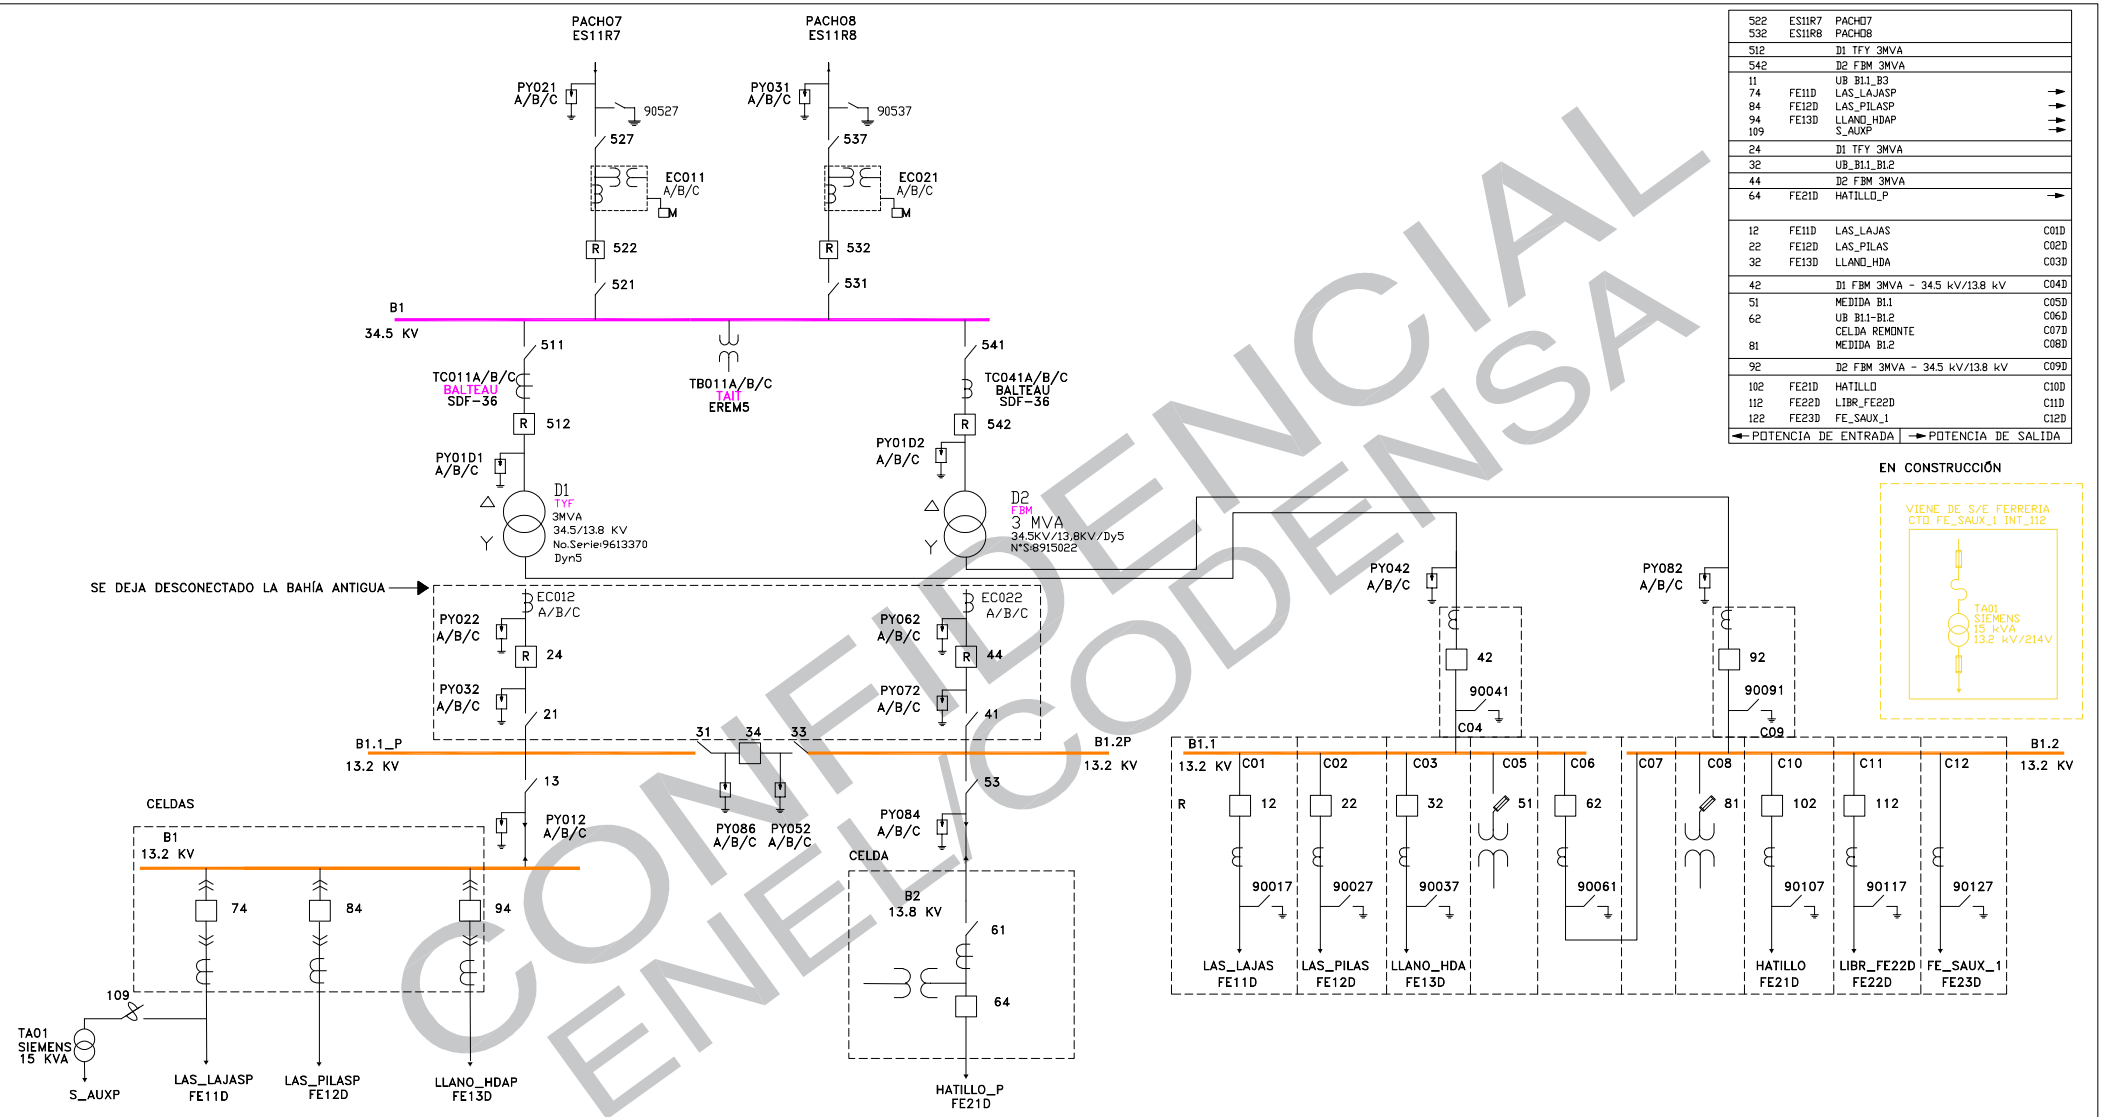

522	ES11R7	PACHO7	
532	ES11R8	PACHO8	
512		D1 TFY 3MVA	
542		D2 FBM 3MVA	
11		UB B1.1_B3	
74	FE11D	LAS_LAJASP	→
84	FE12D	LAS_PILASP	→
94	FE13D	LLAND_HDAP	→
109		S_AUXP	→
24		D1 TFY 3MVA	
32		UB_B1.1_B1.2	
44		D2 FBM 3MVA	
64	FE21D	HATILLO_P	→
12	FE11D	LAS_LAJAS	C01D
22	FE12D	LAS_PILAS	C02D
32	FE13D	LLAND_HDA	C03D
42		D1 FBM 3MVA - 34.5 kV/13.8 kV	C04D
51		MEDIDA B1.1	C05D
62		UB B1.1-B1.2	C06D
		CELDA REMONTE	C07D
81		MEDIDA B1.2	C08D
92		D2 FBM 3MVA - 34.5 kV/13.8 kV	C09D
102	FE21D	HATILLO	C10D
112	FE22D	LIBR_FE22D	C11D
122	FE23D	FE_SAUX_1	C12D

← POTENCIA DE ENTRADA | → POTENCIA DE SALIDA

CONFIDENCIAL
ENEL CODENSA

codensa

Unidad Organizativa
Administración Información
Técnica Col

REVISION No. 14
FECHA: NOVIEMBRE/2022
ARCHIVO: FERRERIA.DWG
C:\ESQUEMAS SUBESTACIONES\ESQUEMAS DEFINITIVOS

DIAGRAMA UNIFILAR
SUBESTACION FERRERIA
ANTIGUO PACHO
MUNICIPIO DE PACHO
CODIGO: FE

613
HOJA: 1
DE: 1