




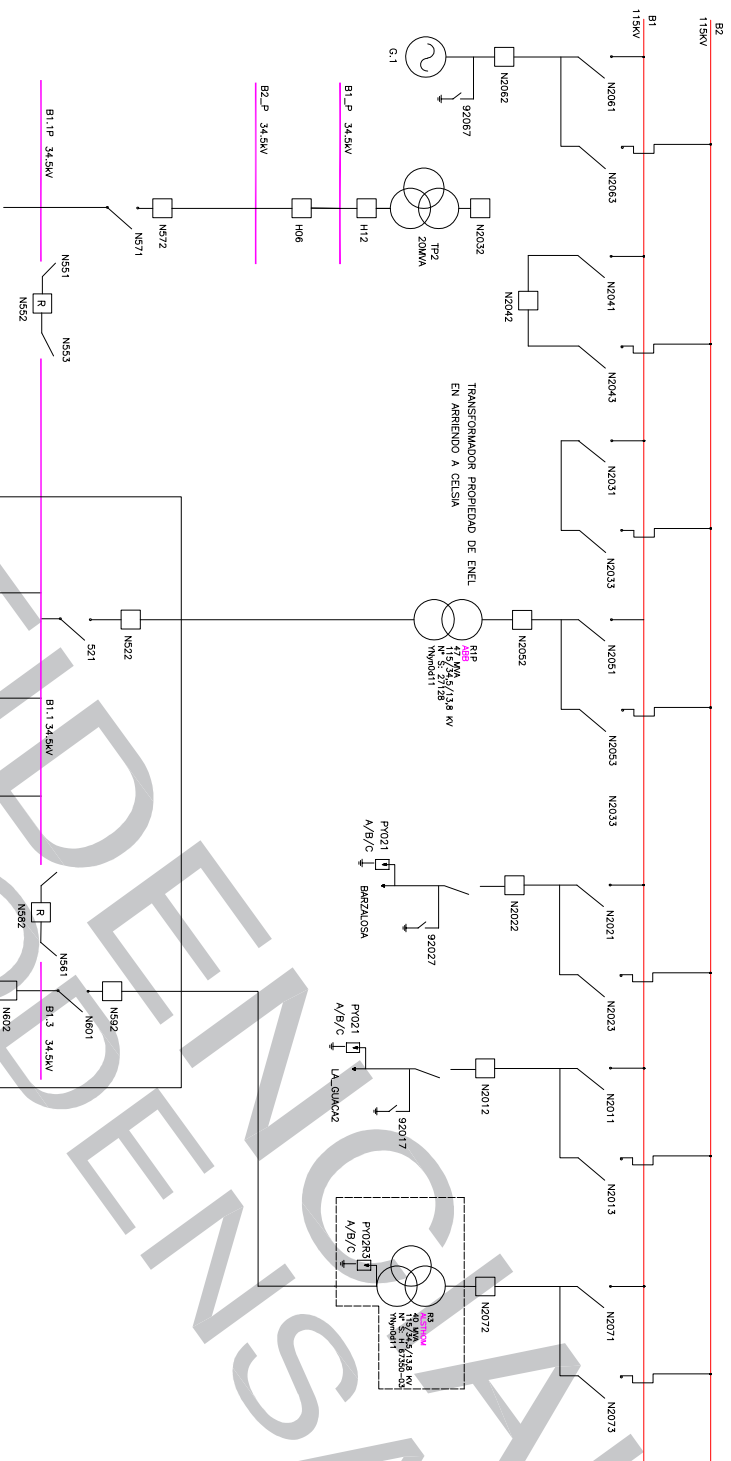


N602	FL31R	GIRARDOTP
N642	FL31R	ISLAENOP
N532	FL12R	PENAGUAP
N512	FL11R	TOLEMADAP
N2052	R1	47MVA PRIMARIO
N2032	R1	47MVA SECUNDARIO
N2032	R2	40MVA PRIMARIO
N572	R2	40MVA SECUNDARIO
N2072	R3	25MVA PRIMARIO
N592	R3	25MVA SECUNDARIO
N562	D1	SECUNDARIO
N42	D1	SECUNDARIO
N12	FL11D	TRONAP
N22	FL12D	LIBR.FL12P
N32	FL13D	TARONAP
N562	UB.B1.1.B1.2	
N552	UB.B1.1.B1.2	

EQUIPOS PROPIEDAD DE ENEL
TRAF0 R1 y CABLE NIVEL III
EN PANTO BAHIA ISLA, PERSON
EXCEPTO EQUIPOS DE CONTROL Y PRTT FL13D

EQUIPOS A RETIRAR DE CELSIA

EQUIPOS CONECTADOS EN CELDAS GIS CELSIA

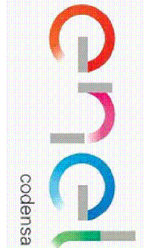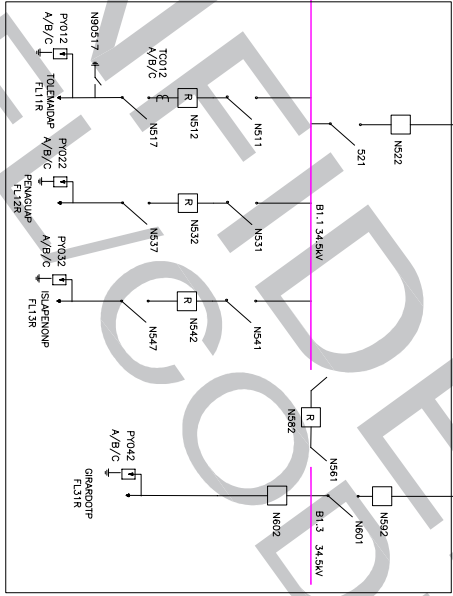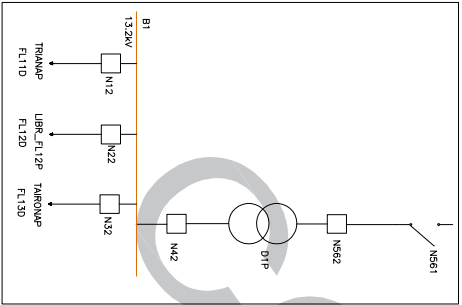

Unidad Organizativa
Administración Informativa
Técnica Col

REVISIÓN No. 8

FECHA: ENERO/2023

ARCHIVO: FLANDES.DWG
Y:\FieServer\CONTROL UNIFILARES\UNIFILARES_MARZO_2019

DIAGRAMA UNIFILAR

SUBSTACION FLANDES
M/PIO. DE FLANDES DEP. DEL TOLIMA

CODIGO: FL

127

HOLDA: 1

DE: 2