
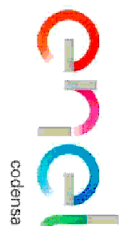


CO2R4	COVIANDES4	→
S12	DI SIEMENS 3/3,75 MVA	
12	F011D LAVADERO	→
29	F013D FQ_S AUX_1	→
31	UB B11-B12	
42	F012D GRAMAL	→
S1	DI SIEMENS 3/3,75 MVA	

← POTENCIA DE ENTRADA → POTENCIA DE SALIDA

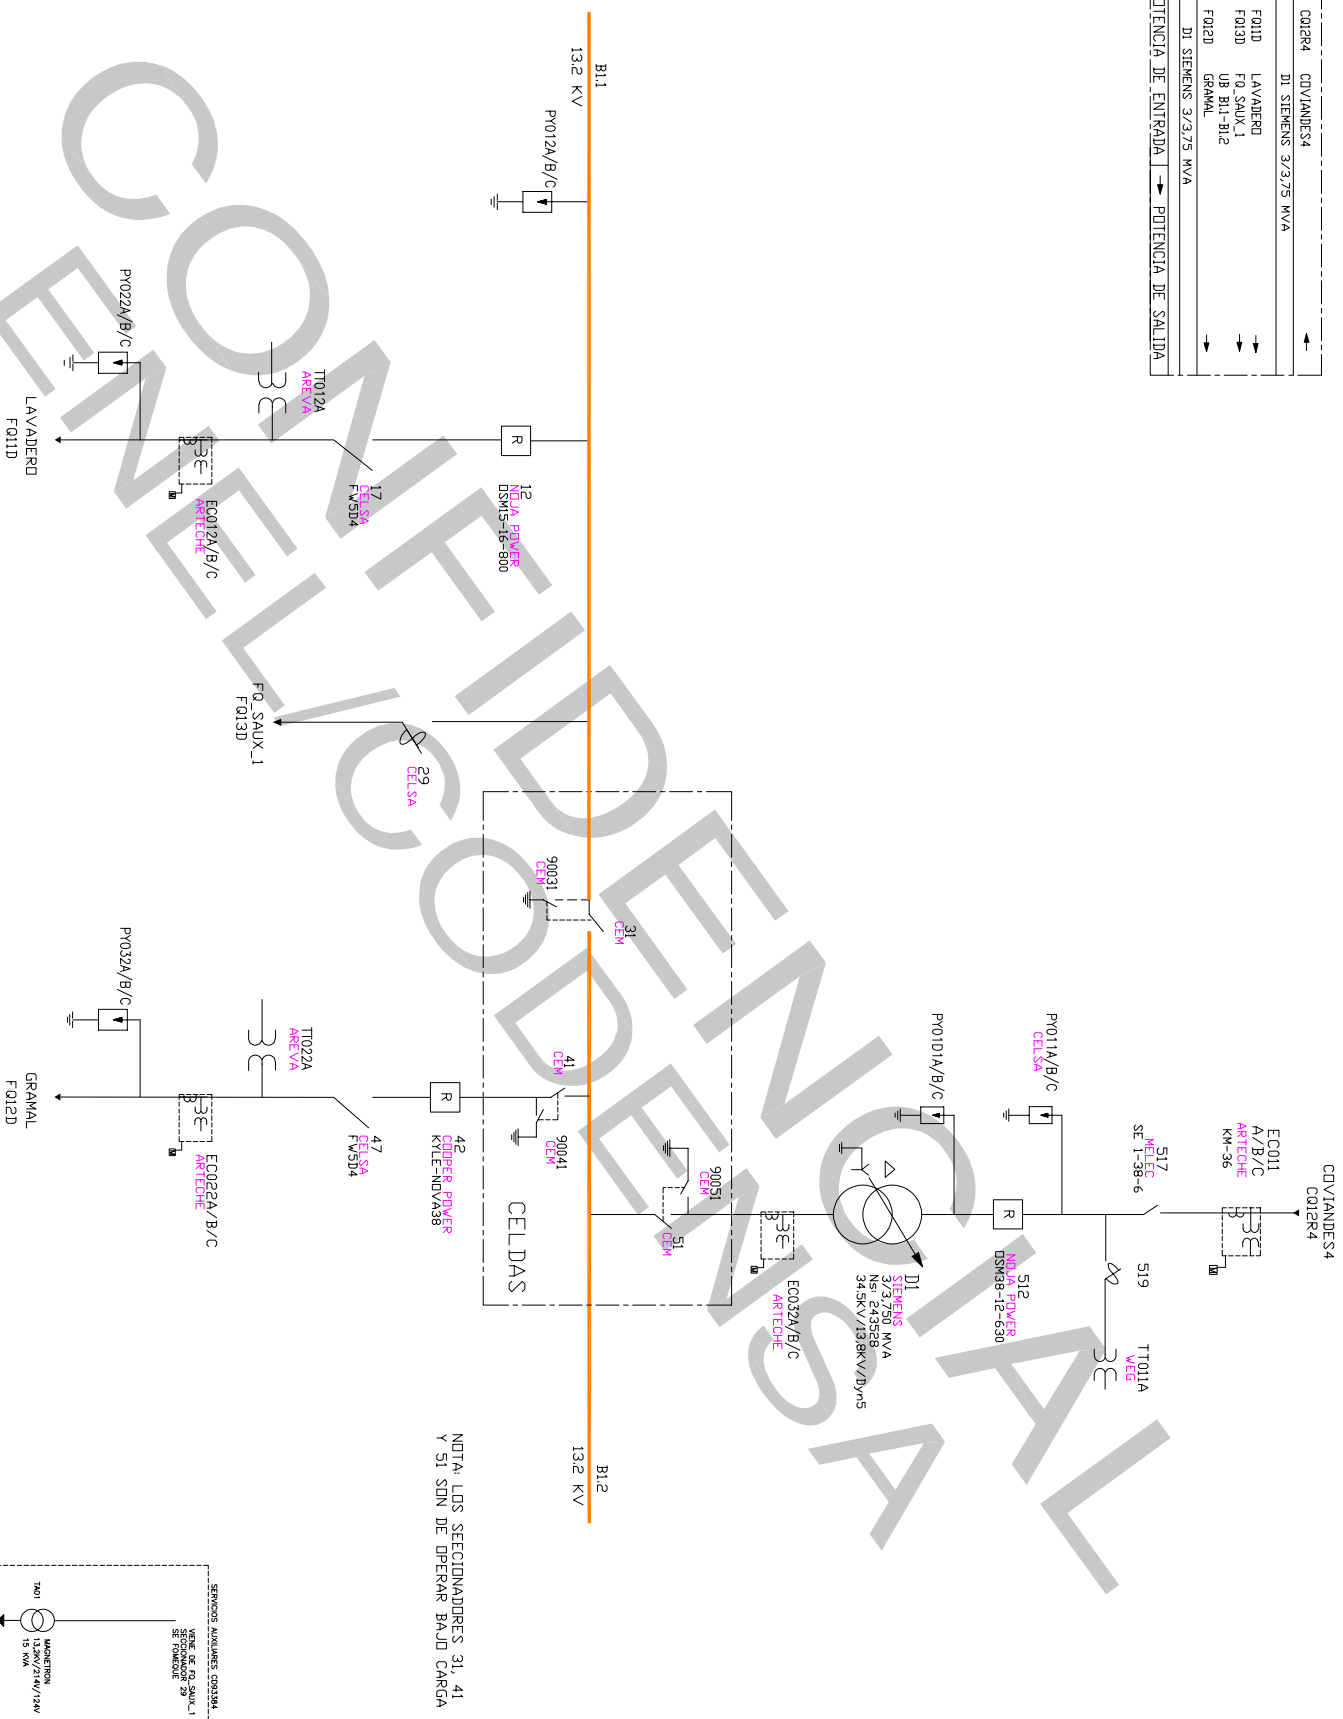

Unidad Organizativa
Administración Informacion
Técnica Col

REVISION No.	8	DIAGRAMA UNIFILAR	612
FECHA:	NOVIEMBRE/2022	SUBESTACION FOMEQUE	HOJA: 1
ARCHIVO:	FOMEQUE.DWG	MUNICIPIO DE FOMEQUE	DE: 1
Y:\Frieserve\CONTROL UNIFILARES UNIFILARES_JAMRZO_2019		CODIGO: FQ	