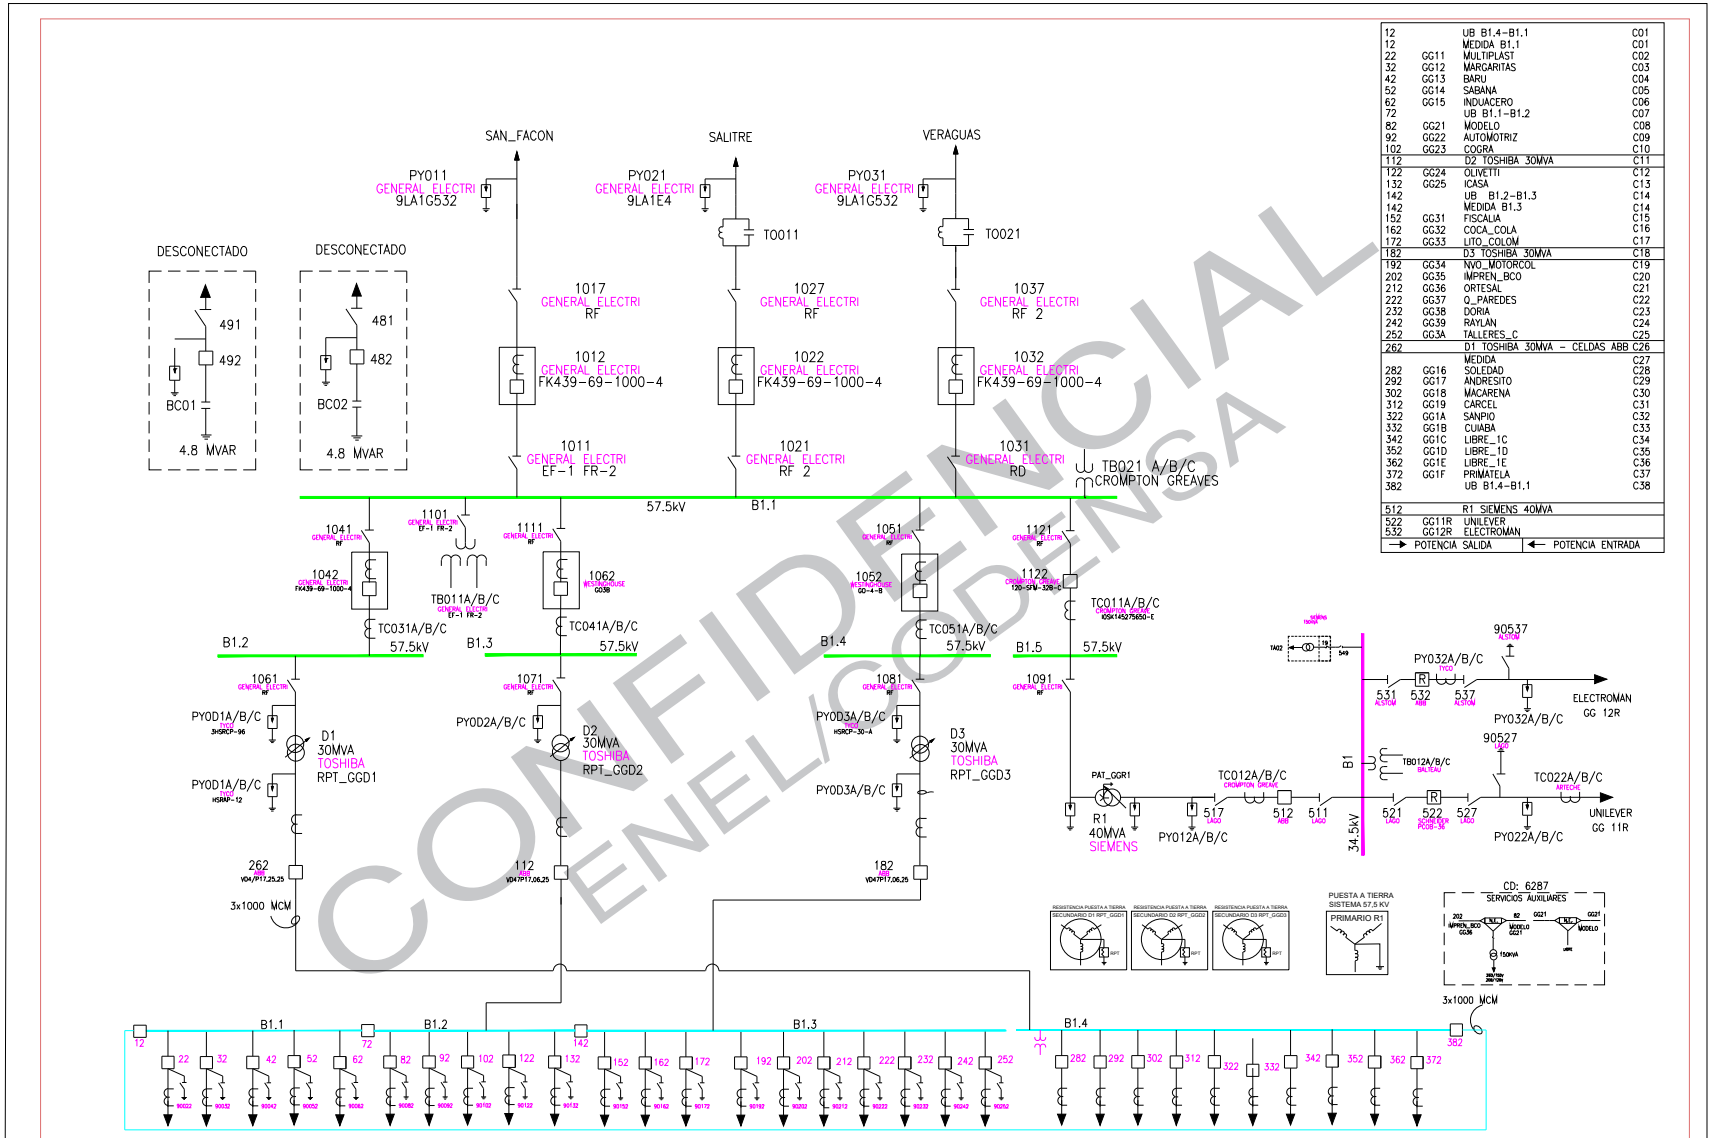

12		UB B1.4-B1.1	C01
12		MEDIDA B1.1	C01
22	GG11	MULTIPLAST	C02
32	GG12	MARGARITAS	C03
42	GG13	BARU	C04
52	GG14	SABANA	C05
62	GG15	INDUACERO	C06
72		UB B1.1-B1.2	C07
82	GG21	MODELO	C08
92	GG22	AUTOMOTRIZ	C09
102	GG23	COGRA	C10
112		D2 TOSHIBA 30MVA	C11
122	GG24	OLIVETTI	C12
132	GG25	ICASA	C13
142		UB B1.2-B1.3	C14
142		MEDIDA B1.3	C14
152	GG31	FISCALIA	C15
162	GG32	COCA_COLA	C16
172	GG33	LITO_COLOM	C17
182		D3 TOSHIBA 30MVA	C18
192	GG34	NVO_MOTORCOL	C19
202	GG35	IMPREN_BCO	C20
212	GG36	ORTESAL	C21
222	GG37	Q_PAREDES	C22
232	GG38	DORIA	C23
242	GG39	RAYLAN	C24
252	GG3A	TALLERES_C	C25
262		D1 TOSHIBA 30MVA - CELDAS ABB	C26
		MEDIDA	C27
282	GG16	SOLEDAD	C28
292	GG17	ANDRESITO	C29
302	GG18	MACARENA	C30
312	GG19	CARCEL	C31
322	GG1A	SANPIO	C32
332	GG1B	CUIABA	C33
342	GG1C	LIBRE_1C	C34
352	GG1D	LIBRE_1D	C35
362	GG1E	LIBRE_1E	C36
372	GG1F	PRIMATELA	C37
382		UB B1.4-B1.1	C38
512		R1 SIEMENS 40MVA	
522	GG11R	UNILEVER	
532	GG12R	ELECTROMAN	

→ POTENCIA SALIDA | ← POTENCIA ENTRADA

CONFIDENCIAL
ENEL/CODENSA

enel codensa	Unidad Organizativa Administración Información Técnica Col.	REVISION No. 25	DIAGRAMA UNIFILAR
		FECHA: NOVIEMBRE/2022	SUBESTACION GORGONZOLA CALLE 13 N° 39-61 TEL. 2472990 SIEMENS 6542
		ARCHIVO: GORGONZOLA.DWG Y:\CONTROL UNIFILARES\UNIFILARES_DICIEMBRE_2019	CODIGO: GG
			21 HOJA: 1 DE: 1