
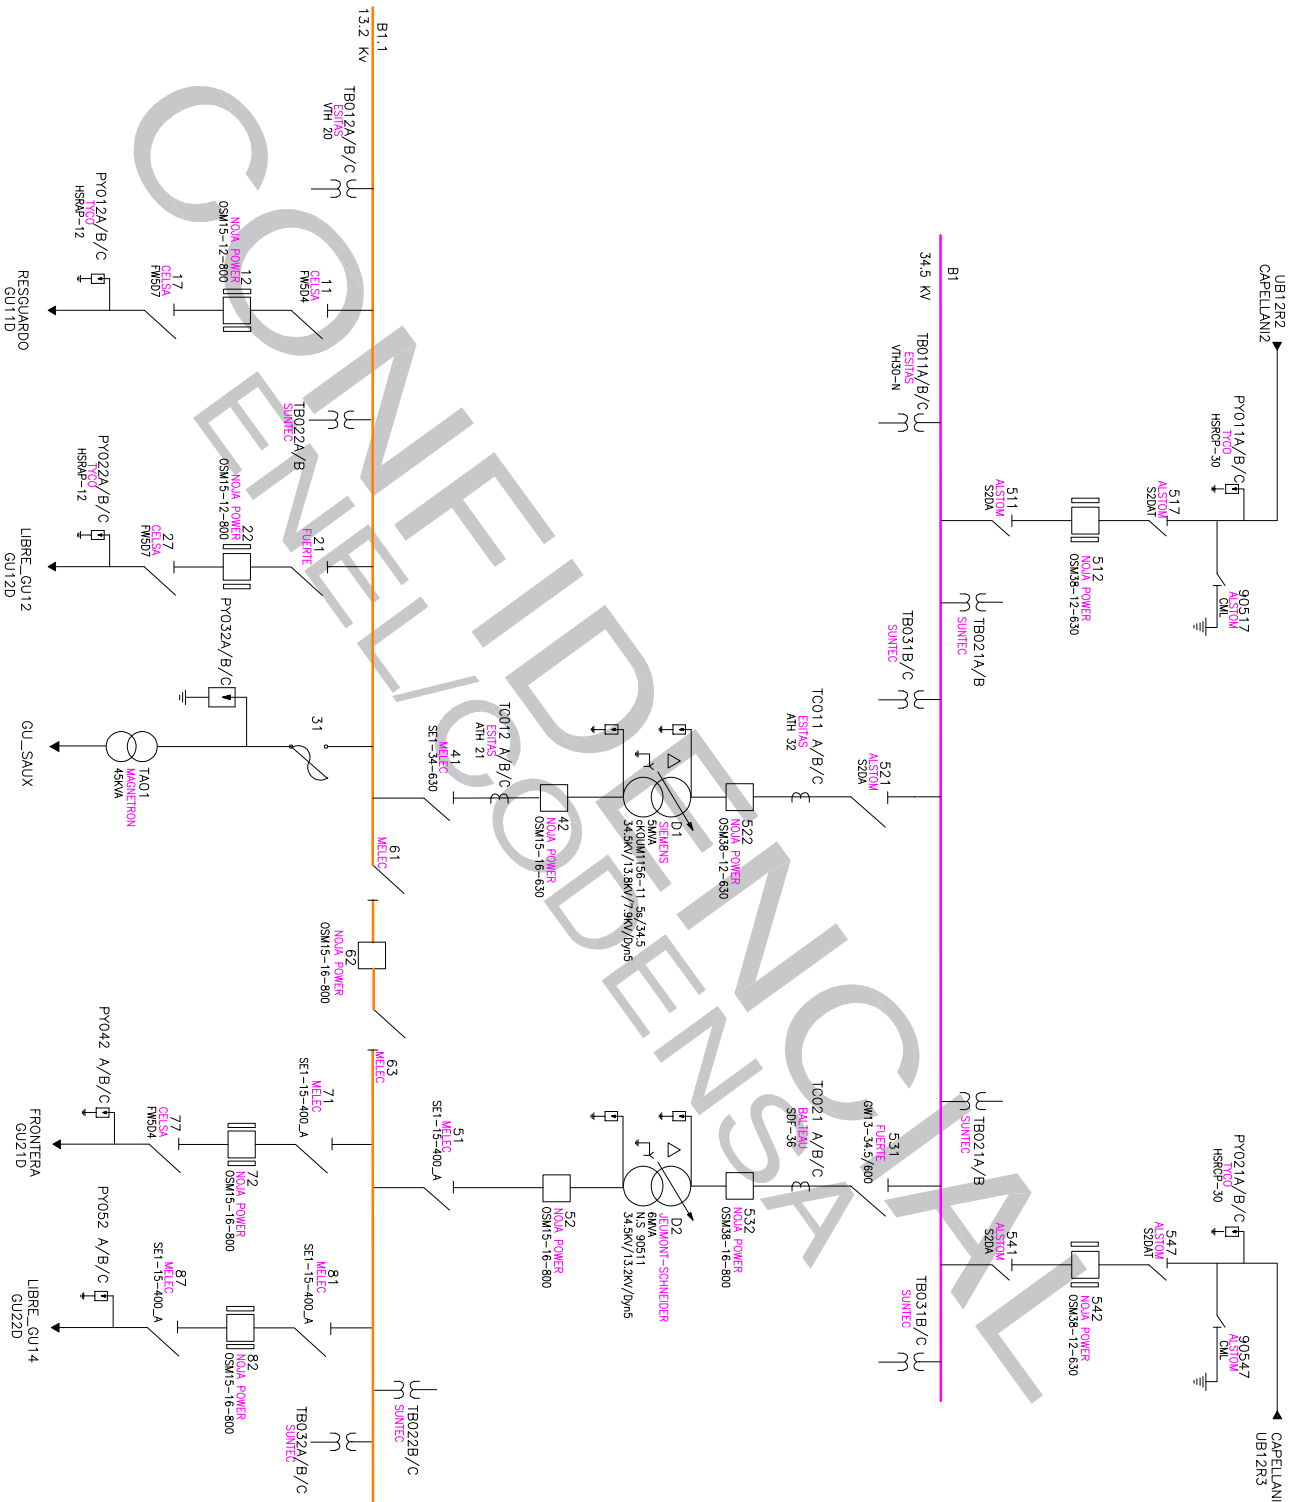


512	UB12R2	CAPELLANIZ	→
522	UB12R3	CAPELLANIZ	→
42	GU10	D1 SERVIDOR BANA	→
12	GU110	RESGUARDO	→
22	GU120	LIBRE_GU12	→
31		GU130X	→
522		D2 JUMINAT-SCHNEIDER BANA	→
52	GU120	D2 JUMINAT-SCHNEIDER BANA	→
72	GU210	LIBRE_GU14	→
82	GU220	LIBRE_GU14	→
82		UB B1-1-B1-2 13.2KV	→

SERVICIOS AUXILIARES
CD33386

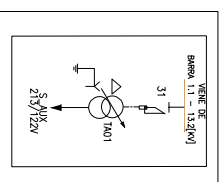

Unidad Organizativa
Administración Informática
Técnica Col.

REVISION No. 10

FECHA: AGOSTO/2021
ARCHIVO: GUACHETA.DWG

DIAGRAMA UNIFILAR
SUBESTACION GUACHETA
VEREDA LA FRONTERA, FINCA SAN ANTONIO,
MUNICIPIO DE GUACHETA

CODIGO: GU
DE: 1

151