


19	JN15D	JN SAUX.1
22	JN12D	GACHETA
32	JN12D	CHUSCALES
41		UB. B11, B12
51	JN13D	D1 SIEMENS 3.75MVA
62	GAMA	
72	JN14D	NEMOSTEN

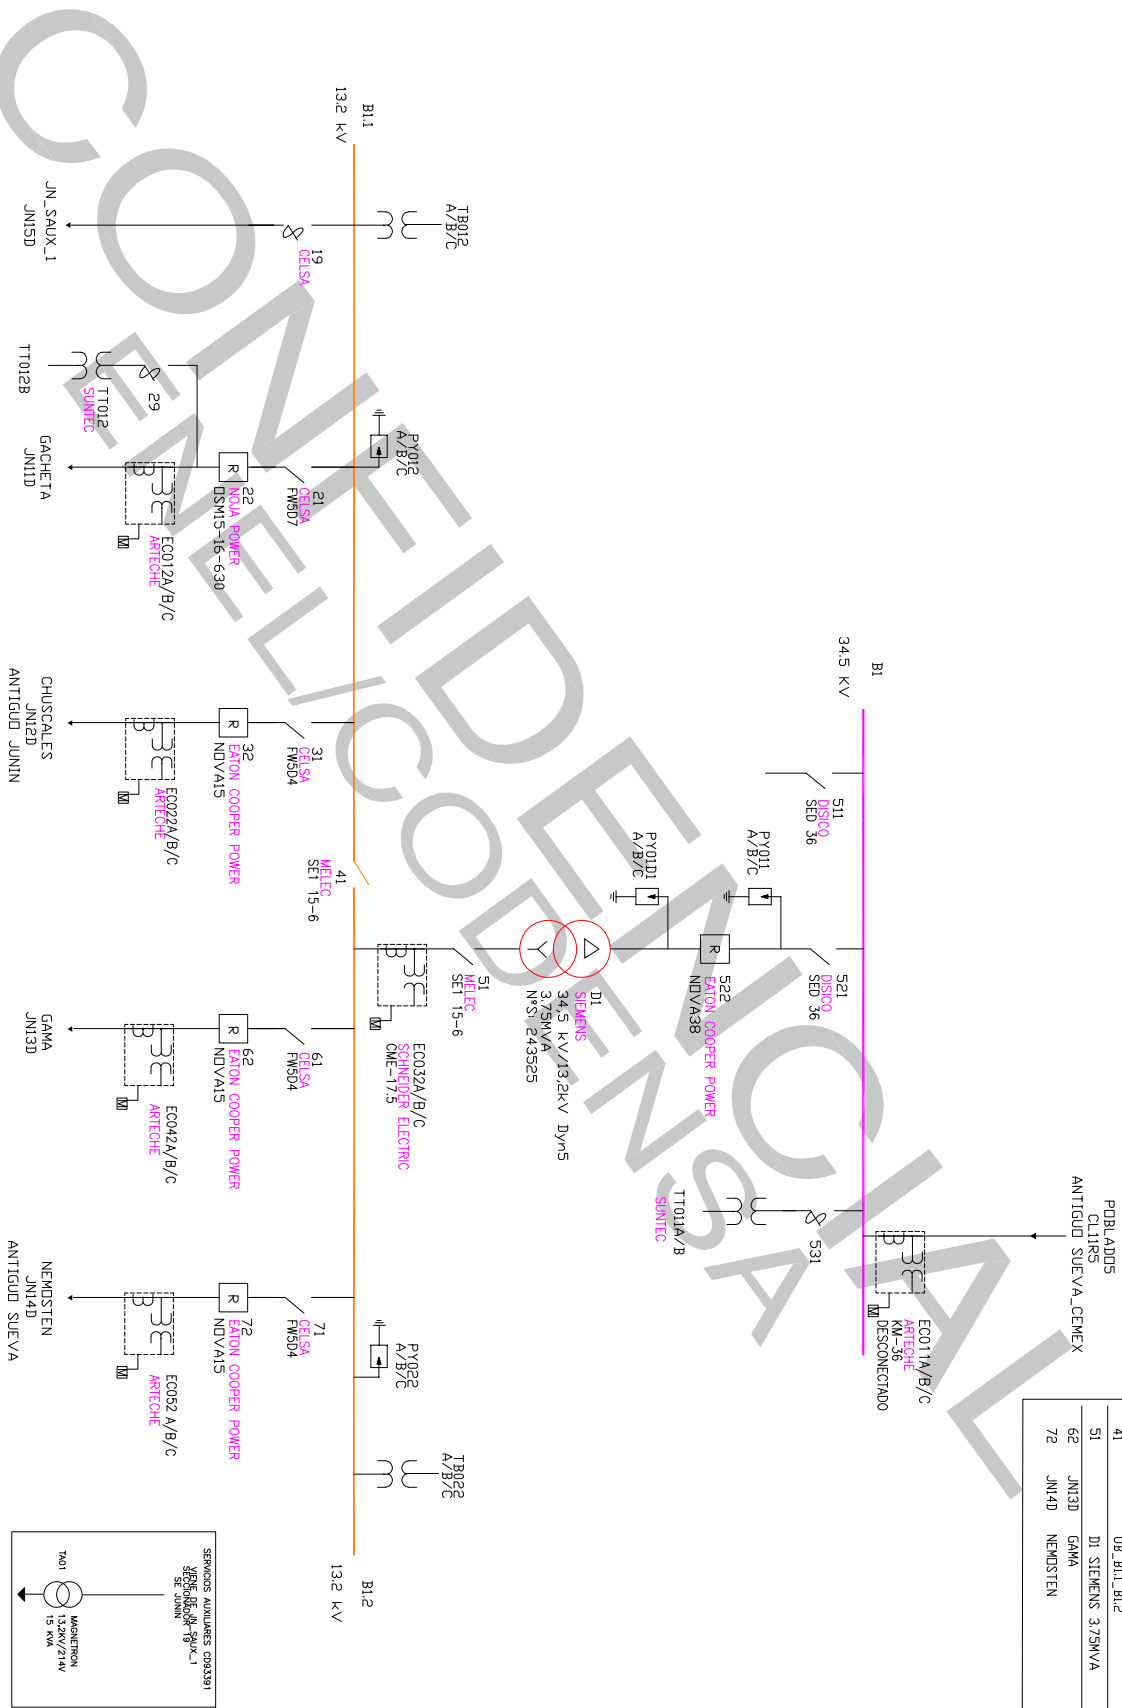



Unidad Organizativa

Administración Informacon

Técnica Col.

REVISION No.

6

DIAGRAMA UNIFILAR

FECHA:

MAYO/2022

SUBSTACION JUNIN

ARCHIVO:

JUNIN.DWG

ANTIGUO GACHETA

CODIGO:

JN

MUNICIPIO DE GACHETA

DE:

1

HOJA:

1

601