

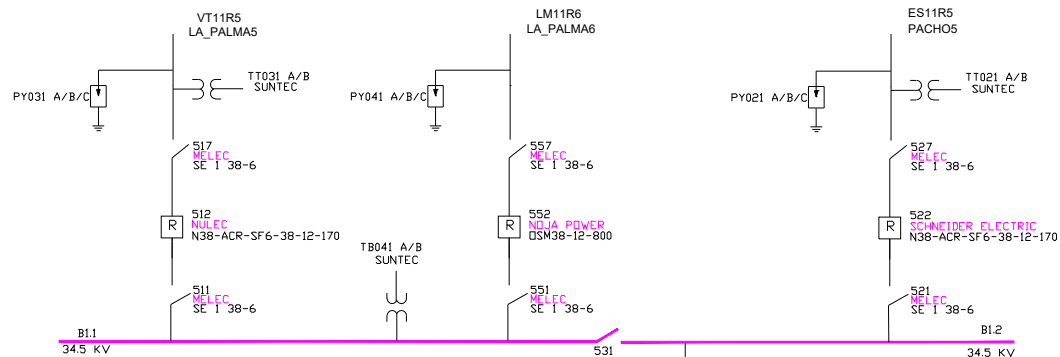


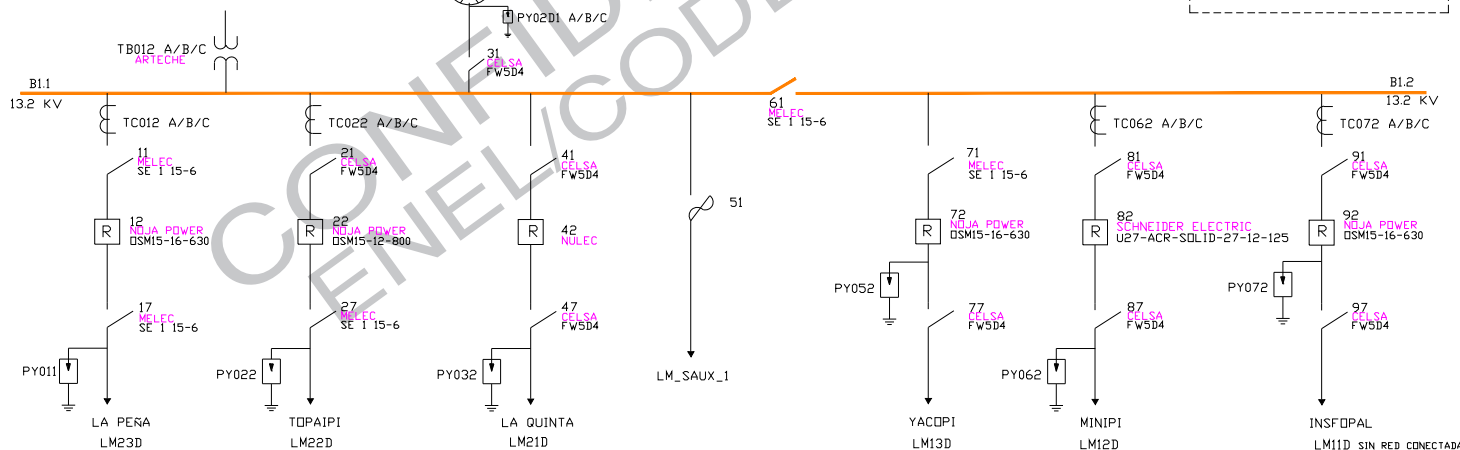

512	VT11R5	LAS_PALMA5
522	ES11R5	PACHO5
531		UB B1.1-B1.2
542		D1 SIEMENS 5MVA
552	LM11R6	LA_PALMA6
		MEDIDA B1.3
		MEDIDA B1.1
12	LM23D	LA PERA
22	LM22D	TOPAIP1
31		D1 SIEMENS 5MVA
42	LM21D	LA_QUINTA
51		LM_SAUX_1
61		UB B1.1-B1.2
72	LM13D	YACOP1
82	LM12D	NINIPI
92	LM11D	INSFOPAL

← POTENCIA DE ENTRADA → POTENCIA DE SALIDA

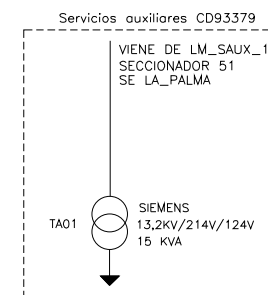

Unidad Organizativa
Administración Informacion
Técnica Col

REVISION No. 21
FECHA: ABRIL/2022
ARCHIVO: LA PALMA.DWG
\\COLC009F501\FileSystem\CONTROL UNIFILARES

DIAGRAMA UNIFILAR
SUBSTACION LA PALMA
AFUERAS DEL MPO.COSTADO IZO VIA LA PALMA-PACHO
CALLE_ 9_4_35 barrio matadero nueva frente estadio

CODIGO: LM

81

HOJA: 1
DE: 1