

511	TU11R2	BIMB02	→
541	NO11R1	EL_VINO	→
532	D1	SIEMENS 10MVA PRIMARIO	→
61	D1	SIEMENS 10MVA SECUNDARIO	→
82	PT11D	RETEN	→
71	PT12D	LIBRE PT14	→
12	PT13D	S_AUX	→
522	D2	ABB 5 MVA PRIMARIO	→
31	D2	ABB 5 MVA SECUNDARIO	→
12	PT21D	PALMACERA	→
22	PT22D	PTC_PIEDRA	→
41	ACOPLE B1-1-B1-2 11.4KV		
→ POTENCIA DE ENTRADA			
→ POTENCIA DE SALIDA			

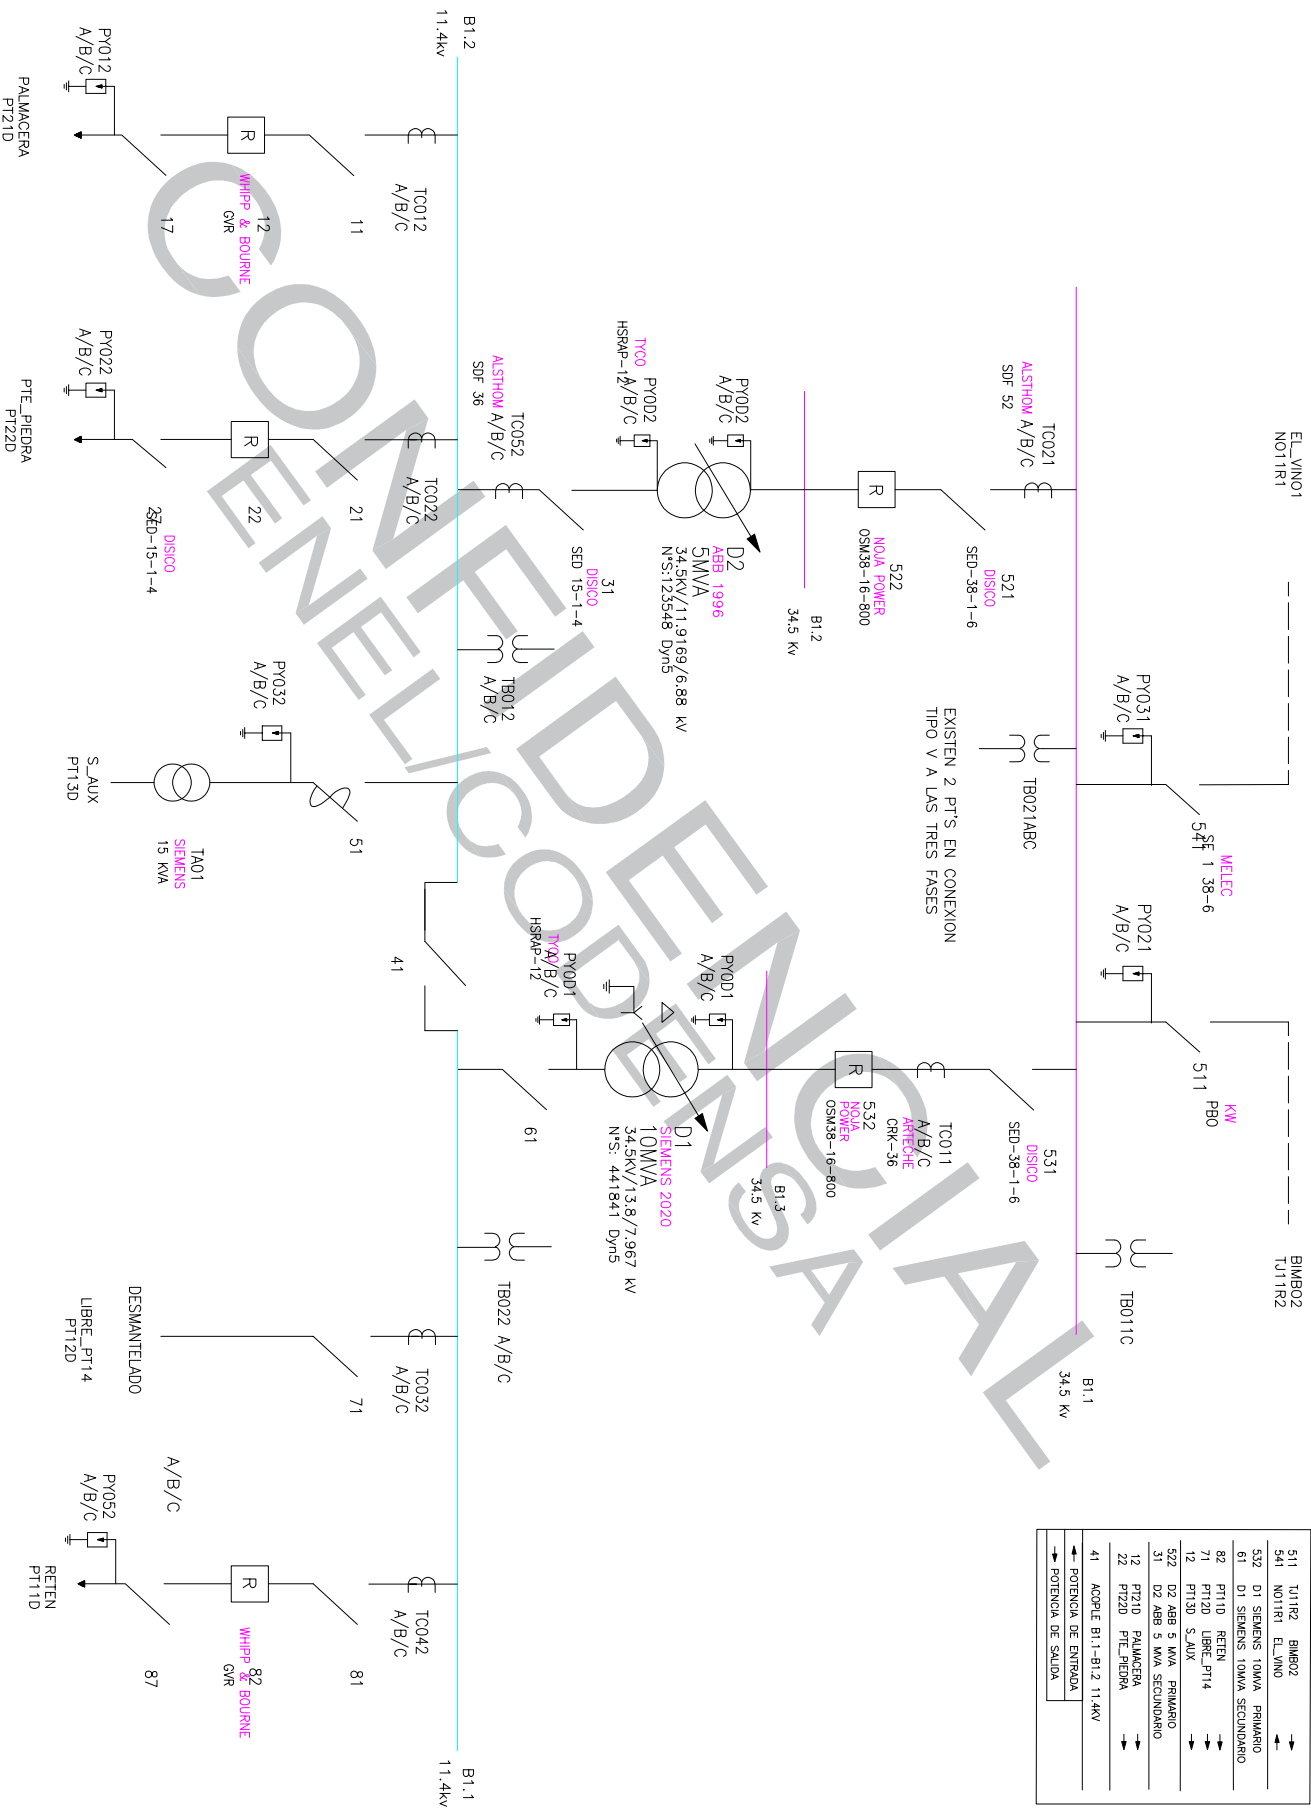


DIAGRAMA UNIFILAR

83

FECHA:		ENERO/2022		SUBESTACION LA_PUNTA		03
ARCHIVO:		LA_PUNTA.DWG		AUTOMEDILUN A 1.5KW PEALÉ DE SIBERIA. COST. IZQ CONTIGUO A LA ESTACION DE POLICIA VEREDA LA PUNTA		
Y:\FisServer\CONTROL UNIFILARES\UNIFILARES_ABRIL_2019		CODIGO:		PT		
				DE:	1	

Unidad Organizativa
Administración Informativa
Técnica Col.

