


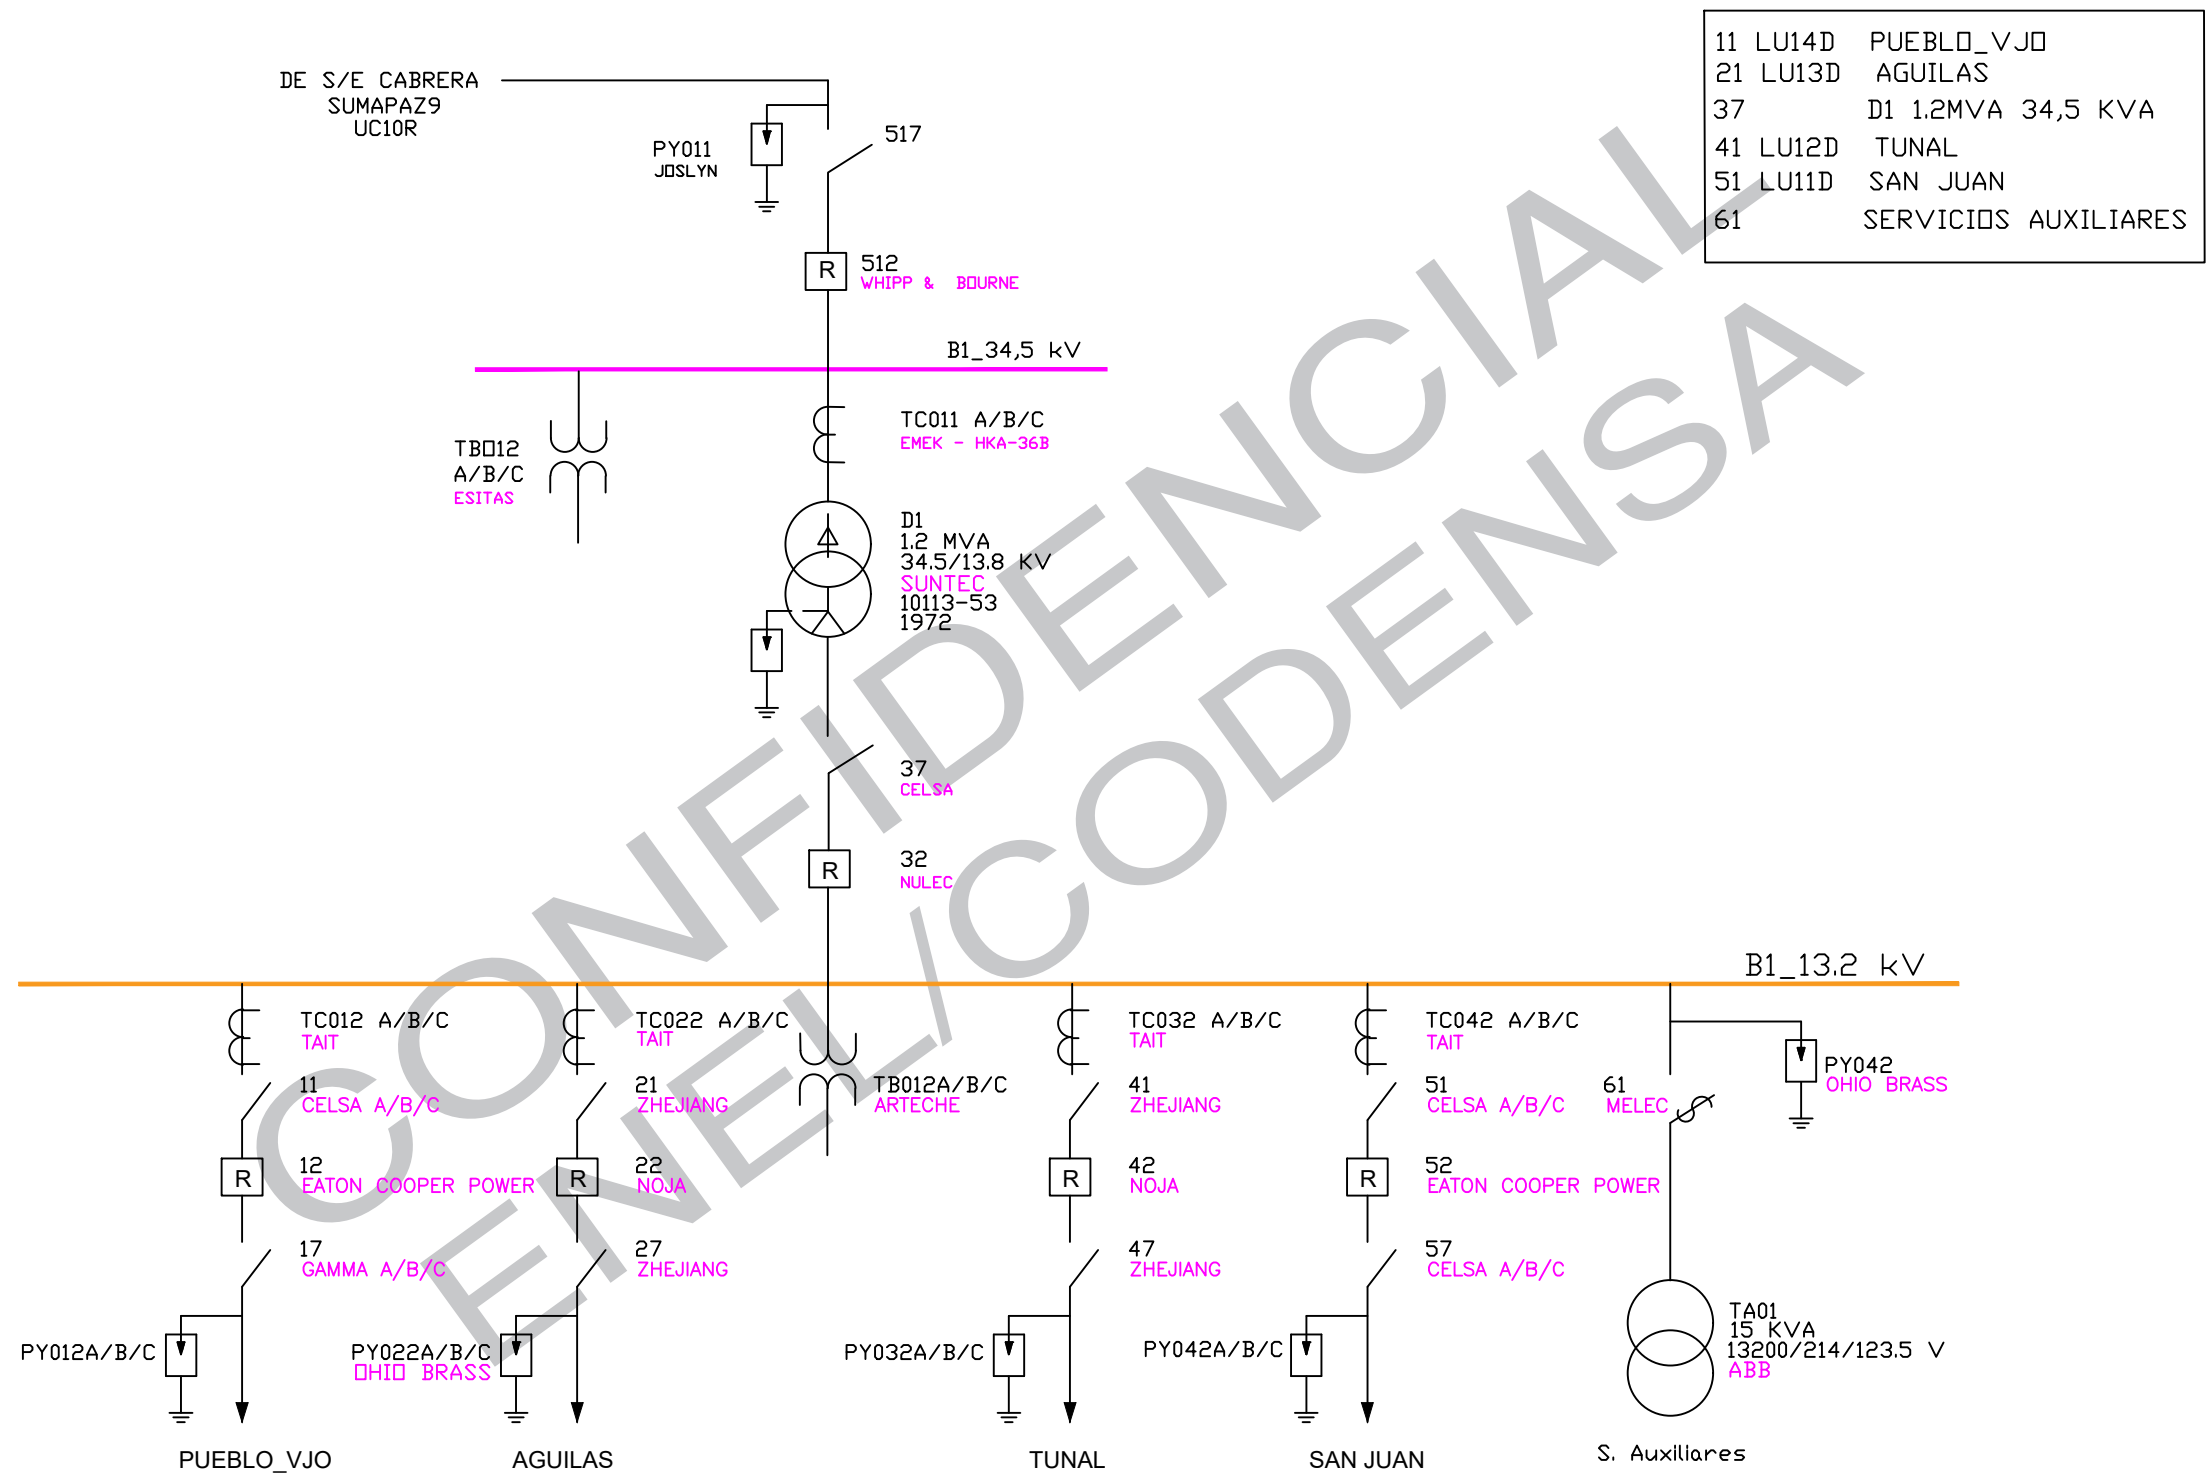

11	LU14D	PUEBLO_VJO
21	LU13D	AGUILAS
37		D1 1.2MVA 34,5 KVA
41	LU12D	TUNAL
51	LU11D	SAN JUAN
61		SERVICIOS AUXILIARES



Unidad Organizativa
Administración Información
Técnica Col

REVISION No. 12

FECHA: DICIEMBRE/2021

ARCHIVO: LA UNIÓN.DWG
C:\ESQUEMAS SUBESTACIONES\ESQUEMAS DEFINITIVOS

DIAGRAMA UNIFILAR

SUBESTACION LA UNION

Municipio de la union a 80km de Usme carretera
hacia municipio la Cabrera

CODIGO: LU

84

HOJA: 1

DE: 1