


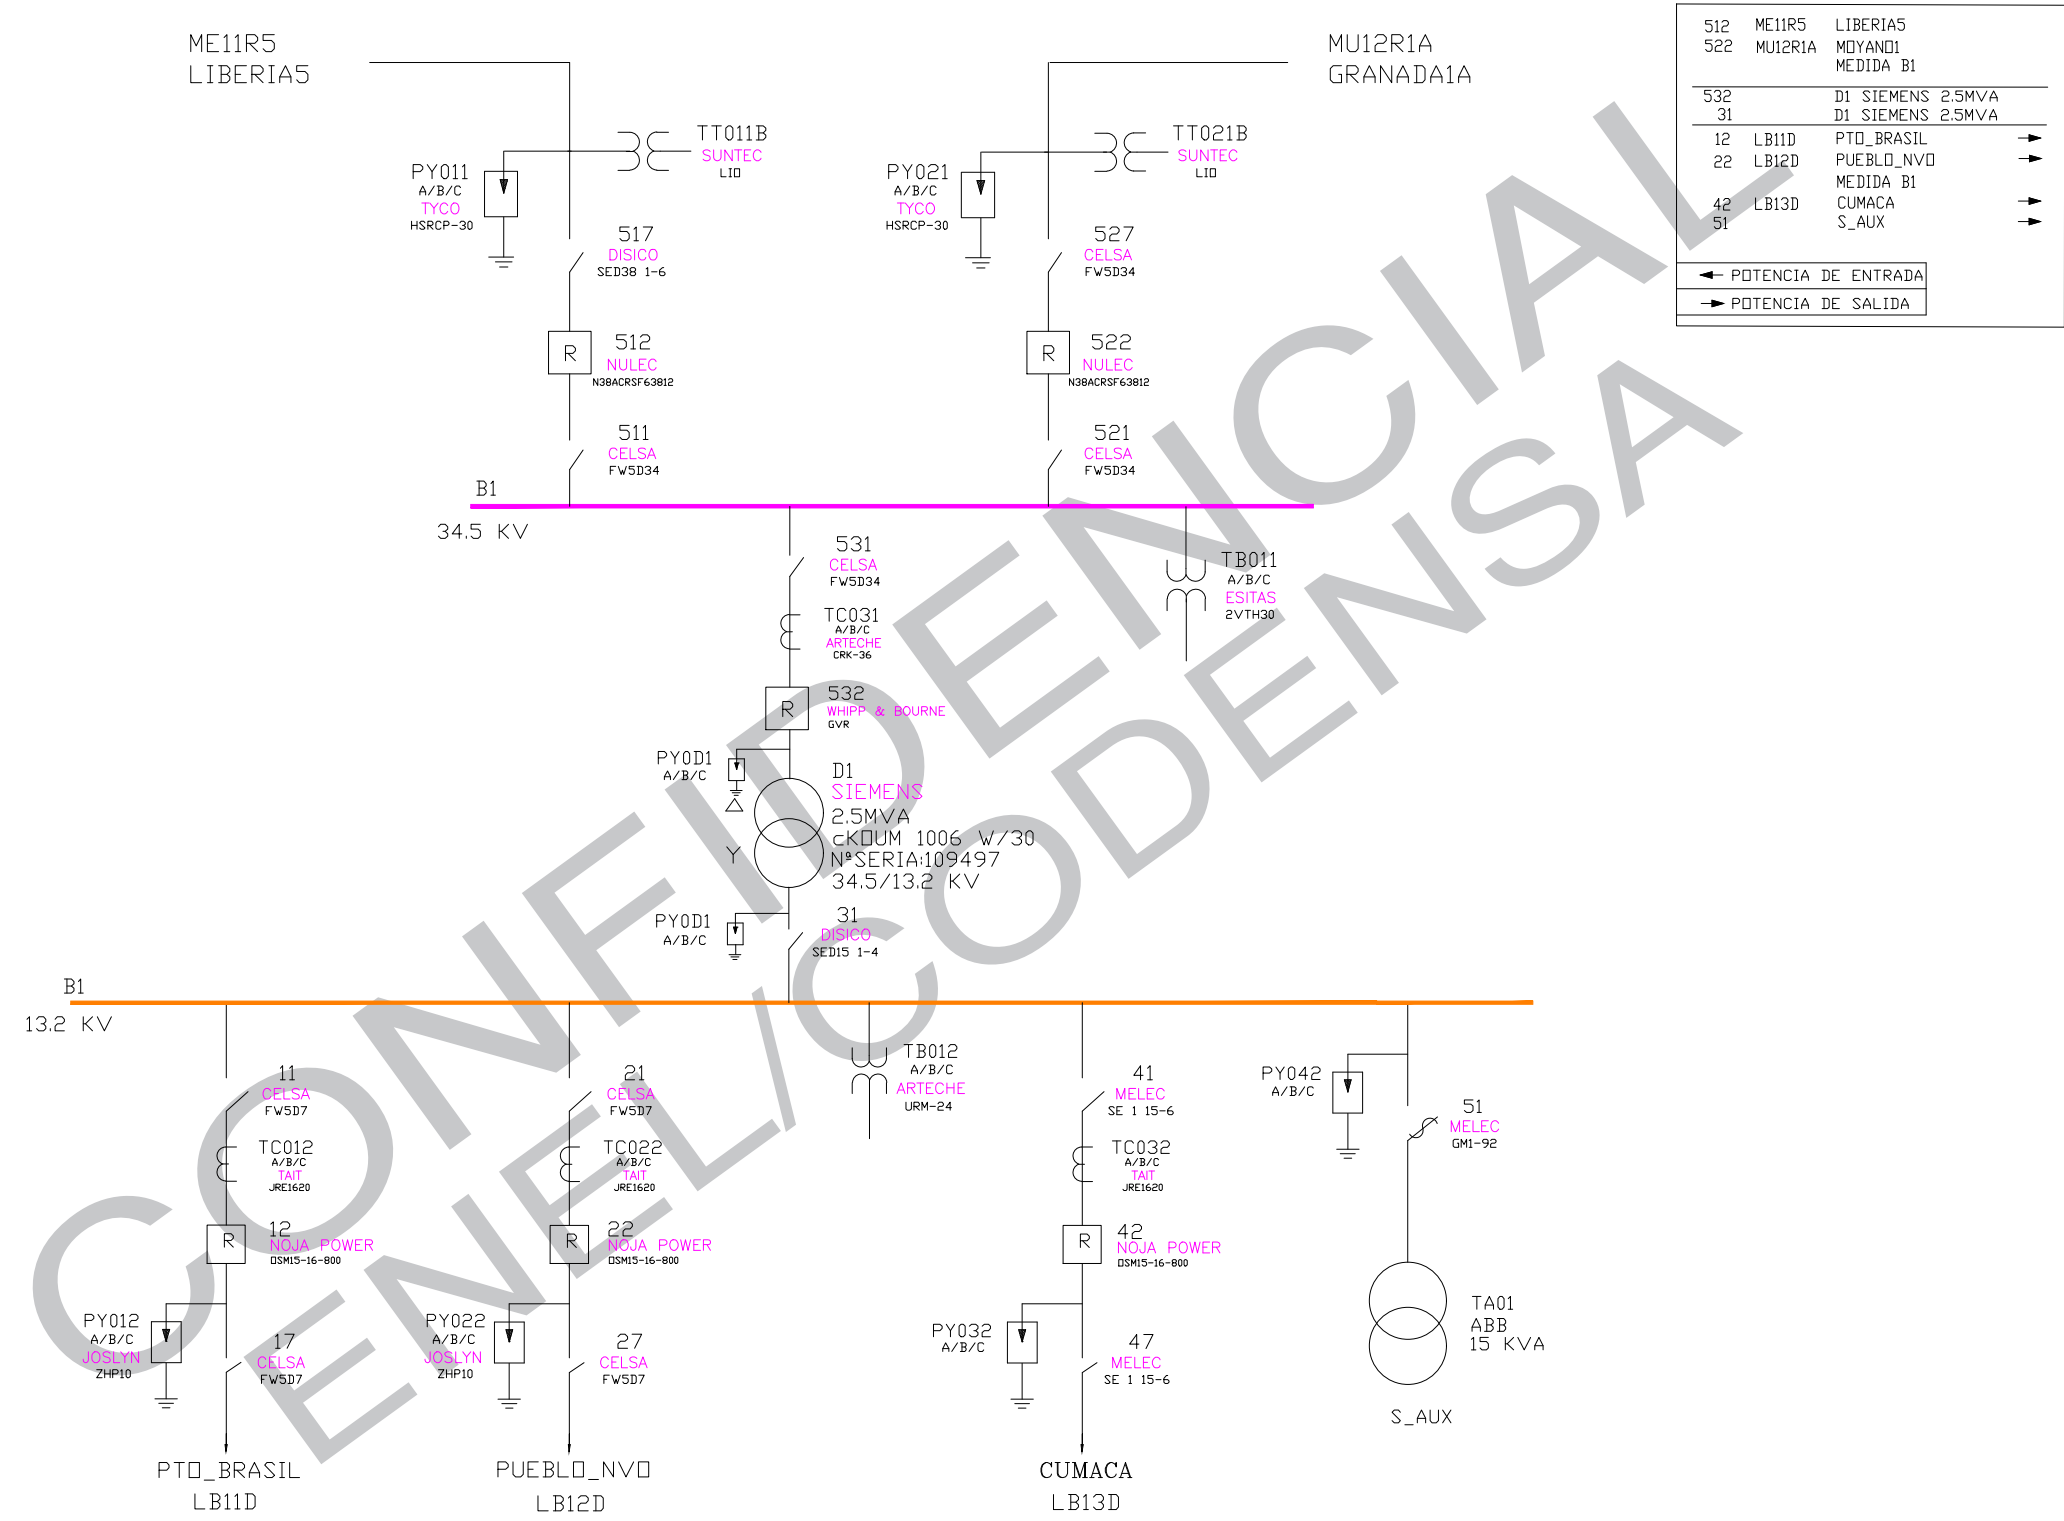

512	ME11R5	LIBERIA5
522	MU12R1A	MOYANDI
		MEDIDA B1
532		D1 SIEMENS 2.5MVA
31		D1 SIEMENS 2.5MVA
12	LB11D	PTO_BRASIL
22	LB12D	PUEBLO_NVO
		MEDIDA B1
42	LB13D	CUMACA
51		S_AUX

← POTENCIA DE ENTRADA
→ POTENCIA DE SALIDA



Unidad Organizativa
Administración Información
Técnica Col.

REVISION No.	17
FECHA:	MARZO/2022
ARCHIVO:	LIBERIA.DWG \\COLCOD09FS01\FileServer\CONTROL UNIFILARES

DIAGRAMA UNIFILAR
SUBESTACION MT/MT Z.R. MUNICIPIO DE VIOTA VDA. LIBERIA
CODIGO: LB

86
HOJA: 1
DE: 1