


MAGDALENA1

11	MA_SUAX_1	C01
22	MAGDALENA2	C02
32	MAGDALENA3	C03
42	MAGDALENA4	C04
52	MAGDALENA1	C05

← POTENCIA DE ENTRADA
→ POTENCIA DE SALIDA

CELDAS COLGIOVANNY

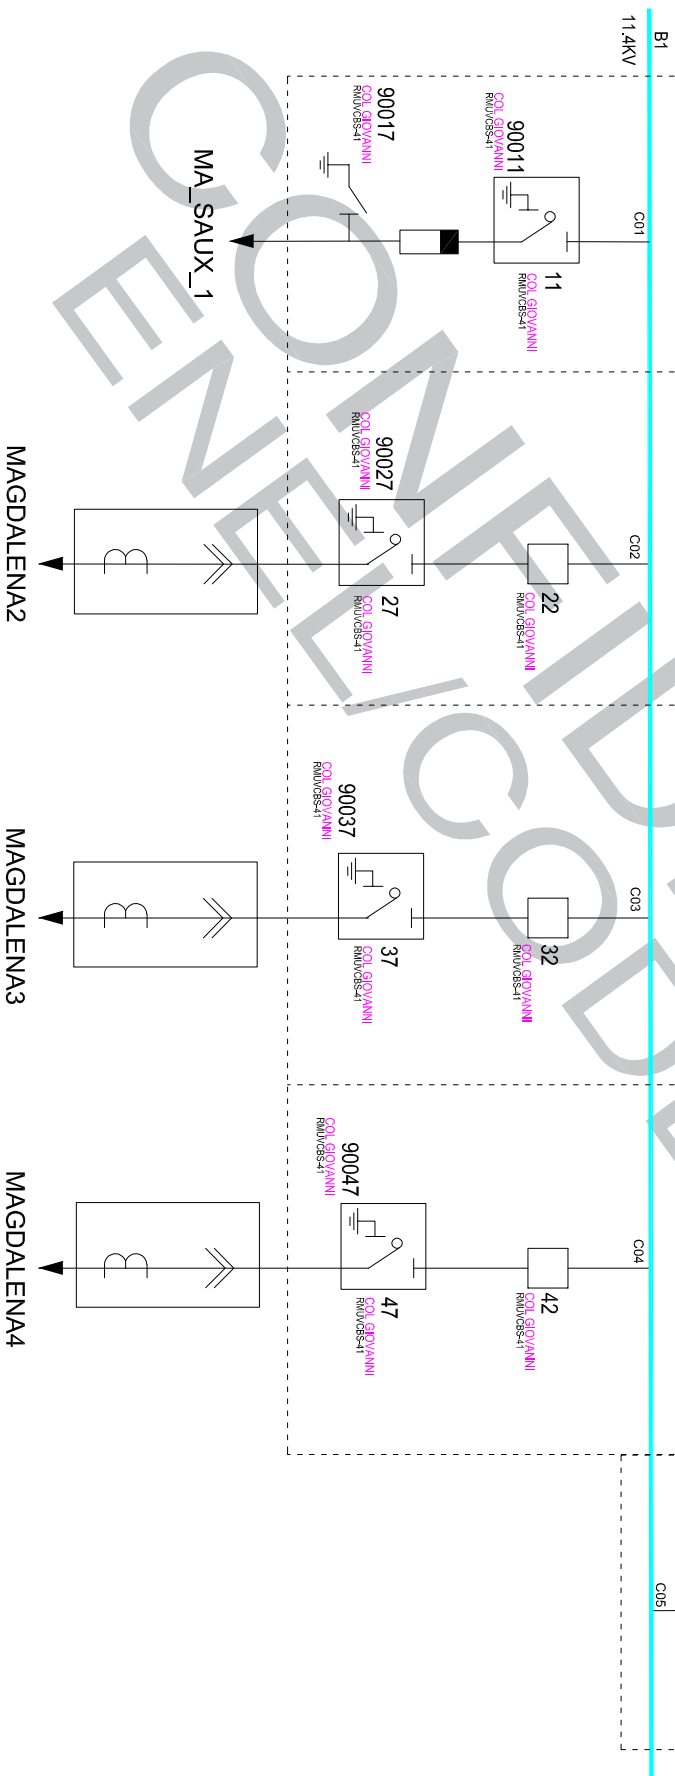

codensa

Unidad Organizativa
Administración Informática
Técnica Col.

REVISION No. 2

FECHA: OCTUBRE/2022

ARCHIVO: MAGDALENA.DWG
Y:\FileServer\CONTROL UNIFILARES\UNIFILARES_ABRIL_2020

DIAGRAMA UNIFILAR

SUBESTACIÓN SATELITE MAGDALENA

DG 40 A BIS NO 15 - 78

CODIGO: MA

144

HOUA: 1

DE: 1