



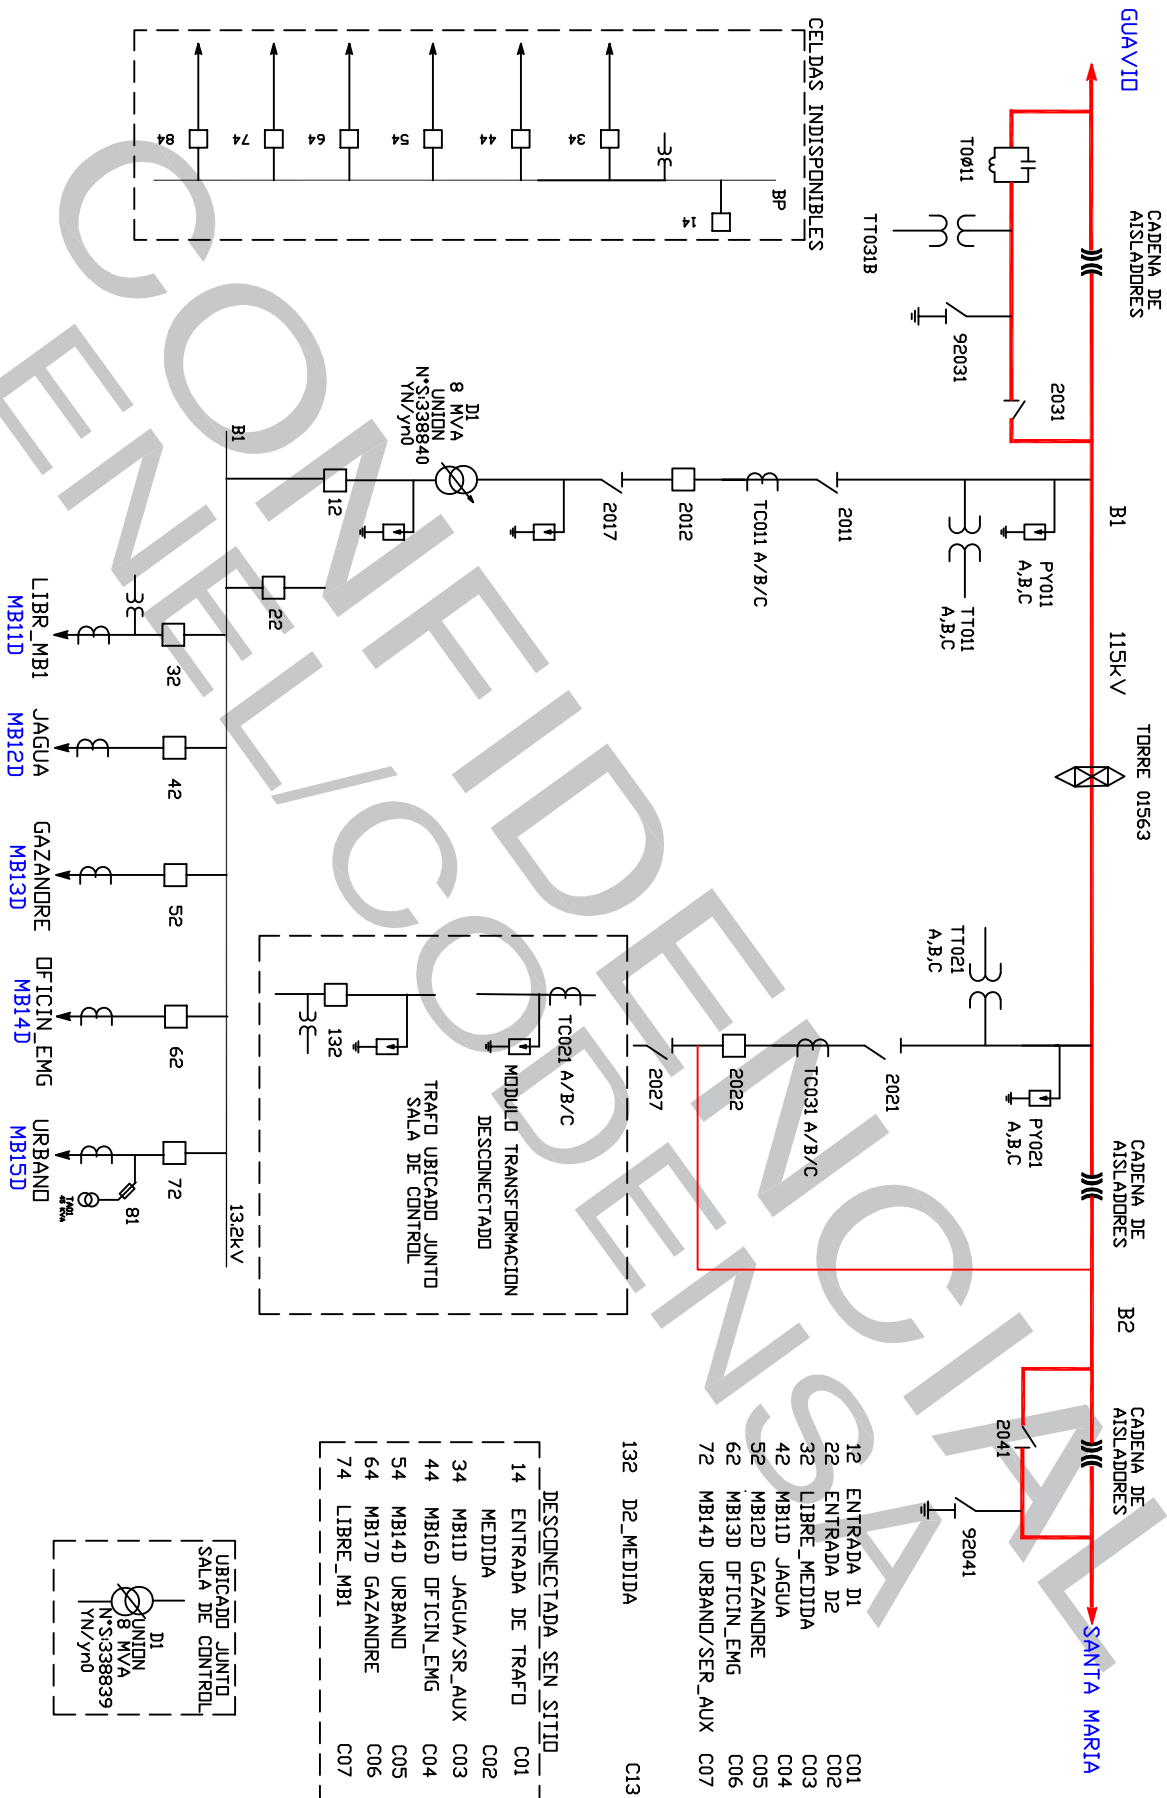

DESCONECTADA SEN SITIO		
14	ENTRADA DE TRAFD	C01
	MEDIDA	C02
34	MB11D JAGUA/SR_AUX	C03
44	MB16D OFICIN_EMG	C04
54	MB14D URBAND	C05
64	MB17D GAZANDRE	C06
74	LIBRE_MB1	C07

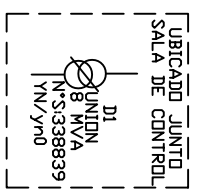

Unidad Organizativa

Administración Informativa

Técnica Col.

REVISION No.

11

FECHA:

NOVIEMBRE/2018

ARCHIVO:

MAMBITA.DWG

21\Volc0000901\Fisicaweb\CONTROL_LINIALES\UNIDADES_Noviembre_2018

DIAGRAMA UNIFILAR

SUBESTACION MAMBITA

AREA ALQAMIENTOS EMWESA

SIEMENS 6615

CODIGO:

MB

DE:

1

27