
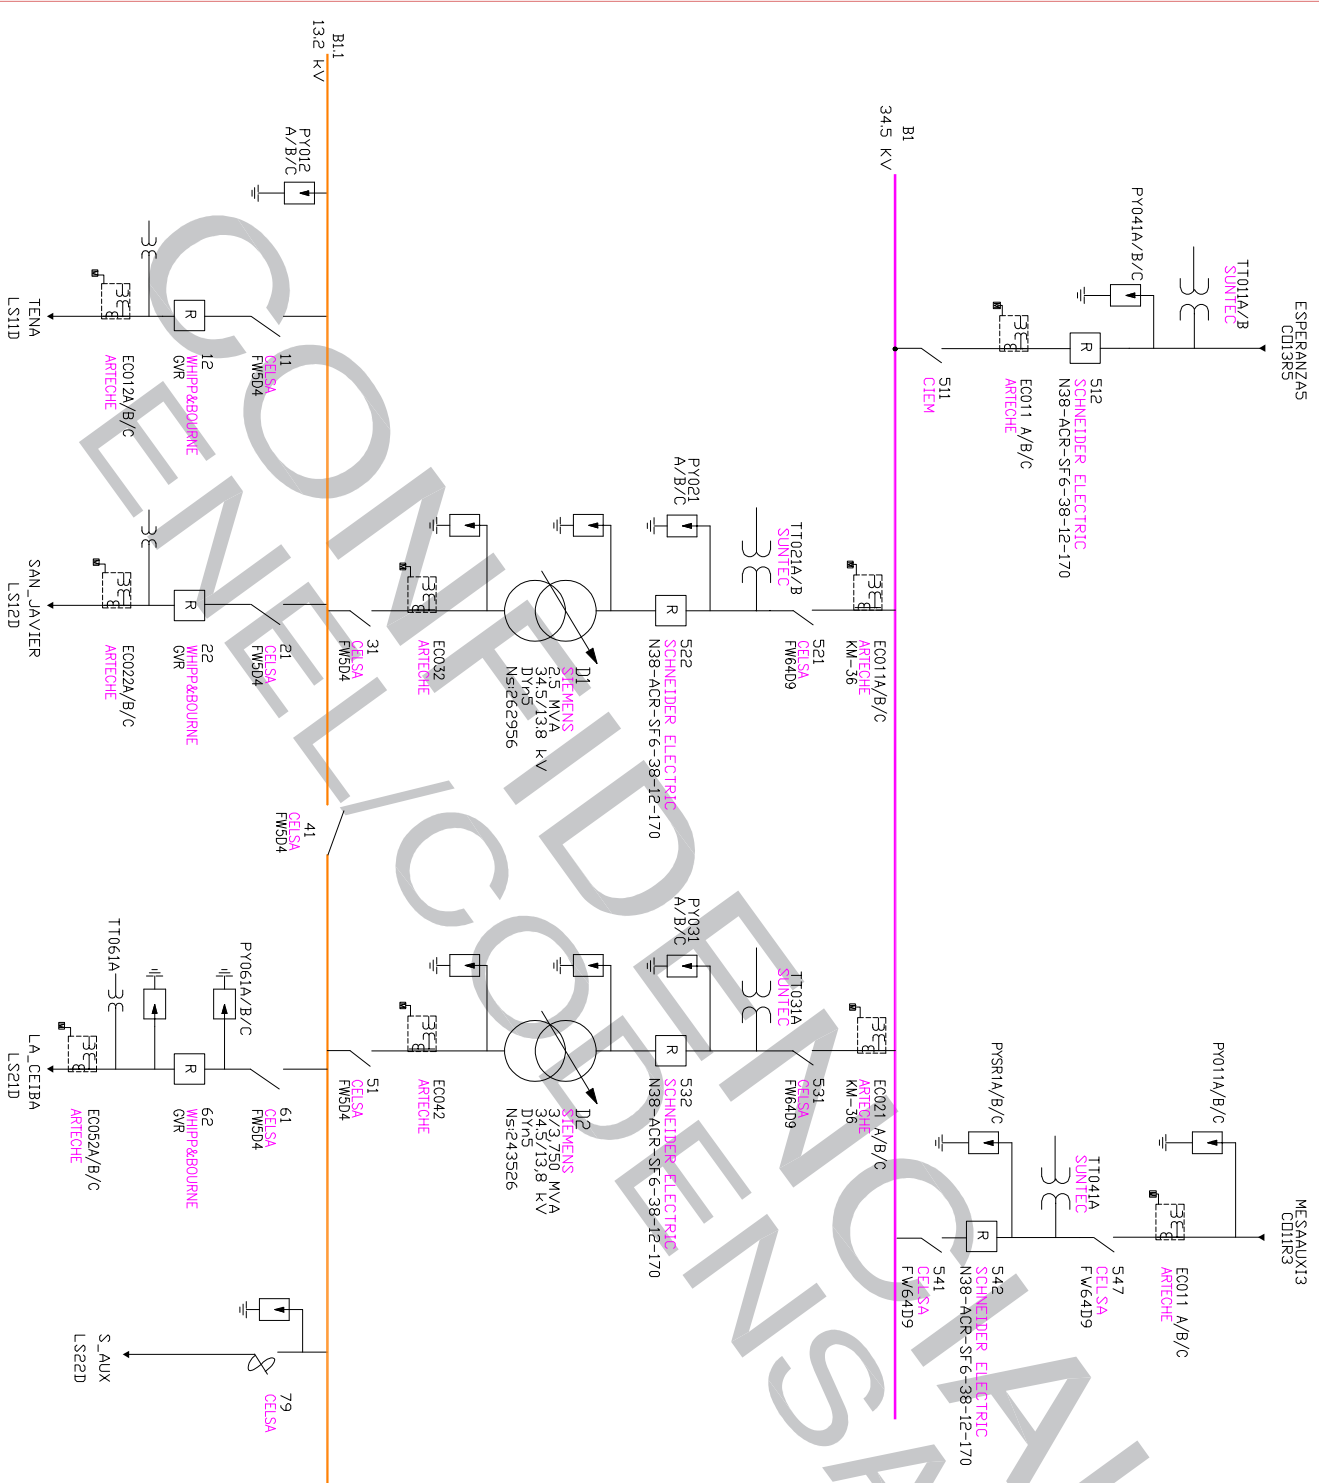
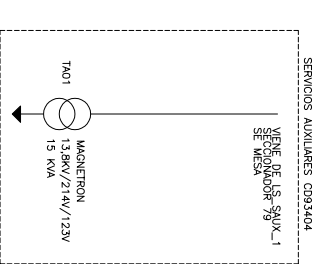


512	CDI3R5	ESPERANZAS	→
522	DI	SIEMENS 2,5 MVA	→
532	D2	SIEMENS 3,75 MVA	→
542	CDIIR3	MESAUXI3	→
12	LS1D	TENA	→
22	LS2D	SAN_JAVIER	→
31		UB BI1-BI2	→
41		D2 SIEMENS 2,5 MVA	→
51		UB BI1-BI2	→
62	LS2D	LA CEIBA	→
79	LS2D	LS SAUX.1	→

→ POTENCIA ENTRADA → POTENCIA SALIDA

12411701

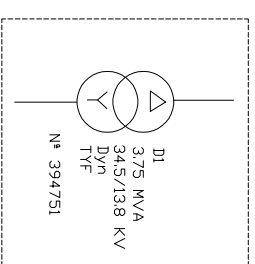

Unidad Organizativa
Administración Informacion
Tecnica Col

REVISION No.	6	DIAGRAMA UNIFILAR	632
FECHA:	ENERO/2022	SUBESTACION MESA	HOJA: 1
ARCHIVO:	MESA.DWG	MUNICIPIO DE LA MESA	DE: 1
Y:\FileServer\CONTROL UNIFILARES\UNIFILARES_MARZO_2019		CODIGO:	LS