


12	MO11 ACUATICO	C01
22	MO12 BOJACA	C02
32	MO13 TORO	C03
42	MO14 MALJORCA	C04
52	MO15 PROSPERIDA	C05
62	D1 AB8 35MVA	C06
72	MO16 SUNSET	C07
82	MO17 URBANIZAC	C08
92	MO18 TIBATITA	C09
102	MO19 MO SAUX_1	C10
112	MEDIA B1.1	C11
122	U.B. B1.1-B1.2	C12
132	MEDIA B1.2	C13
142	MO21 PLASTHOGAR	C14
152	MO22 FLORAMERICA	C15
162	MO23 PO EIOERGE (FUTURO)	C16
172	MO24 STA MARIA	C17
182	D2 SIEMENS 30/35/40 MVA	C18
192	MO25 SAN ANDRES	C19
202	MO26 MADRID	C20
212	MO27 SERREZUELA	C21
222	MO28 MO AUX 2	C22
232	MO29 BELIZCA	C23
242	U.B. B1.3-B1.2	C24
252	MO31 PUENTES	C25
262	MO32 BELVERDE	C26
272	MO33 FUNZA	C27
282	MO34 VILLA PAUL	C28
292	MO35 GUATEMALA	C29
302	D3 SIEMENS 30/35/40MVA	C30
312	MEDIA B1.3	C31
322	U.B. B1.3-B1.4	C32
332	MEDIA B1.4	C33
342	D3 SIEMENS 30/35/40MVA	C34
352	MO36 ZUAME	C35
362	MO37 CL_TERCERA	C36
372	MO38 MARTINS	C37
382	MO39 ITALCOL	C38
392	MO3A LA HERRERA	C39
402	U.B B1.4-B1.1	C40

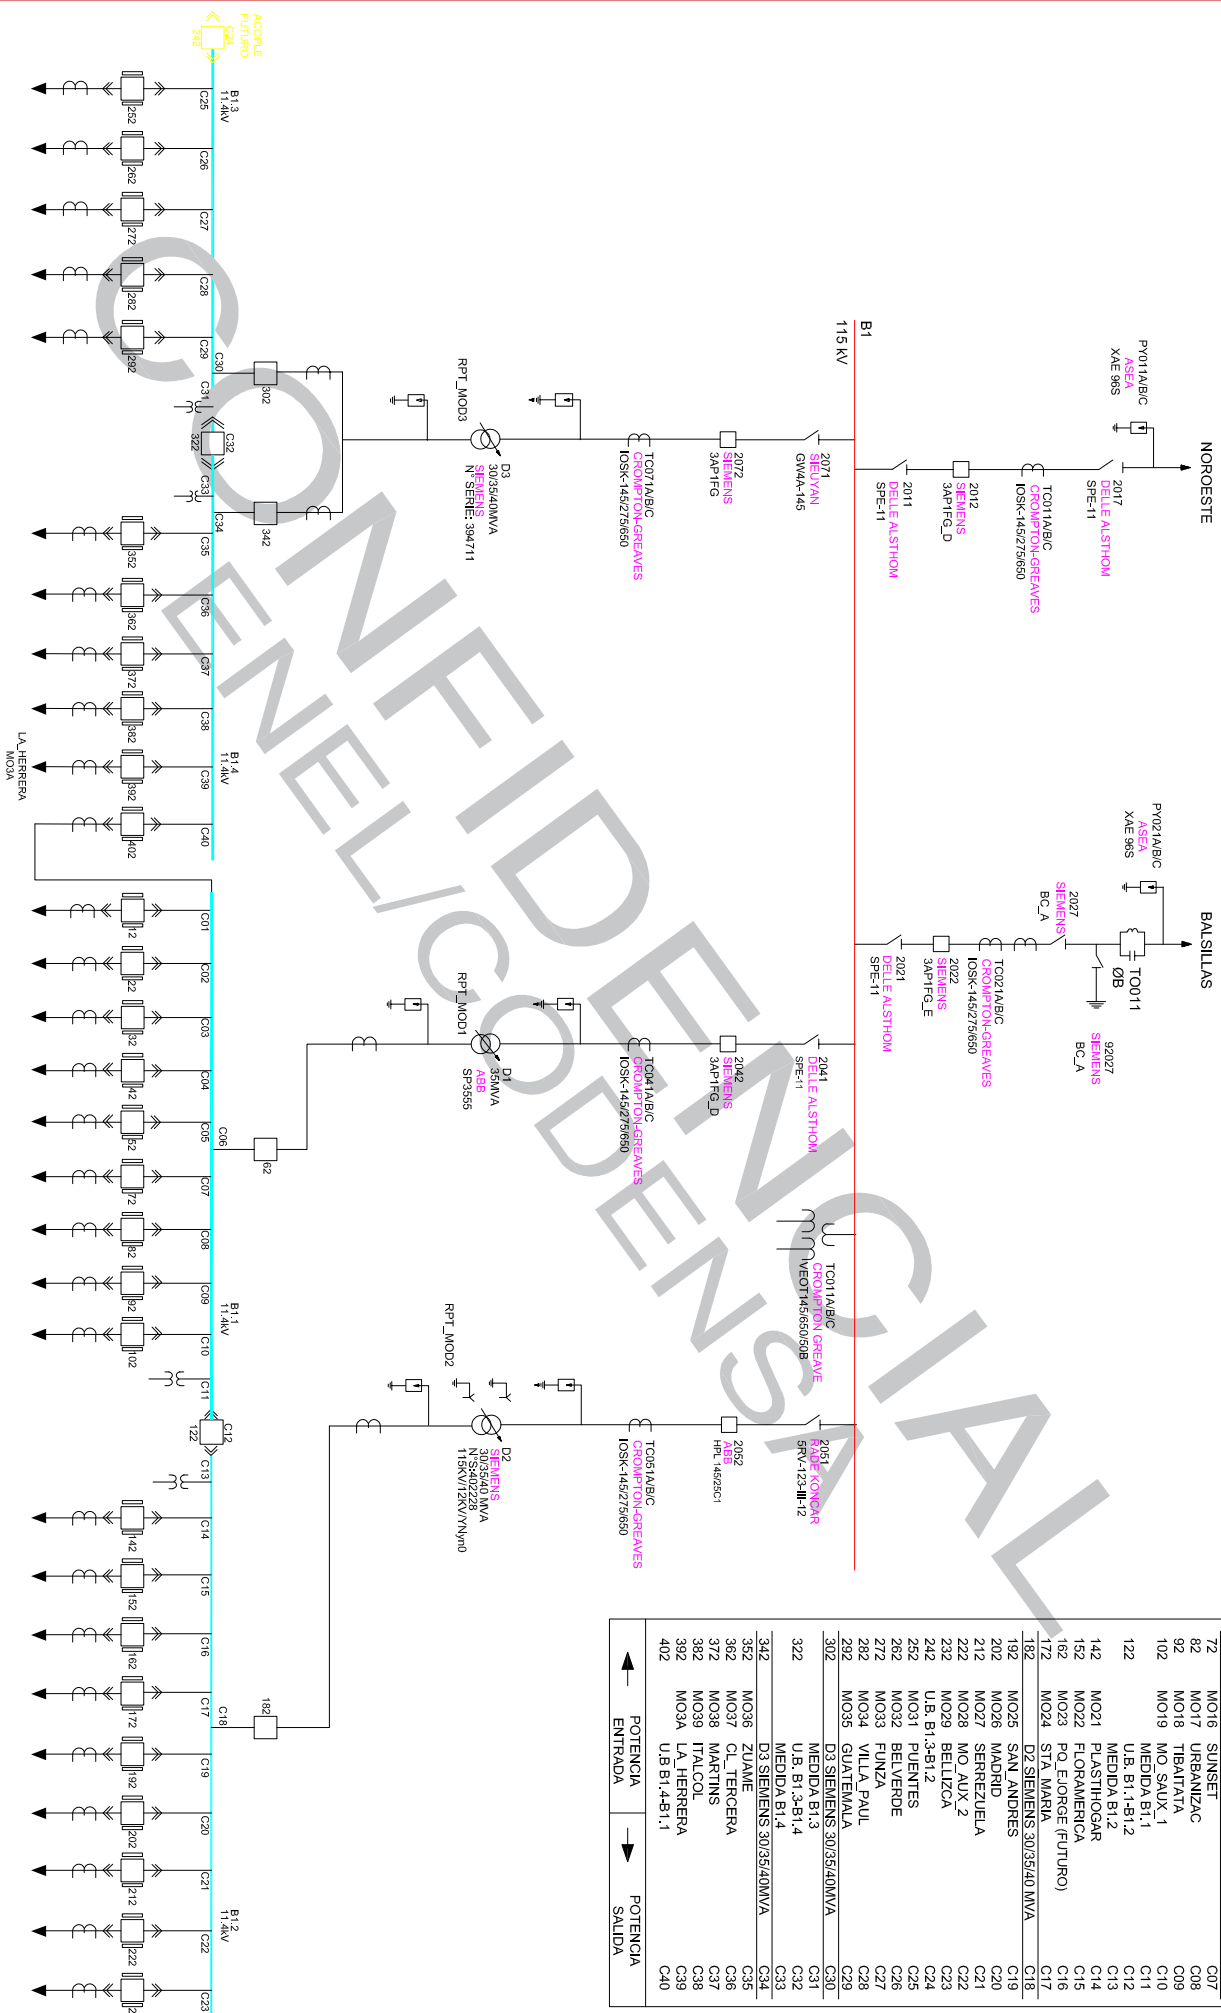

Unidad Organizativa
Administración Informacion
Técnica Col.

REVISION No.

40

DIAGRAMA UNIFILAR

29

FECHA:

NOVIEMBRE/2022

MOSQUERA

TEL :8276158, SIEMENS 6552

CARRETERA OCC. KM 18.5 VIA FACATATIVA

HOJA:

1

ARCHIVO:

MOSQUERA.DWG

Y:\FileServer\CONTROL_UNIFILARES\MAEZO_2020

CODIGO:

MO

DE:

2