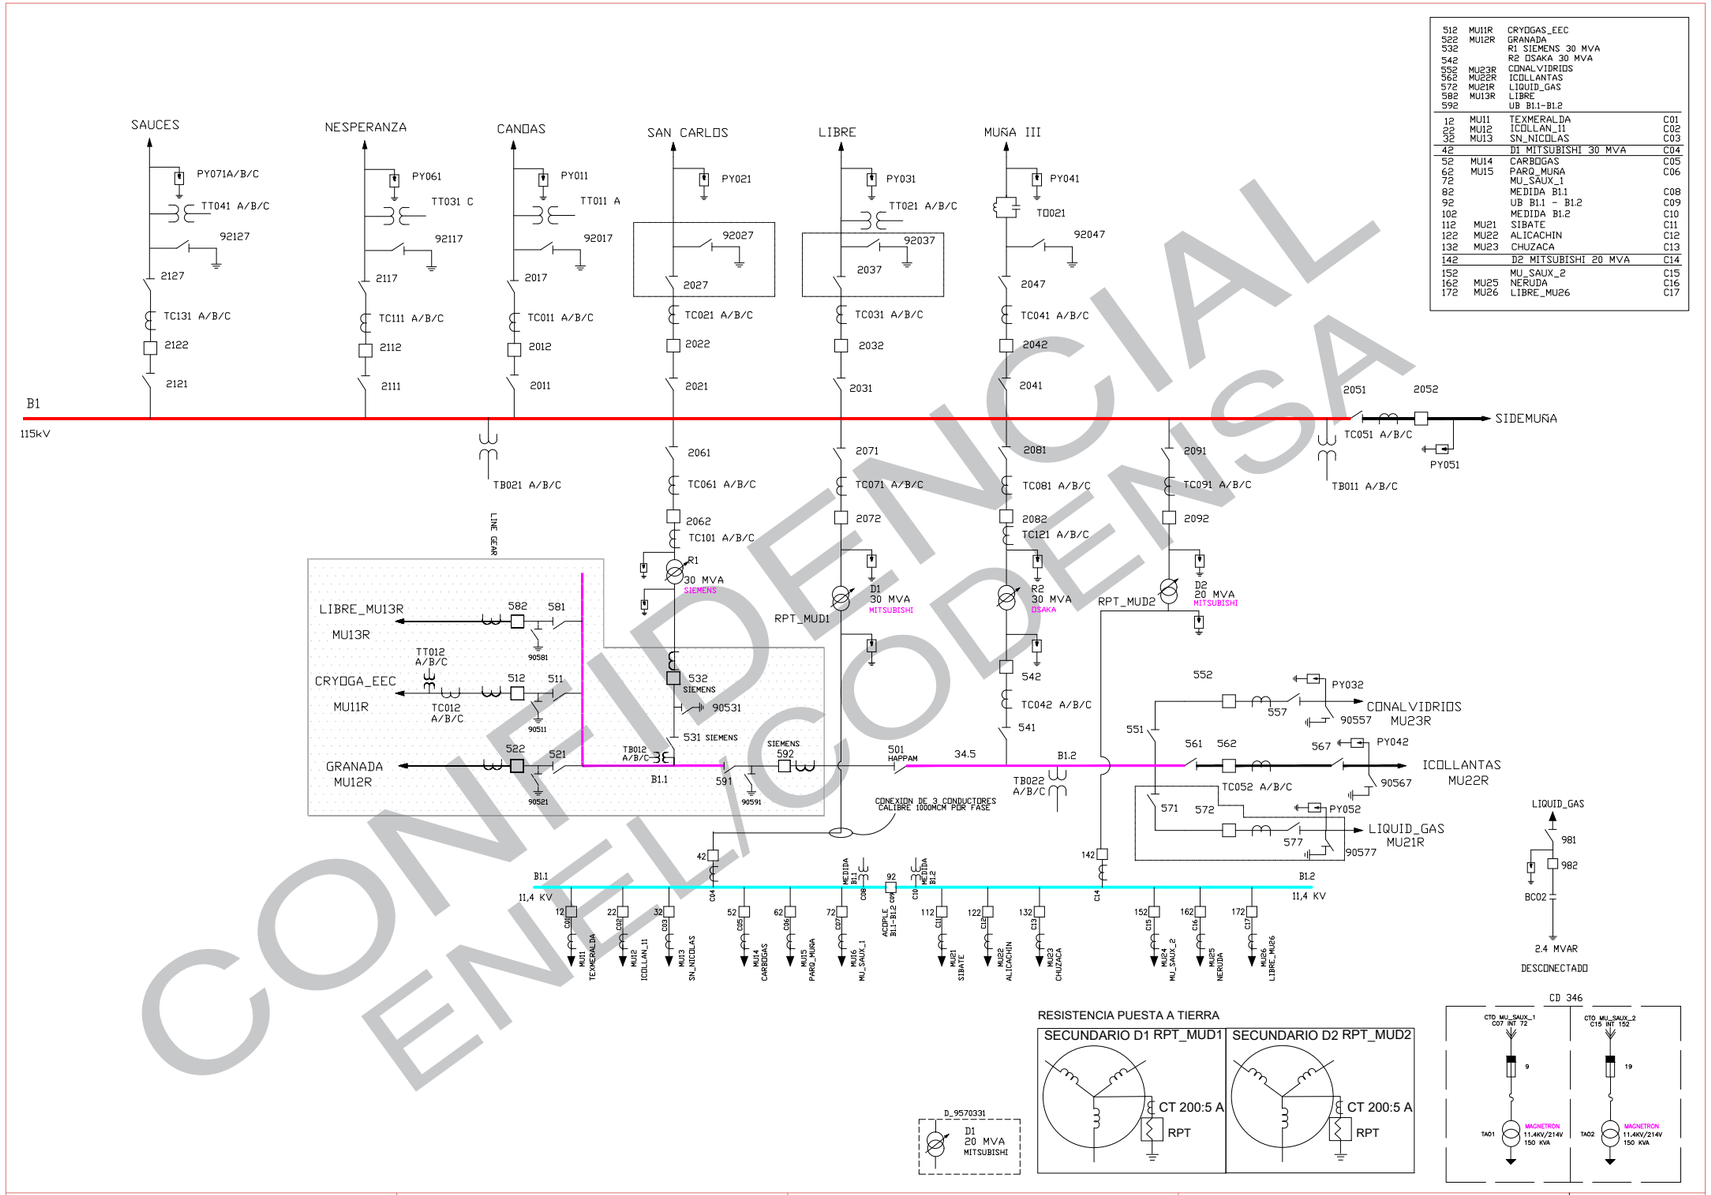

CONFIDENCIAL
ENEL CODENSA

512	MU11R	CRYOGAS_EEC
522	MU12R	GRANADA
532		R1 SIEMENS 30 MVA
542		R2 DSAKA 30 MVA
552	MU23R	CONALVIDRIOS
562	MU22R	ICOLLANTAS
572	MU21R	LIQUID_GAS
582	MU13R	LIBRE
592		UB B1.1-B1.2
12	MU11	TEXMERALDA C01
22	MU12	ICOLLAN_11 C02
32	MU13	SN_NICOLAS C03
42		D1 MITSUBISHI 30 MVA C04
52	MU14	CARBOGAS C05
62	MU15	PARQ_MUÑA C06
72		MU_SAUX_1
82		MEDIDA B1.1 C08
92		UB B1.1 - B1.2 C09
102		MEDIDA B1.2 C10
112	MU21	SIBATE C11
122	MU22	ALICACHIN C12
132	MU23	CHUZACA C13
142		D2 MITSUBISHI 20 MVA C14
152		MU_SAUX_2 C15
162	MU25	NERUDA C16
172	MU26	LIBRE_MU26 C17

enel codensa	Unidad Organizativa Administración Información Técnica Col.	REVISION No. 30 FECHA: FEBRERO/2022 ARCHIVO: MUÑA.DWG \\COLCOD09FS01\FileServer\CONTROL UNIFILARES	DIAGRAMA UNIFILAR SUBESTACION MUÑA TEL. 7198855 SIEMENS 6554 ZONA INDUSTRIAL MUÑA CODIGO: MU	30 HOJA: 1 DE: 1