


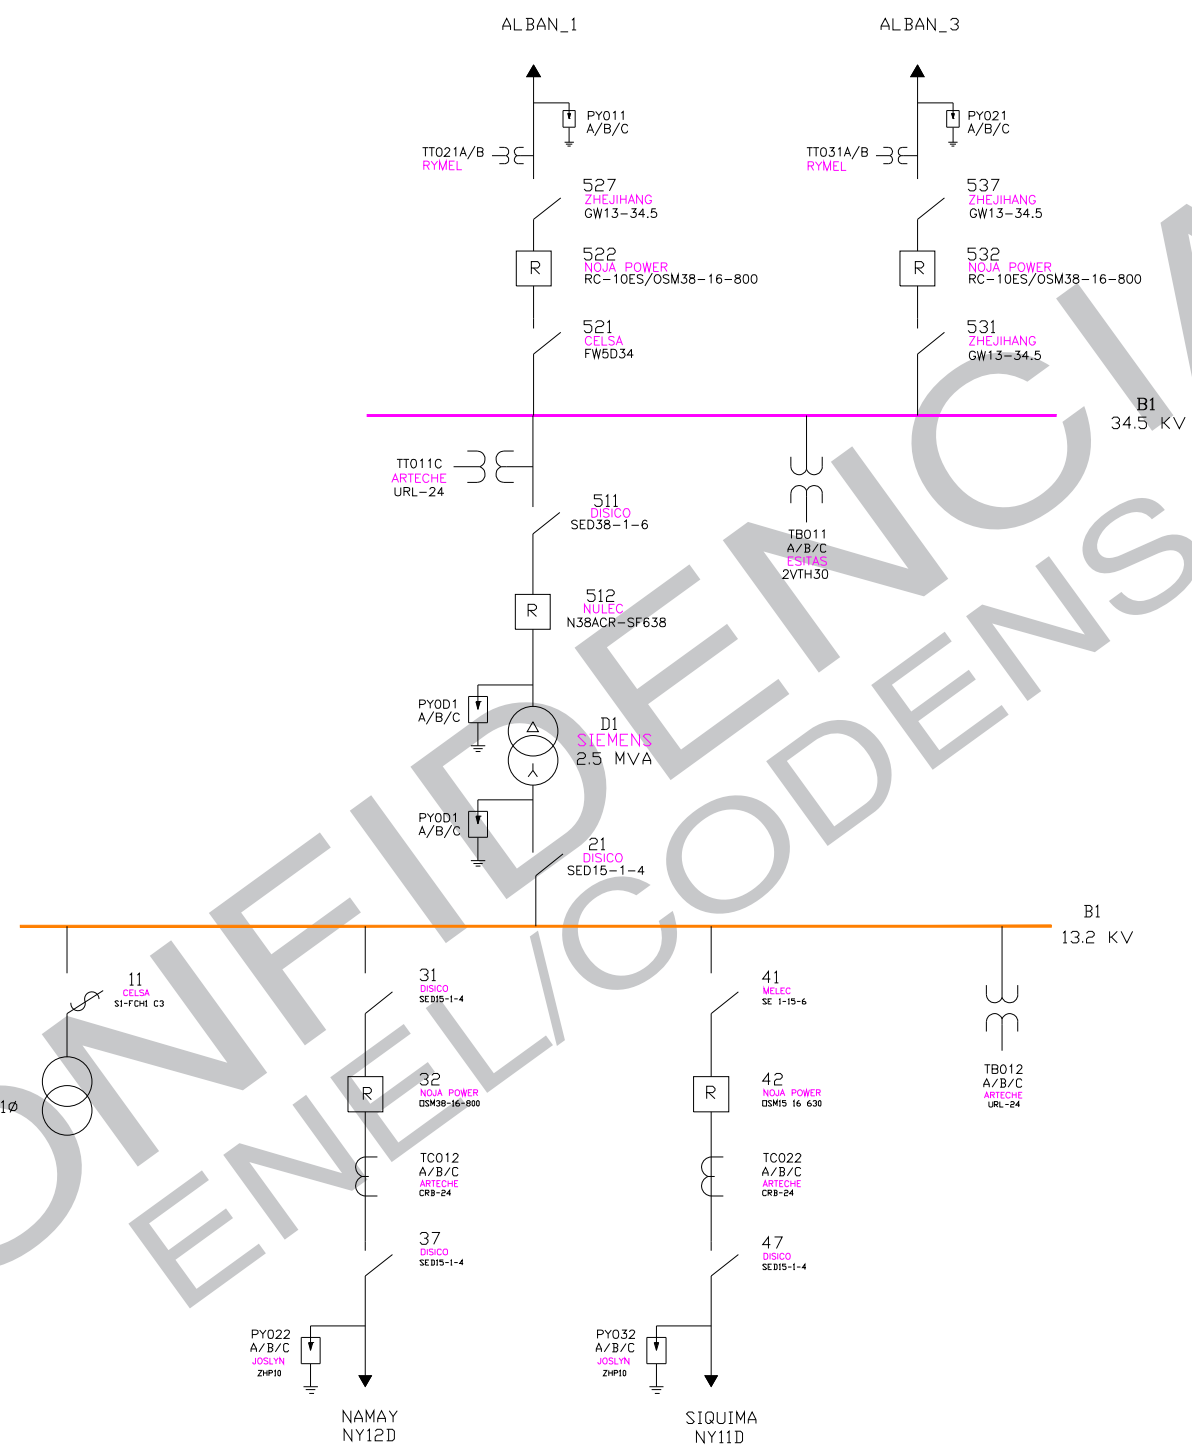

11	S_AUX1
21	D1 SIEMENS 2.5 MVA
32	NAMAY NY12D
42	SIQUIMA NY11D



Unidad Organizativa
Administración Información
Técnica Col.

REVISION No.

12

FECHA:

ENERO/2022

ARCHIVO:

NAMAY.DWG

\\COLCOD09FS01\\FileServer\\CONTROL UNIFILARES

DIAGRAMA UNIFILAR

SUBSTACION NAMAY
VIA ALBAN GUAYABAL DE SIQUIMA
CACERIO CHIMBE

CODIGO:

NY

89

HOJA:

1

DE:

1