

512	UB13R	TAUSA	→
522	SQ12R	LA PLAYA	→
552		MEDIA B1	
532		D1 SIEMENS 7.5-10 MVA	
22		UB B1.1-B1.2	
12		MEDIA B1.1	
32		NM110 ZOCARE	→
52		NM120 CHECUA	→
61		UB B1.1-B1.2	
82		NM130 NM_Saux_1	→
542		NM14D KREATO	→
72		D2 SIEMENS 10 MVA	
		D2 SIEMENS 10 MVA	
		MEDIA B1.2	
42		NM210 LA PUERTA	→
92		NM220 LA RUIDOSA	→
102		NM230 ORATORIO	→
		POTENCIA DE ENTRADA	
		POTENCIA DE SALIDA	

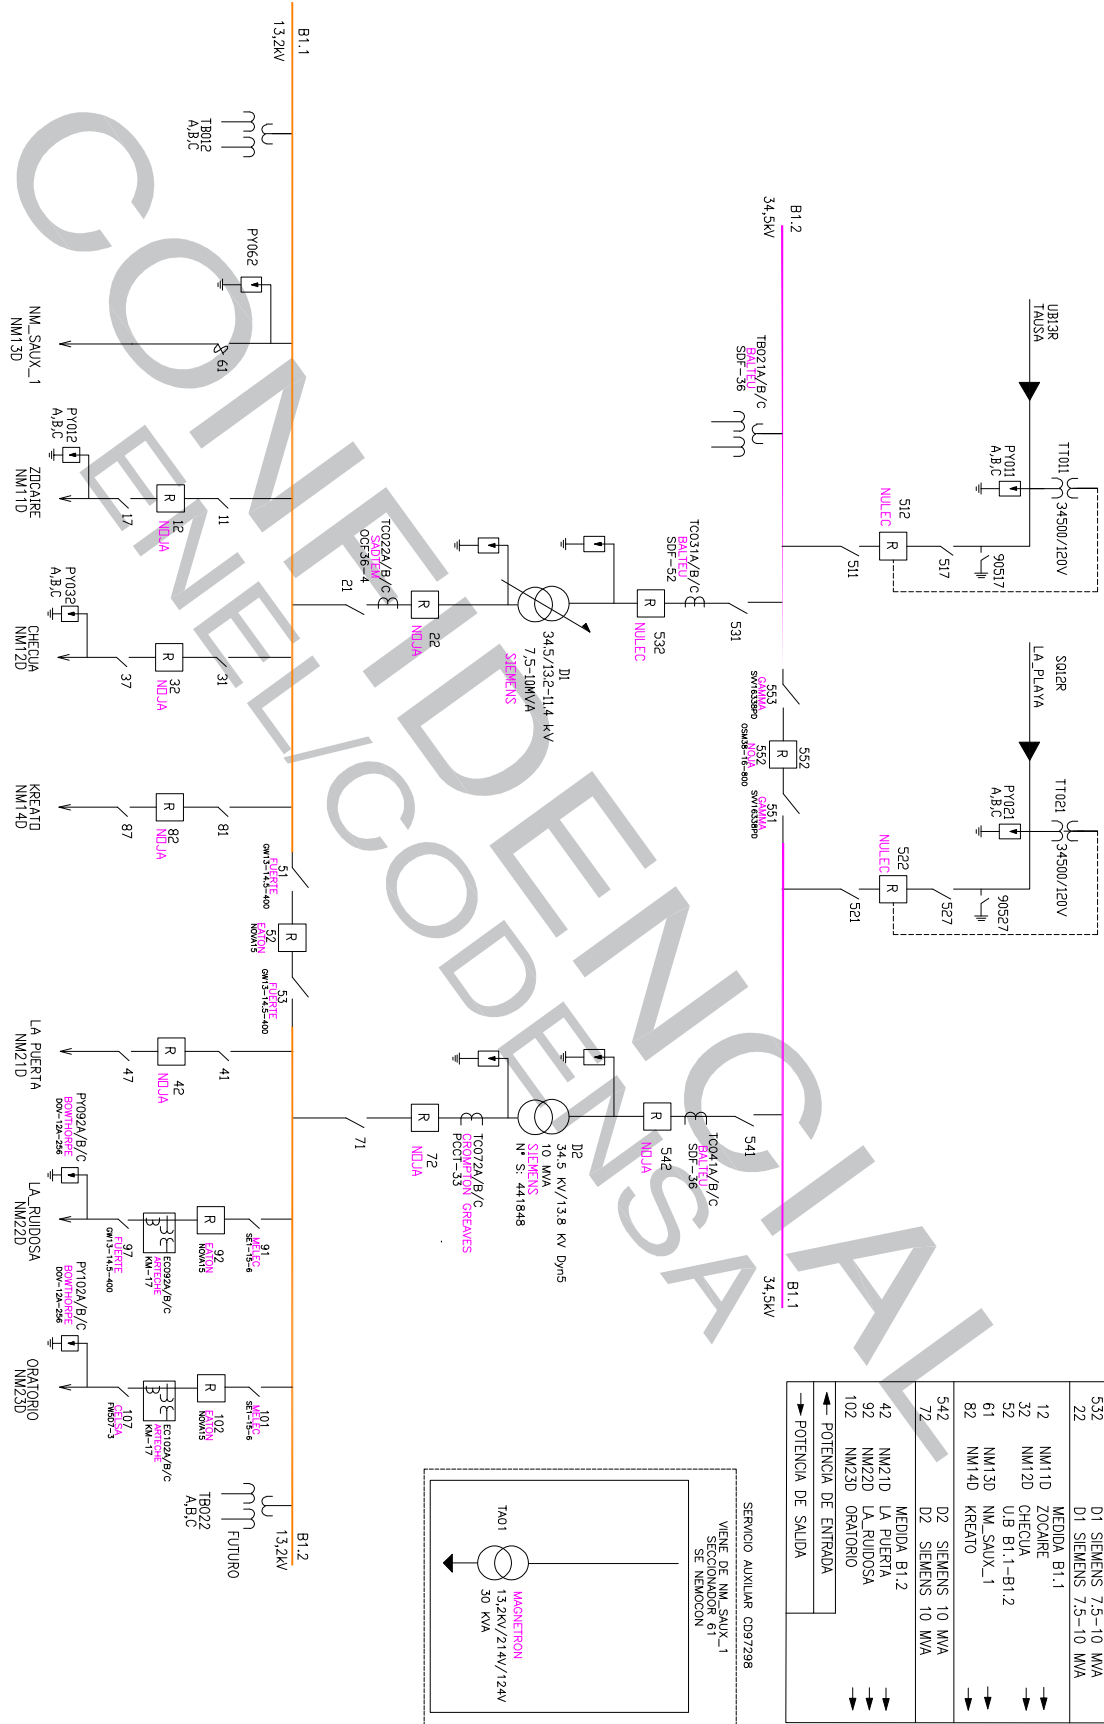


DIAGRAMA UNIFILAR

15

REVISION No.

FECHA:

JULIO/2022

SUBESTACION NEMOCON

MUNICIPIO DE NEMOCON

FRENTE AL ESTADIO MPAL CARRERA 6 JS 05

HOLA: 1

DE: 1

CODIGO: NM

ARCHIVO: NEMOCON.DWG

C:\ESQUEMAS SUBESTACIONES\ESQUEMAS DEFINITIVOS

Administración Informática

Técnica Col.



codensa