
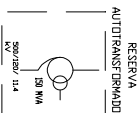


500 kV
B2

500 kV
B1

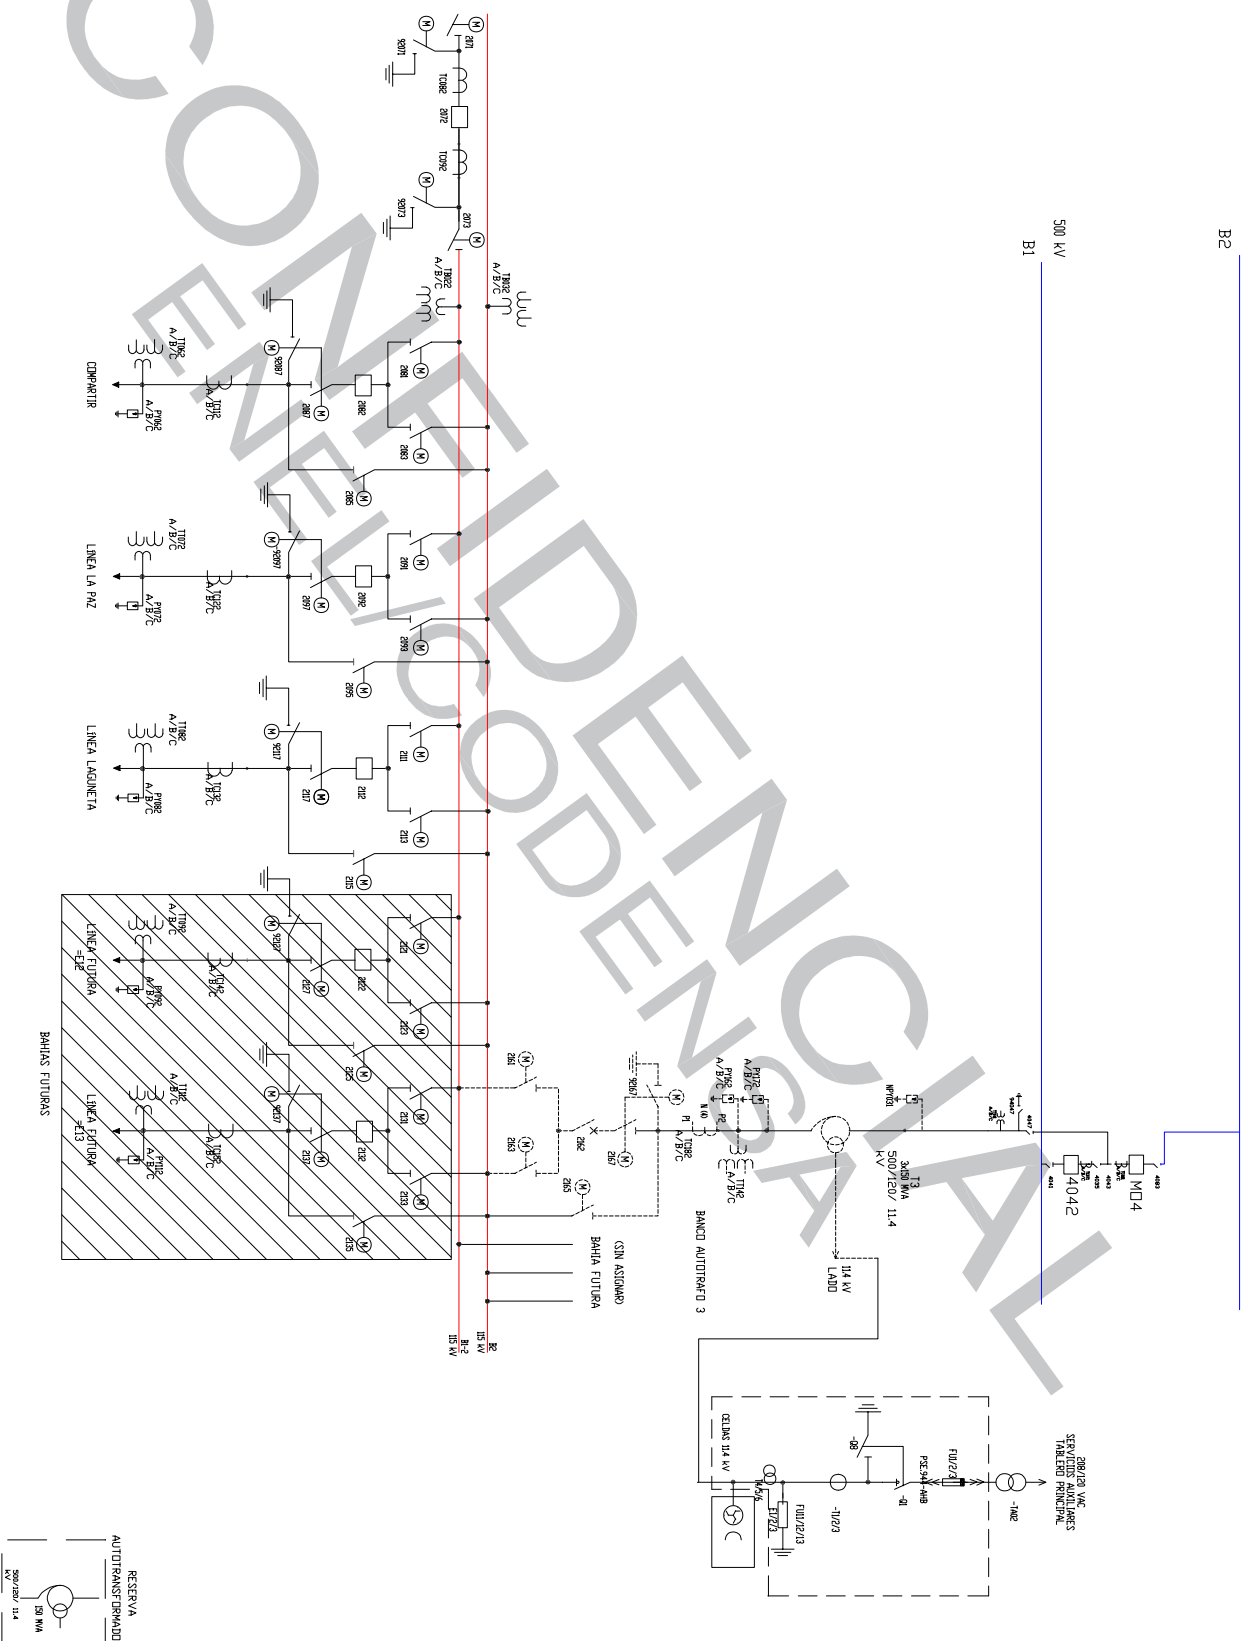

UNIDAD ORGANIZATIVA
ADMINISTRACION INFORMACION
TECNICA COL.

REVISION No.	3	DIAGRAMA UNIFILAR	178
FECHA:	DICIEMBRE/2022	SUBESTACION NESPERANZA	
ARCHIVO:	NESPERANZA_1.DWG	VIA CANOAS	
C:\ESQUEMAS SUBESTACIONES\ESQUEMAS DEFINITIVOS		NE	
CODIGO:			
HOJA:	2		
DE:	2		