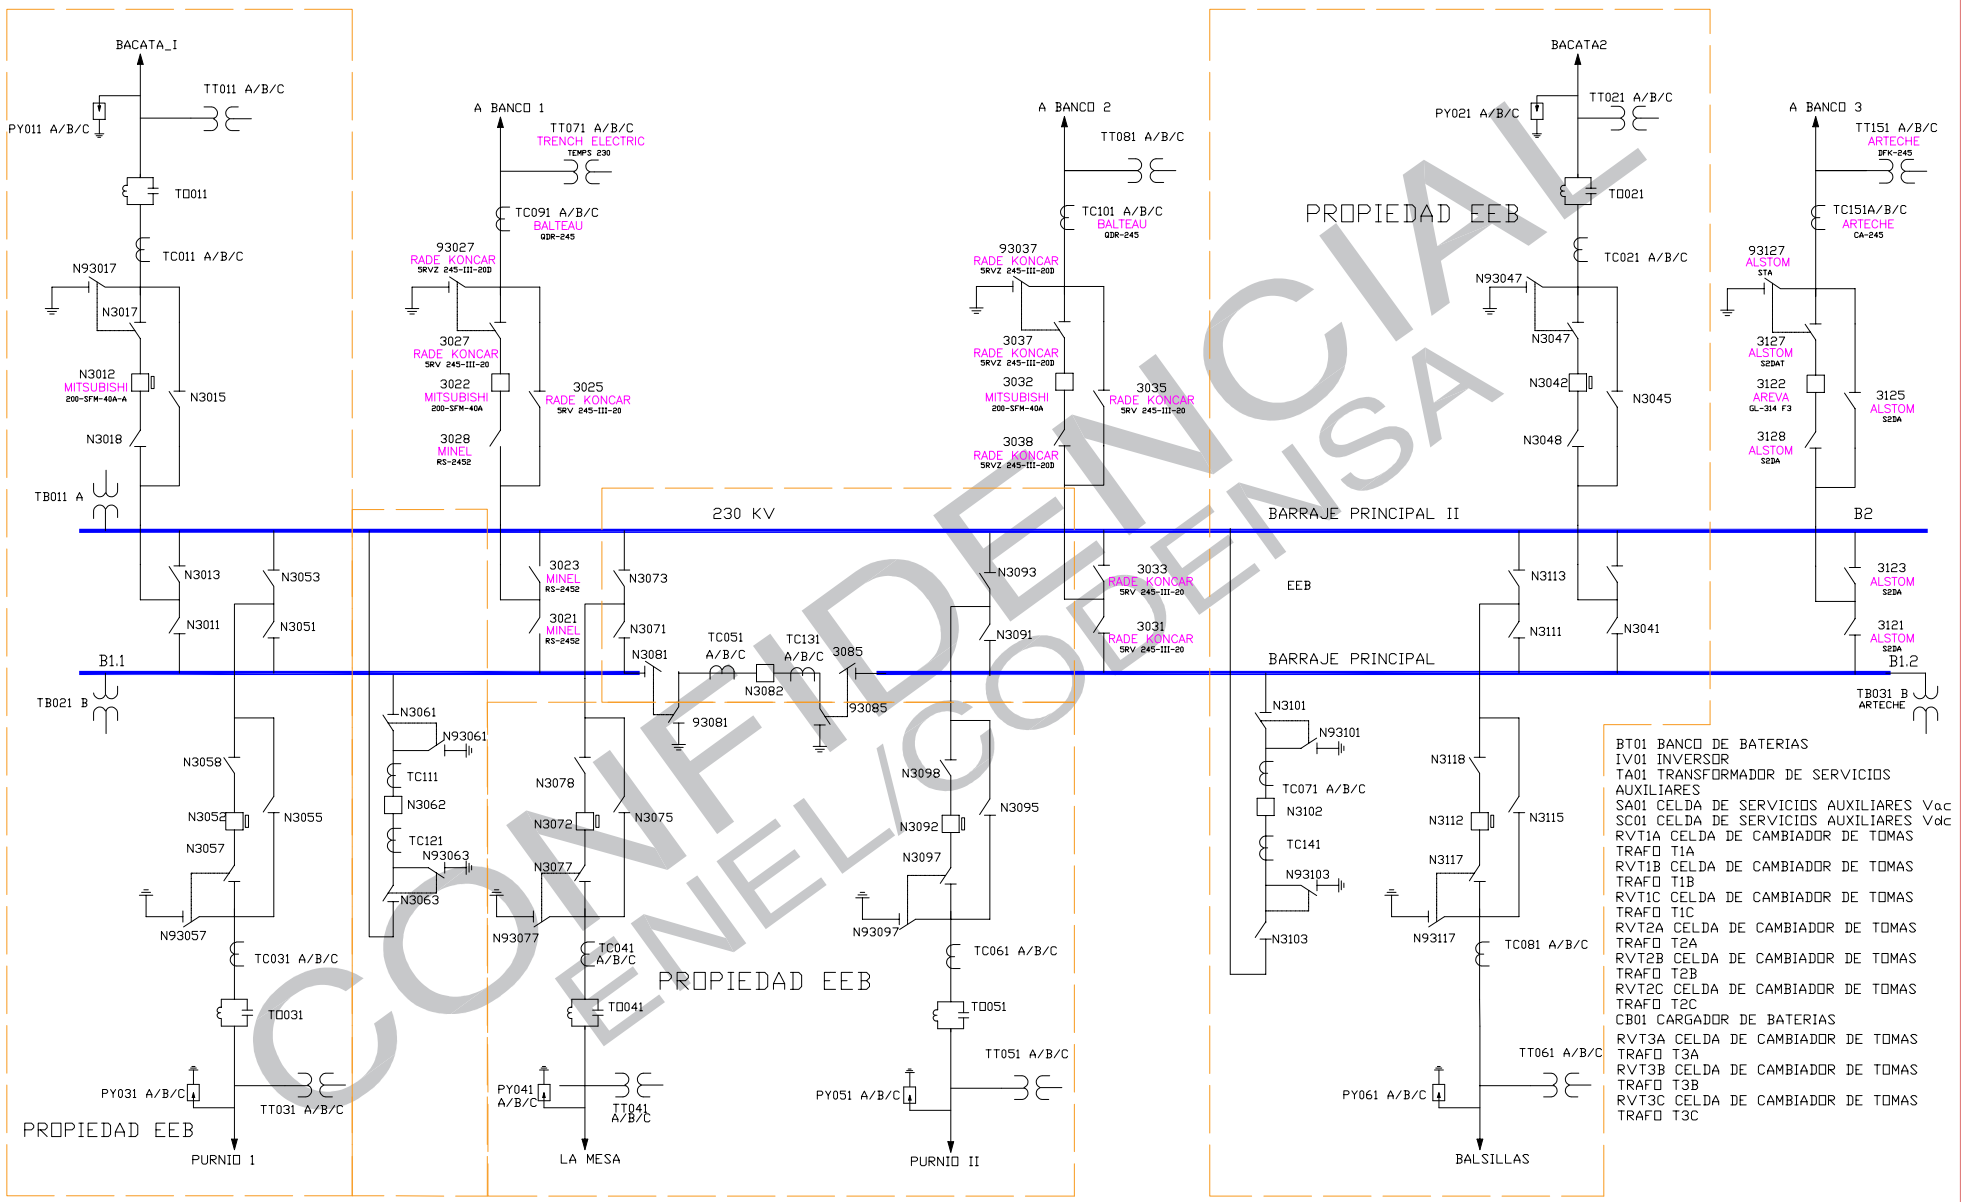

CONFIDENCIAL
ENEL/CODENSA

UNIDAD ORGANIZATIVA
ADMINISTRACIÓN INFORMACIÓN TECNICA COL.

REVISION No. 38

FECHA: ENERO/2023

ARCHIVO: NOROESTE1.DWG
C:\ESQUEMAS SUBESTACIONES\ESQUEMAS DEFINITIVOS

DIAGRAMA UNIFILAR

SUBESTACION NOROESTE
SIEMENS 6560 PLC763
VIA SUBACHOQUE

CODIGO: NO

128

HOJA: 1

DE: 3