
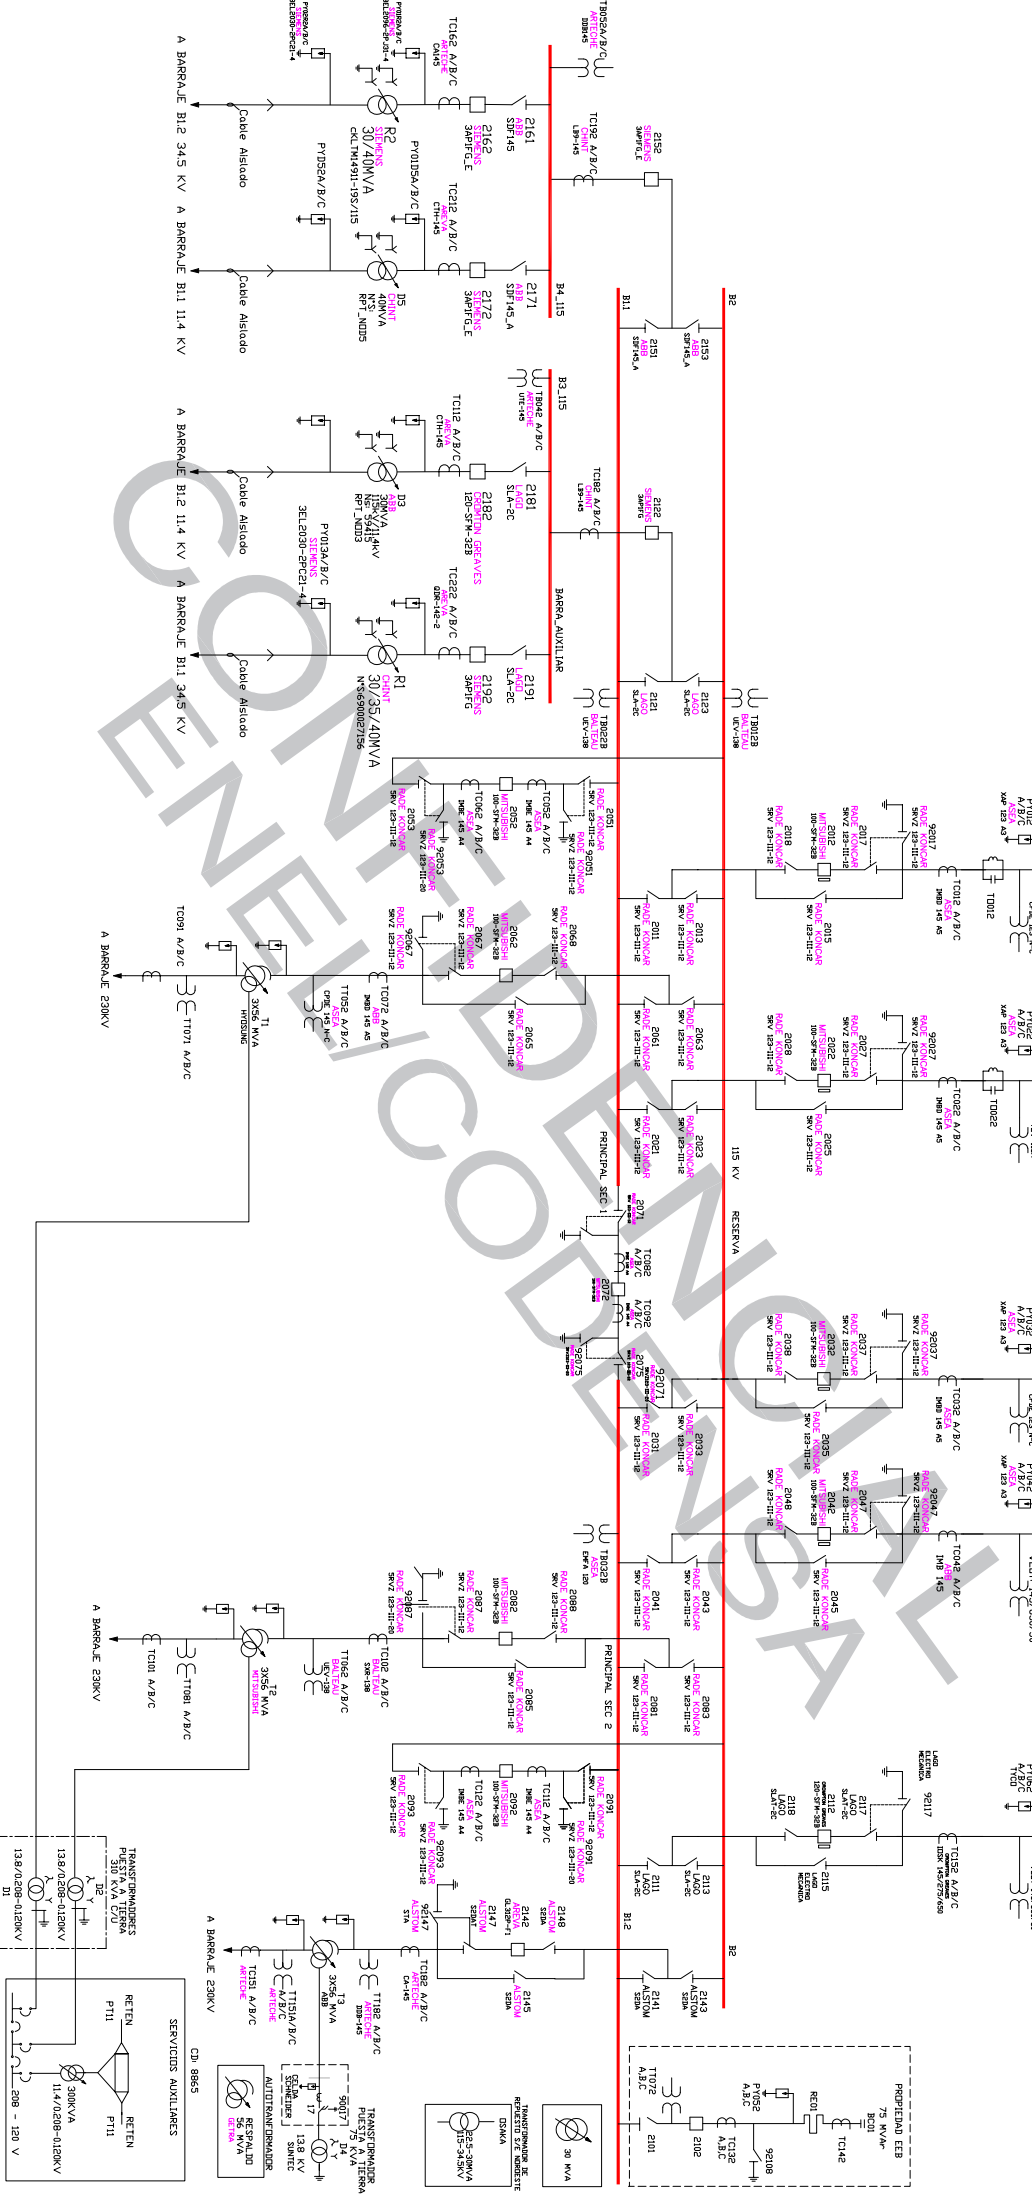


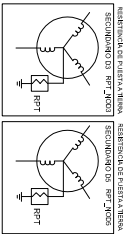

UNIDAD ORGANIZATIVA
ADMINISTRACION INFORMACION
TECNICA COL.

REVISION No. 38

FECHA: ENERO/2023

ARCHIVO: NOROESTE2.DWG
V:\FisServer\CONTROL UNIFILARES\UNIFILARES_MARZO_2019

DIAGRAMA UNIFILAR

SUBESTACION NOROESTE
SIEMENS 6560 PLC 763
VIA SUBAHOQUE

CODIGO: NO

128

HOJA: 2

DE: 3