


VIENE DEL TRAFORO 2 115/34.5 KV

VIENE DEL TRAFORO 5 115/11.4 KV



VIENE DEL TRAFORO 3 115/11.4 KV

VIENE DEL TRAFORO 1 115/34.5 KV

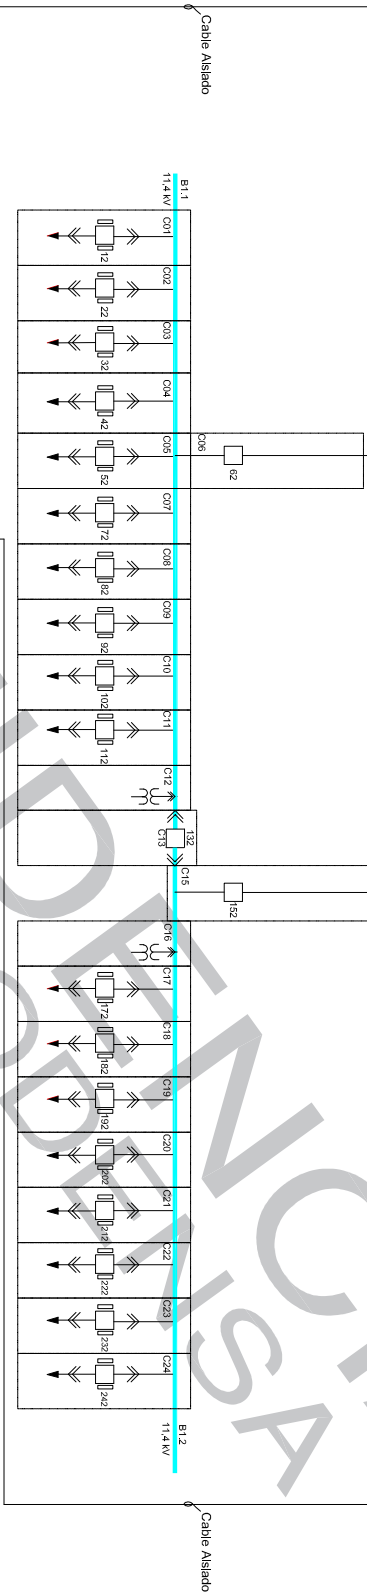

512	NO11R	EL_VINO	→	CO1R
522	NO12R	INDUL_80	→	CO2R
532	NO13R	LIBRE_NO13R	→	CO3R
542	NO14R	R1_CHINT_30MVA	→	CO4R
552	NO15R	NO_SAUX_2	→	CO5R
562	NO16R	LIBRE_NO16R	→	CO6R
572	NO17R	LIBRE_NO17R	→	CO7R
582	NO18R	LIBRE_NO18R	→	CO8R
592	NO19R	LIBRE_NO19R	→	CO9R
602	NO20R	LIBRE_NO20R	→	CO10R
612	NO21R	LIBRE_NO21R	→	CO11R
622	NO22R	LIBRE_NO22R	→	CO12R
632	NO23R	LIBRE_NO23R	→	CO13R
642	NO24R	LIBRE_NO24R	→	CO14R
652	NO25R	LIBRE_NO25R	→	CO15R
662	NO26R	LIBRE_NO26R	→	CO16R
672	NO27R	LIBRE_NO27R	→	CO17R

12	NO51	EL_CARO	→	CO1
22	NO52	METALCOM	→	CO2
32	NO53	JACALITO	→	CO3
42	NO54	ASAMBLEAS	→	CO4
52	NO55	ASERRIOS	→	CO5
62	NO56	D5_CHINT_40MVA	→	CO6
72	NO57	MALCUI	→	CO7
82	NO58	ESPAÑOLA	→	CO8
92	NO59	NO_SAUX_3	→	CO9
102	NO60	DIRECTV	→	CO10
112	NO61	LIBRE_NO61	→	CO11
122	NO62	LIBRE_NO62	→	CO12
132	NO63	LIBRE_NO63	→	CO13
142	NO64	LIBRE_NO64	→	CO14
152	NO65	LIBRE_NO65	→	CO15
162	NO66	LIBRE_NO66	→	CO16
172	NO67	LIBRE_NO67	→	CO17
182	NO68	LIBRE_NO68	→	CO18
192	NO69	LIBRE_NO69	→	CO19
202	NO70	LIBRE_NO70	→	CO20
212	NO71	LIBRE_NO71	→	CO21
222	NO72	LIBRE_NO72	→	CO22
232	NO73	LIBRE_NO73	→	CO23
242	NO74	LIBRE_NO74	→	CO24

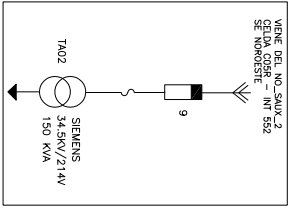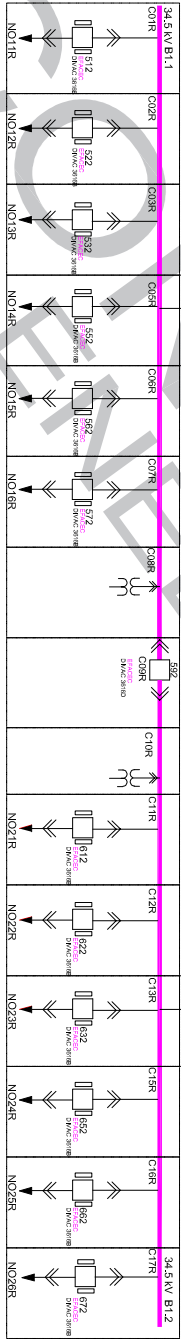

UNIDAD ORGANIZATIVA
ADMINISTRACIÓN INFORMACIÓN
TÉCNICA COL.

REVISIÓN No.

38

FECHA:

ENERO/2023

ARCHIVO:

NOROESTES3.DWG

C:\ESQUEMAS SUBESTACIONES\ESQUEMAS DEFINITIVOS

DIAGRAMA UNIFILAR

SUBESTACION NOROESTE

SIEMENS 6560 PLC763

VIA SUBCHOCQUE

CODIGO:

NO

DE:

3

128