


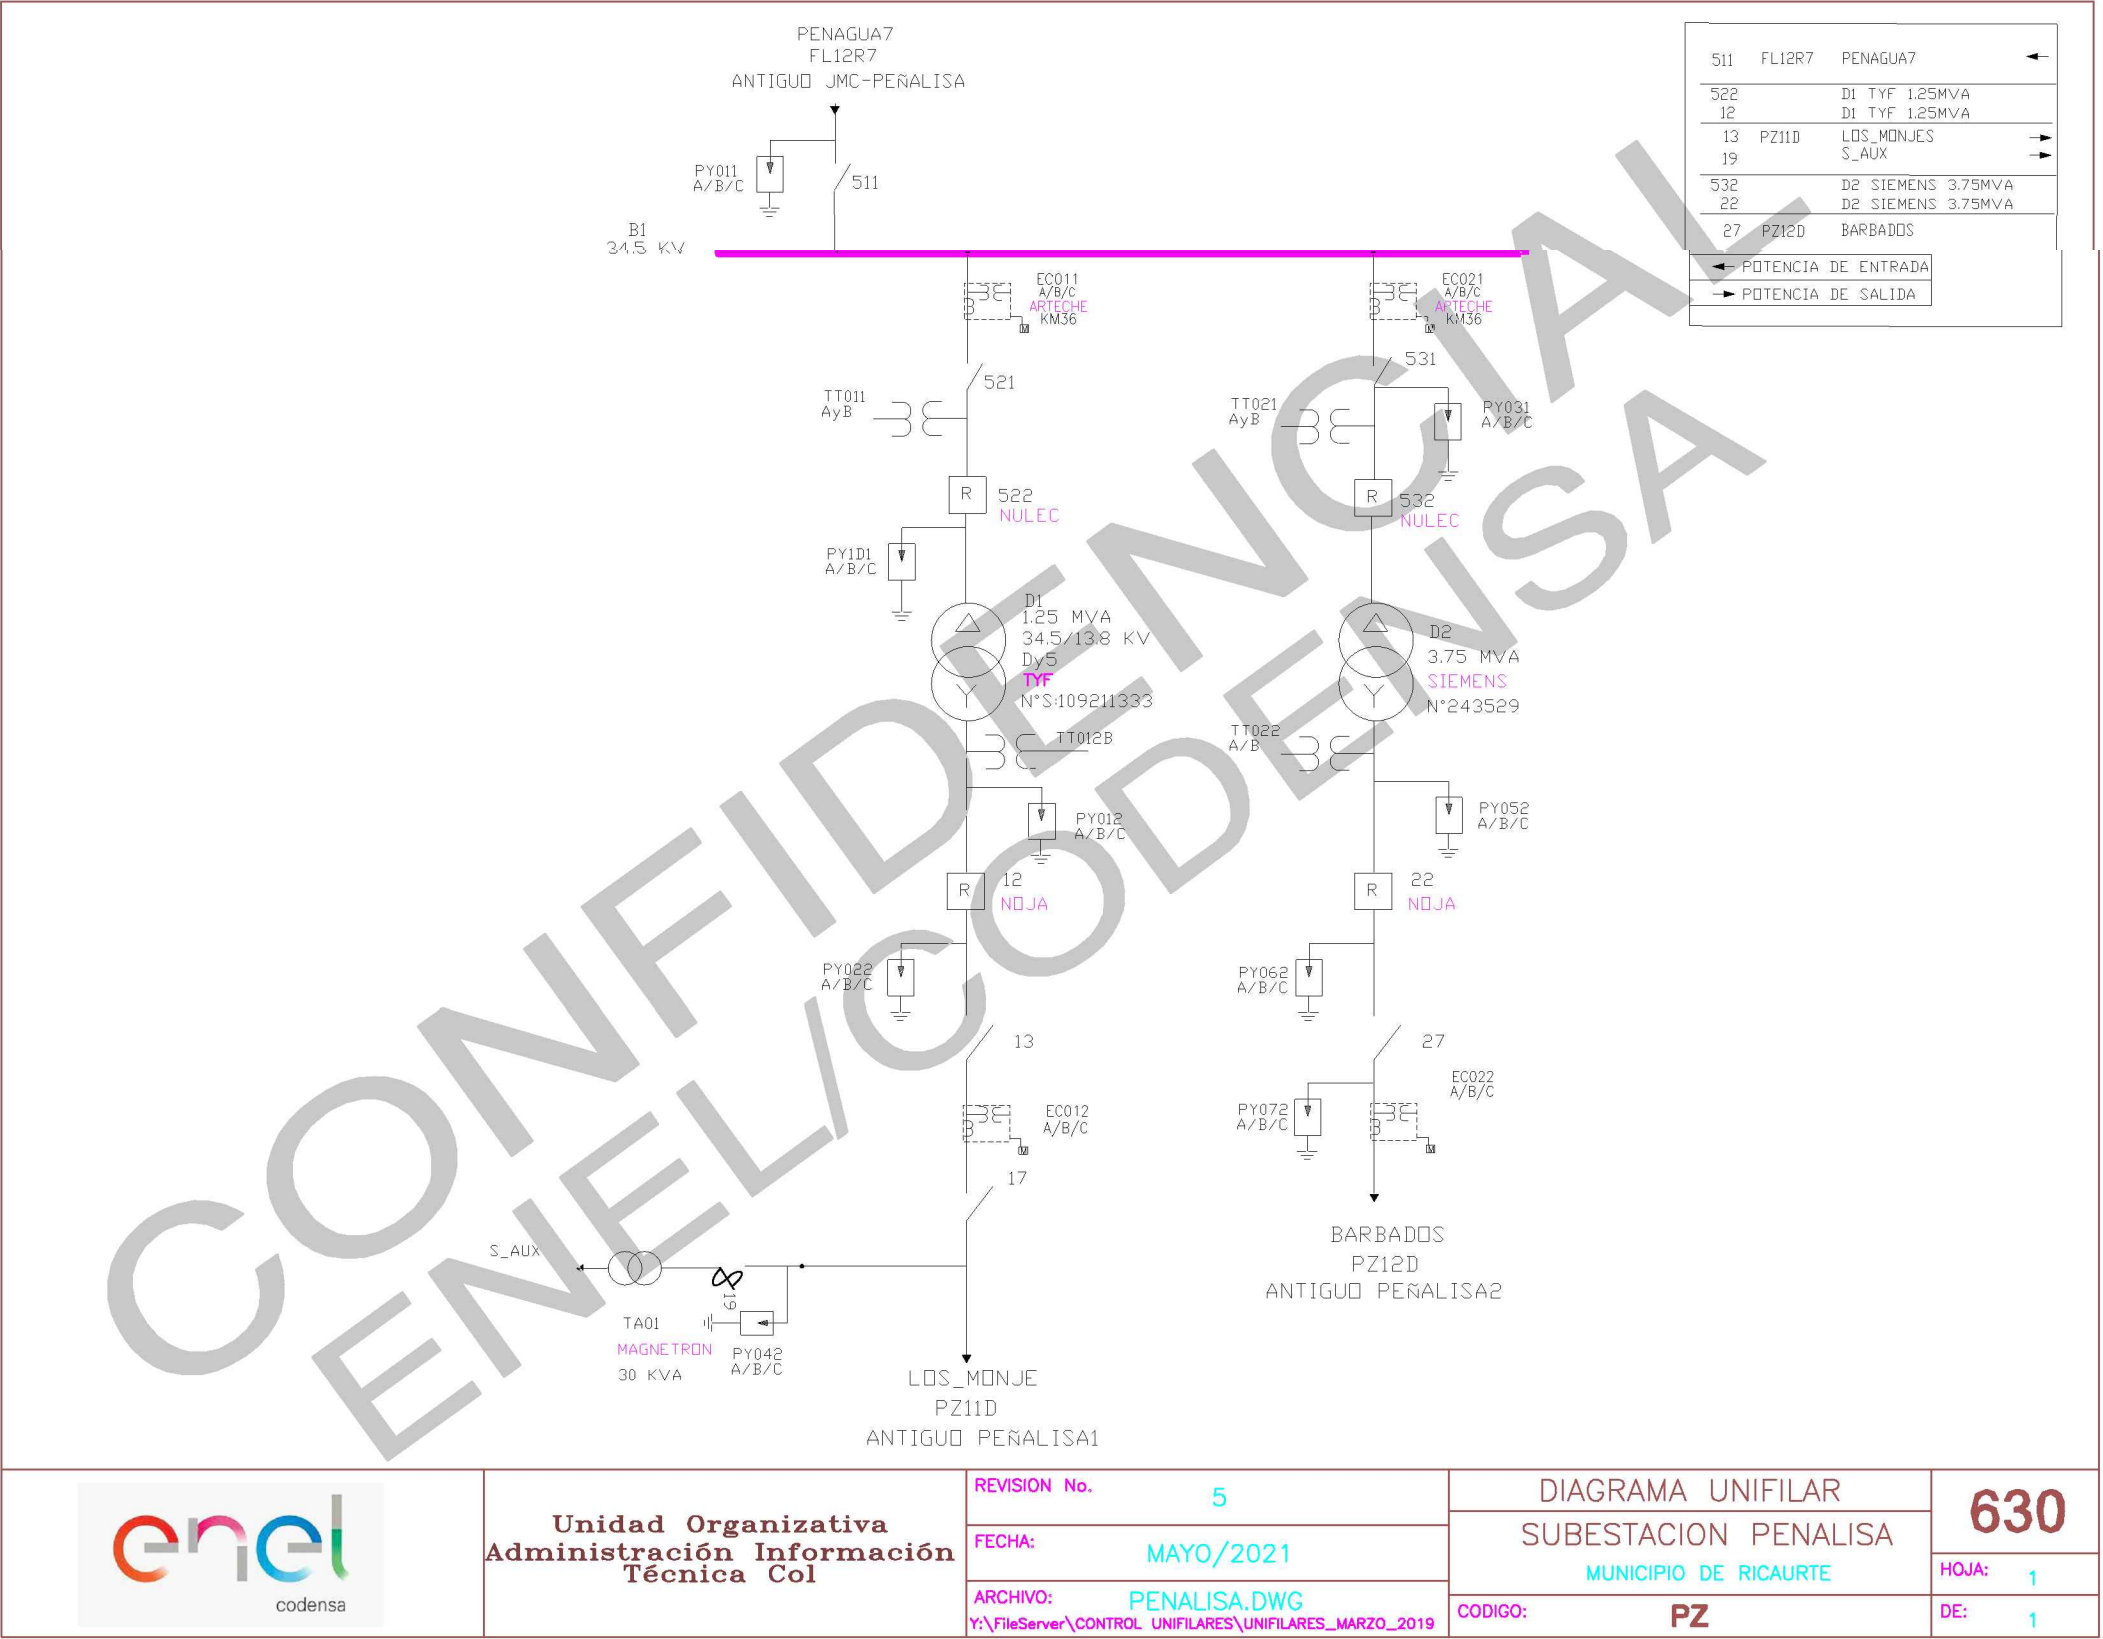

Unidad Organizativa
Administración Información
Técnica Col

REVISION No.	5
FECHA:	MAYO/2021
ARCHIVO:	PENALISA.DWG
Y:\FileServer\CONTROL UNIFILARES\UNIFILARES_MARZO_2019	

DIAGRAMA UNIFILAR
SUBESTACION PENALISA
MUNICIPIO DE RICAURTE
CODIGO: PZ

630
HOJA: 1
DE: 1