


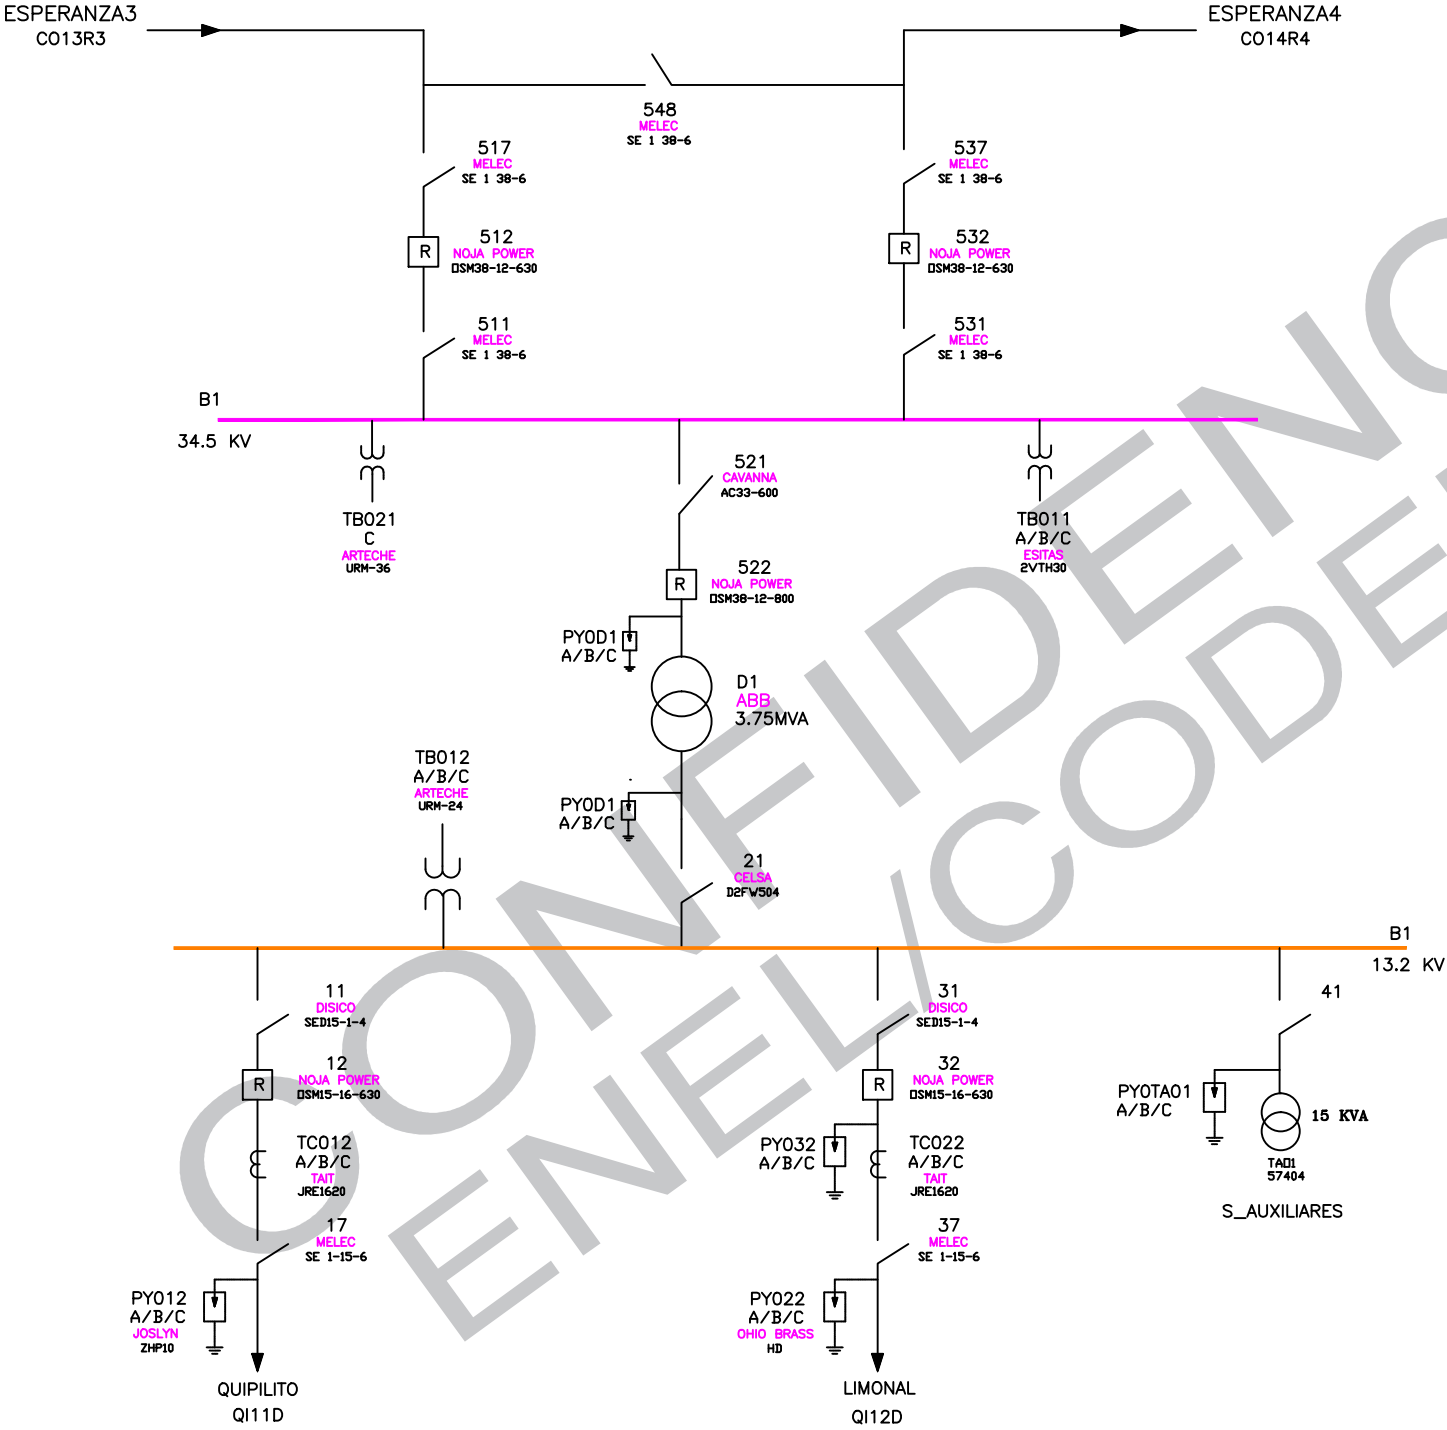

512	C013R3	ESPERANZA3	→
532	C014R4	ESPERANZA4	→
548		ACOPLE	
		MEDIDA B1	
		MEDIDA B1	
522		D1 ABB 2.5MVA	
21		D1 ABB 2.5MVA	
12	QI11D	QUIPILITO	→
		MEDIDA B1	
32	QI12D	LIMONAL	→
41		S_AUXILIARES	
← POTENCIA DE ENTRADA			
→ POTENCIA DE SALIDA			



Unidad Organizativa
Administración Información
Técnica Col.

REVISION No.	13
FECHA:	ENERO/2019
ARCHIVO:	QUIPILE.DWG \\COLC009FS01\FileServer\CONTROL UNIFILARES

DIAGRAMA UNIFILAR
SUBESTACION QUIPILE
MUNICIPIO QUIPILE, RUTA LA MESA SAN JOAQUIN Y QUIPILE
CODIGO: QI

95
HOJA: 1
DE: 1