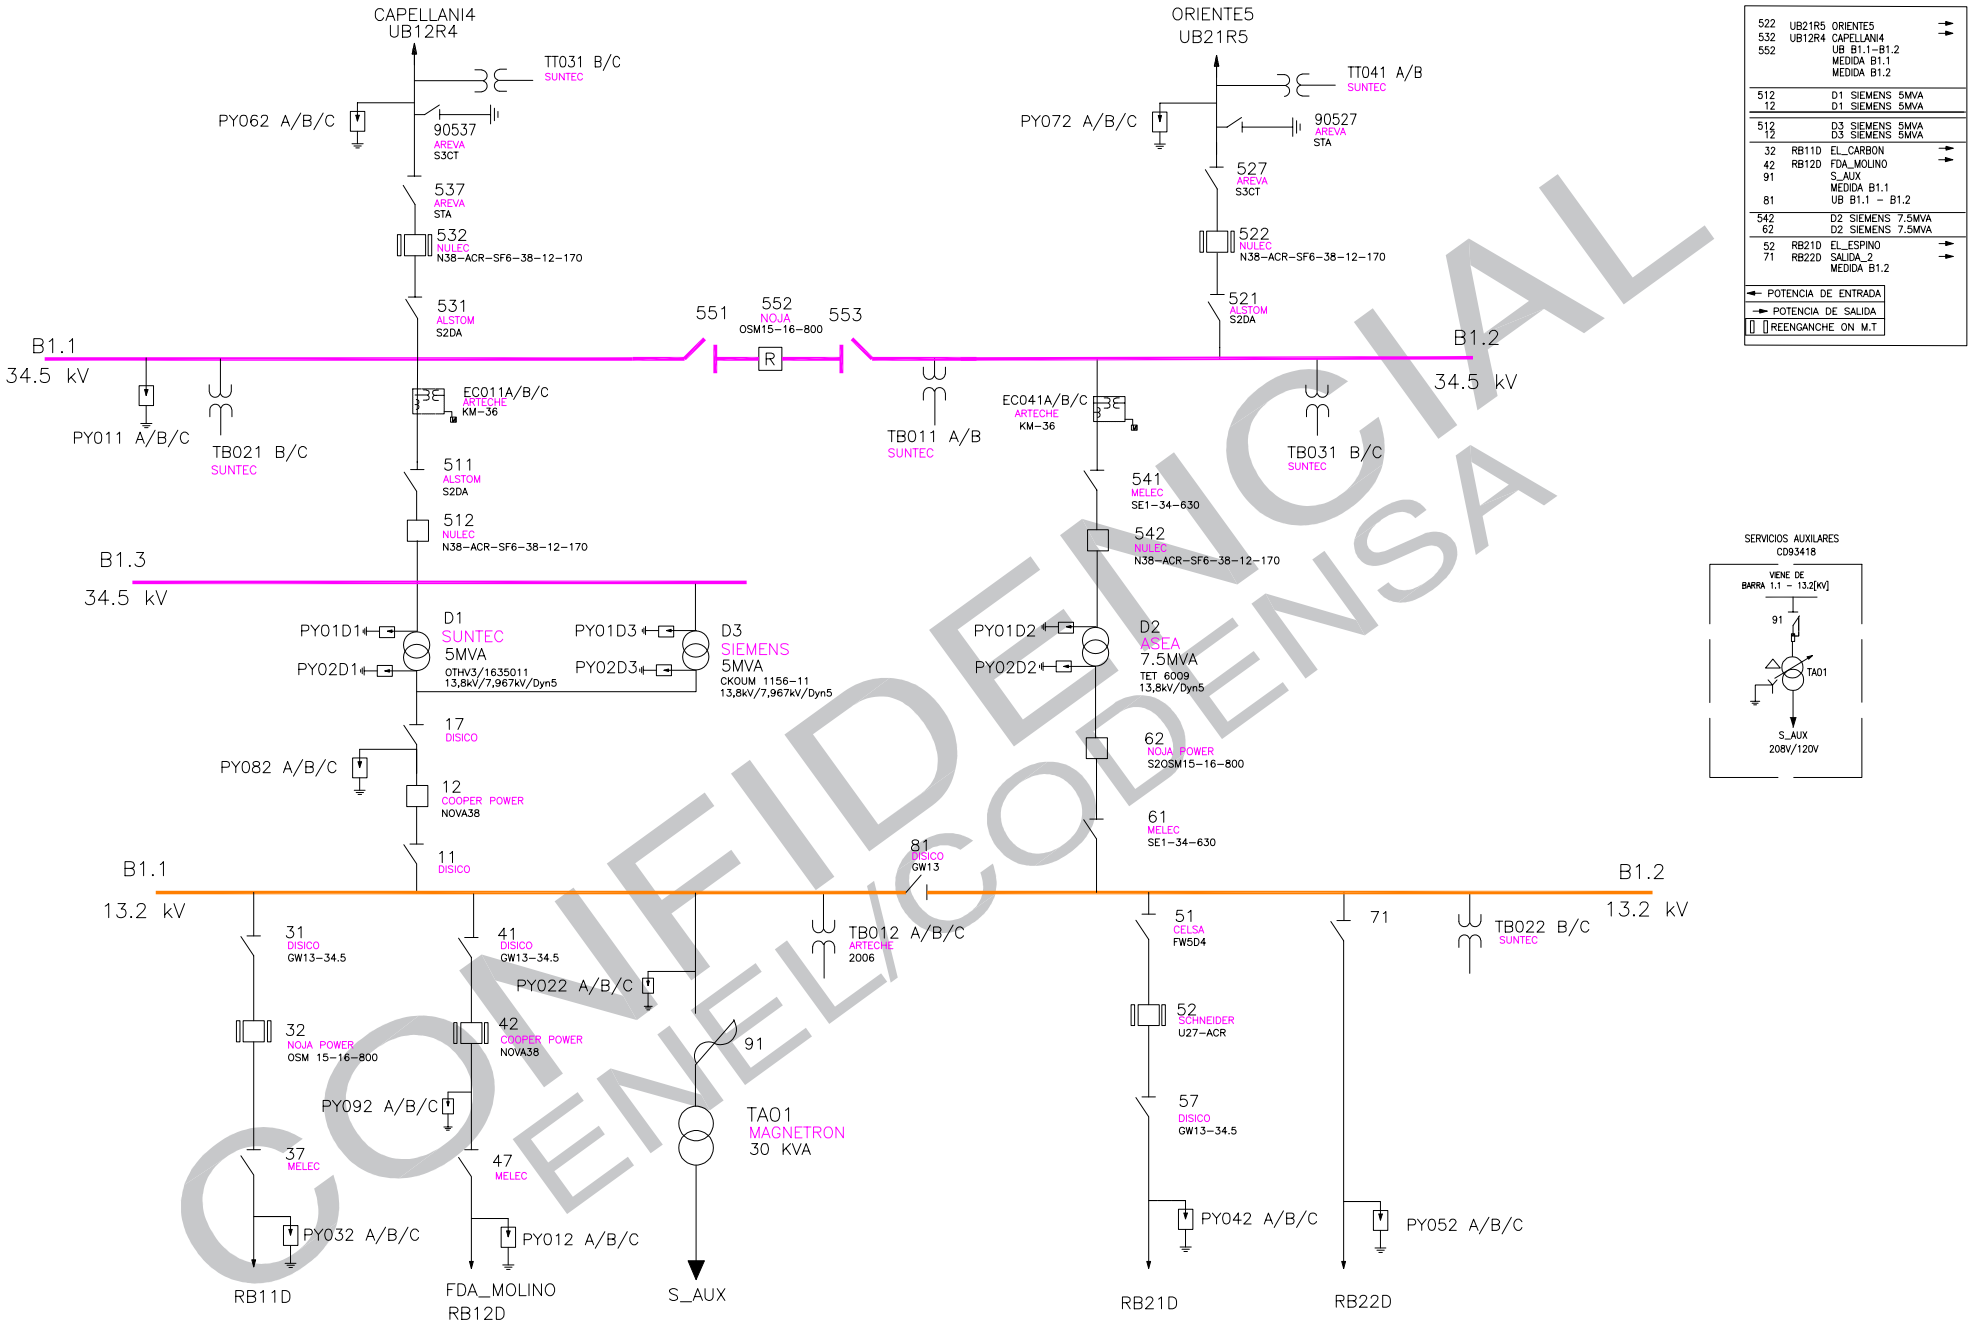

CONFIDENCIAL
ENEL/CODENSA

codensa

Unidad Organizativa
Administración Información
Técnica Col

REVISION No. 26
FECHA: OCTUBRE/2022
ARCHIVO: RABANAL.DWG
\\COLCOD09FS01\FileServer\CONTROL UNIFILARES

DIAGRAMA UNIFILAR
SUBESTACION RABANAL
V.RABANAL/M.GUACHETA
CODIGO: RB

130
HOJA: 1
DE: 1